

HỒ SƠ NỘI THẤT

CÔNG TRÌNH: S MADISON

HẠNG MỤC TẦNG 8

ĐỊA CHỈ: CĂN HỘ 8.03-04-05-06, 15 THI SÁCH, BẾN NGHÉ, QUẬN 1

PK MẶT BẰNG BỐ TRÍ NỘI THẤT PHÒNG KHÁCH

1:50 @ A3

- PK-01** TỦ TIVI:
- MẶT TỦ ỐP ĐÁ ĐEN
 - TỦ ỐP ACRYLIC CHAMPAGE
 - KHUNG SẮT GIA CỐ
- VÁCH TIVI:
- VÁCH ỐP ĐÁ XĂM

- PK-02** TỦ TRUNG BÀY:
- THÙNG MELAMINE + CẢNH KÍNH KHUNG NHÔM
 - ĐỢT KÍNH

- PB-01** TỦ BẾP:
- THÙNG MELAMINE
 - CẢNH KÍNH KHUNG NHÔM
 - CẢNH TỦ ACRYLIC XĂM ĐẬM

- PB-02** QUẦY BẾP:
- THÙNG MELAMINE
 - CẢNH ACRYLIC CHAMPAGE
 - MẶT BẾP ỐP ĐÁ ĐEN

- PB-03** TỦ ĐỪNG:
- THÙNG MELAMINE XĂM ĐẬM
 - CẢNH LAMINATE VÂN GỖ


- PB-04** ĐẢO BẾP:
- THÙNG MELAMINE XĂM ĐẬM
 - GỖ TỰ NHIÊN WALNUT KHUNG SẮT GIA CỐ
 - MẶT DỰNG ỐP ĐÁ XĂM

- S-01** TỦ GIÀY:
- THÙNG MELAMINE XĂM ĐẬM
 - CẢNH ACRYLIC, ĐÈN LED HẮT


- S-02** TỦ GIÀY:
- THÙNG MELAMINE XĂM ĐẬM
 - CẢNH LAMINATE VÂN GỖ, ĐÈN LED HẮT

- S-03** TỦ GIÀY:
- THÙNG MELAMINE XĂM ĐẬM
 - ĐỢT MELAMINE XĂM
 - HẬU LAMINATE VÂN GỖ, ĐÈN LED HẮT


- S-03** TỦ GIÀY:
- THÙNG MELAMINE XĂM ĐẬM
 - ĐỢT MELAMINE XĂM
 - HẬU LAMINATE VÂN GỖ, ĐÈN LED HẮT

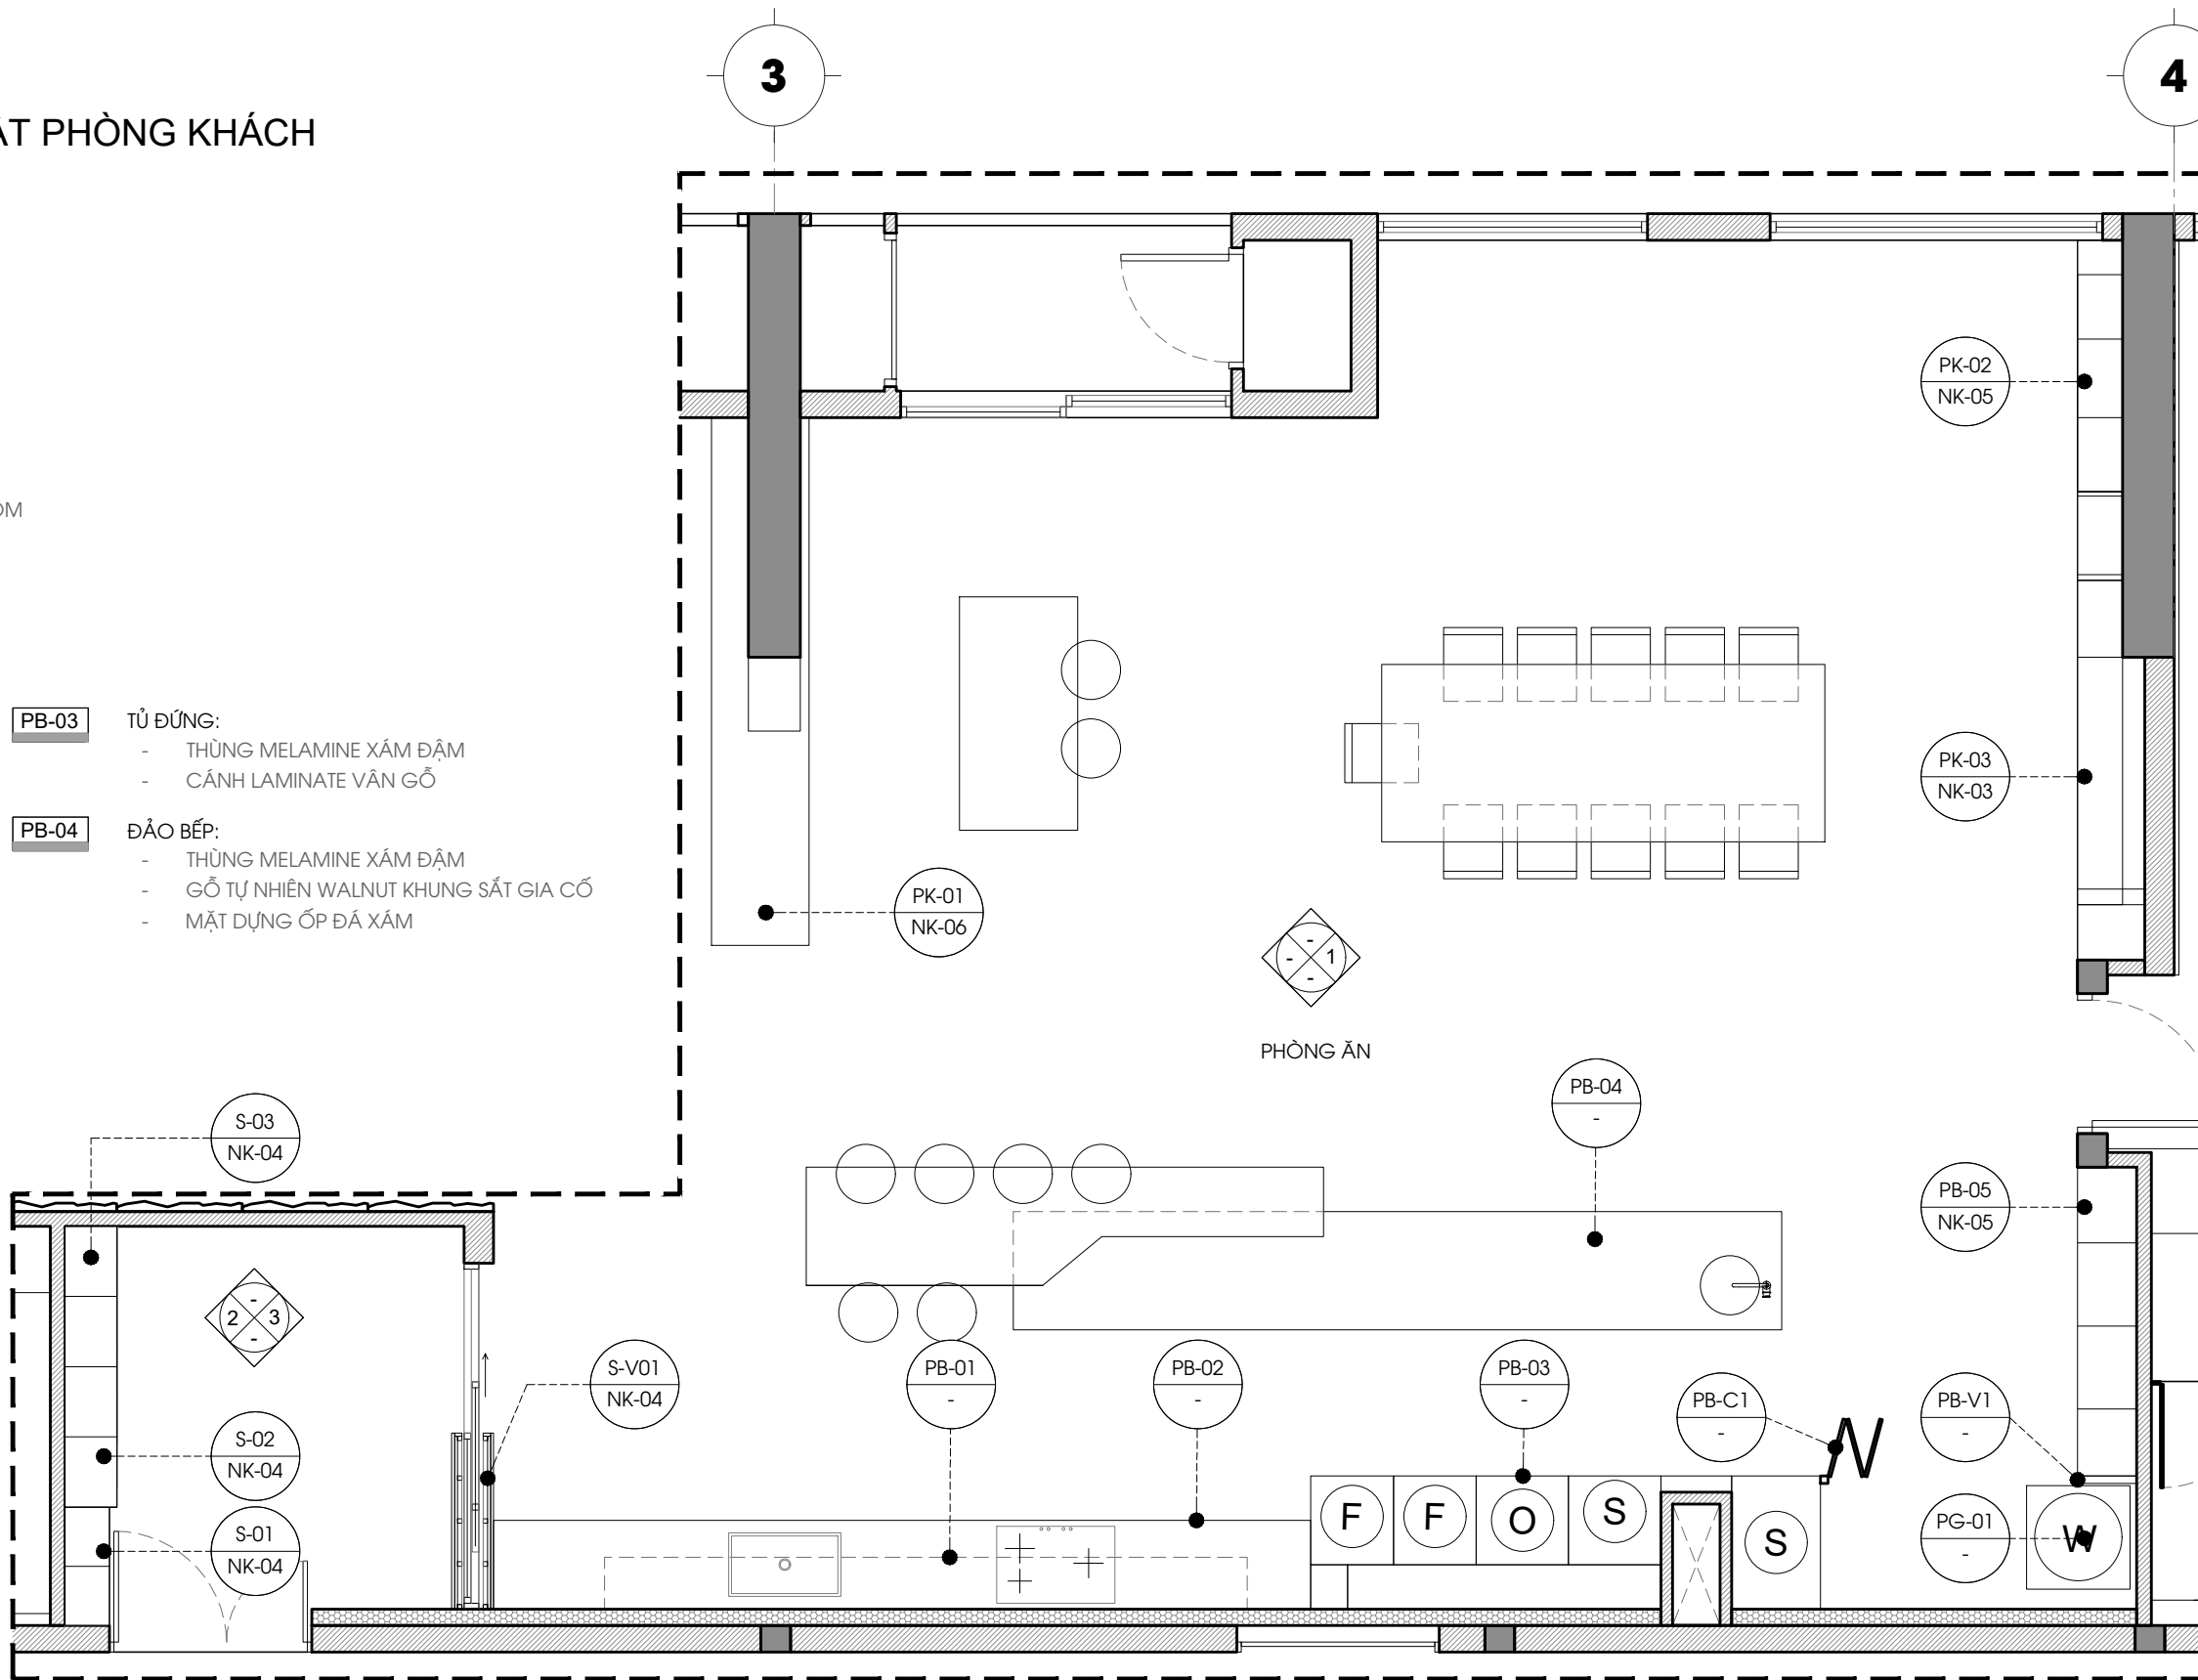


PHÁT HÀNH		HIỆU CHÍNH		GHI CHÚ	ARCHITECTURAL DESIGN — THIẾT KẾ KIẾN TRÚC		DESIGNER - CHỦ TRÌ THIẾT KẾ		PROJECT TITLE - TÊN DỰ ÁN		DATE - NGÀY	
					CÔNG TY TNHH KIẾN TRÚC VIỆT VACO DESIGN LẦU 1, 38/6 PHAN VĂN ĐẠT - P. BẾN NGHÉ - Q.1 - TP. HCM TEL: +84-9-36223364 EMAIL: info@vacodesign.com				CĂN HỘ 08.03- 08.04-08.05-08.06		03 - 2025	
									SCALE - TỈ LỆ			
									1:50			
									DRAWING TITLE - TÊN BẢN VẼ		DRAWING NO. - SỐ HIỆU BẢN VẼ	
									MẶT BẰNG BỐ TRÍ NỘI THẤT PHÒNG KHÁCH		NK-01	
				- MỌI KÍCH THƯỚC CẦN ĐƯỢC KIỂM TRA THEO THỰC TẾ CÔNG TRƯỜNG	ThS.KTS. ĐỖ QUỐC HIỆP		ThS.KTS. ĐỖ QUỐC HIỆP				KÝ HIỆU BẢN VẼ	
					ThS.KTS. ĐỖ QUỐC HIỆP		KTS. TRẦN TRUNG KIẾN					

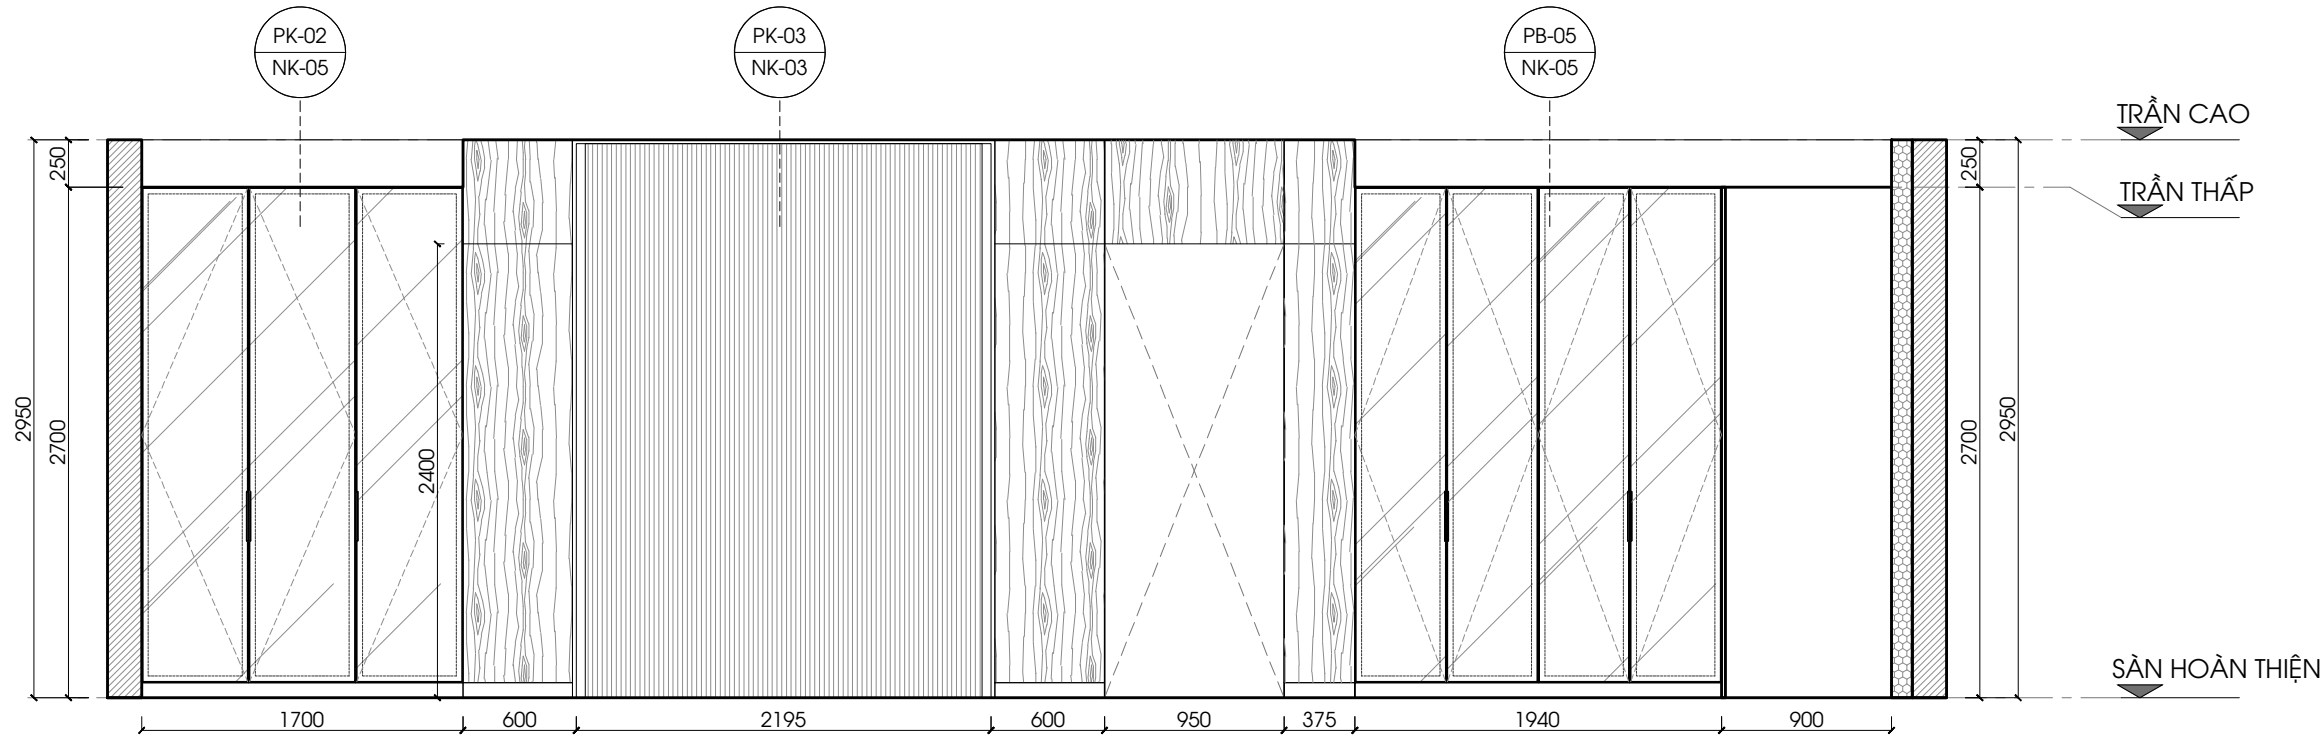

MẶT ĐỨNG 1
1:40 @A3

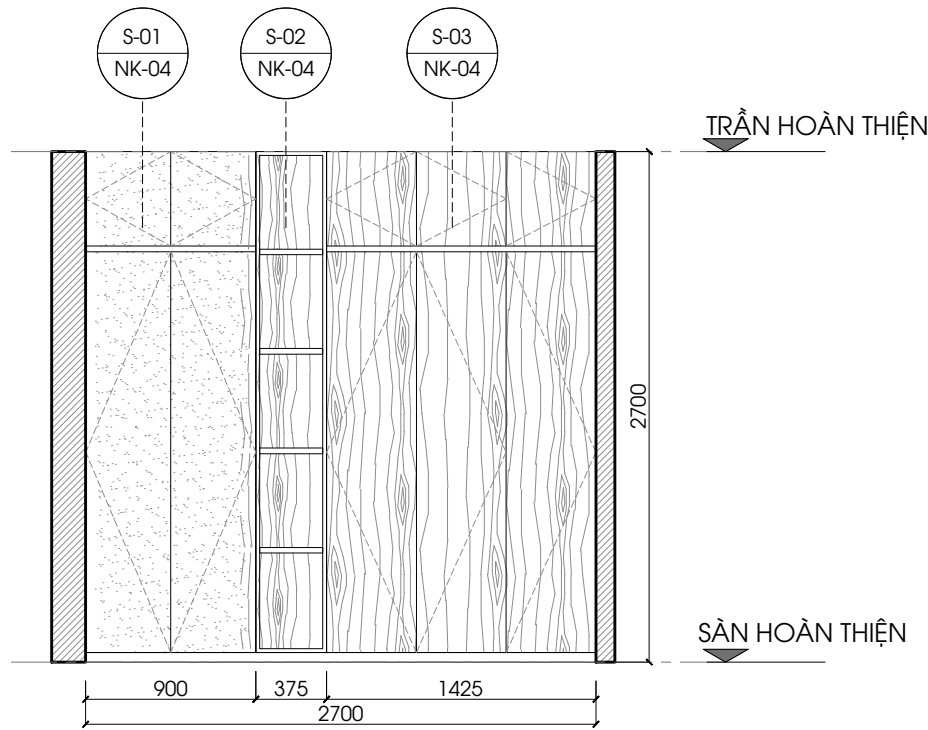


MẶT ĐỨNG 2
1:40 @A3

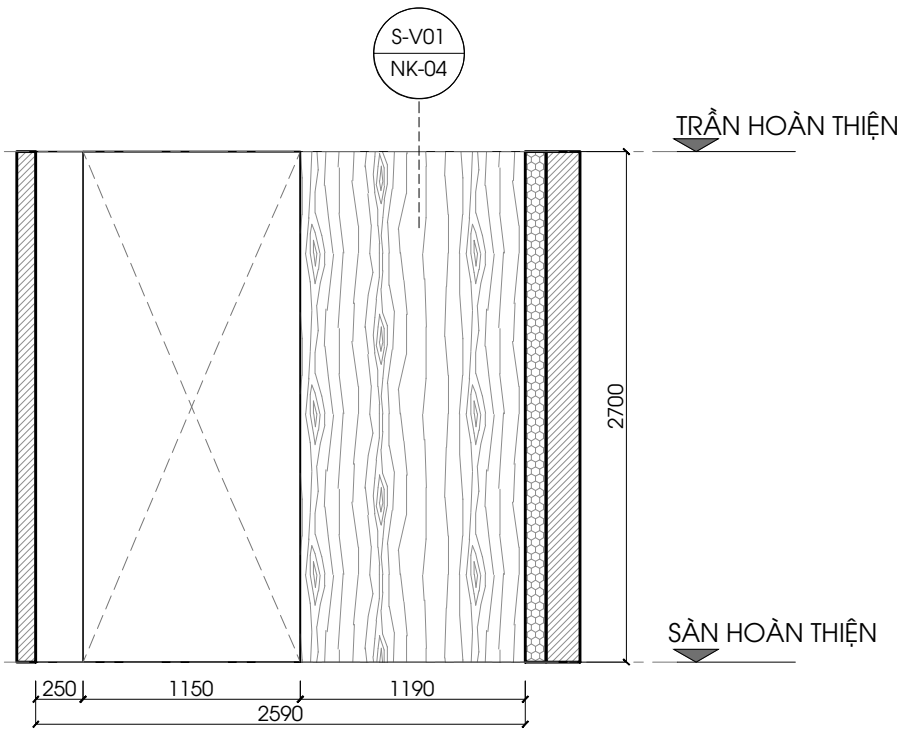


MẶT ĐỨNG 3
1:40 @A3


PHÁT HÀNH		HIỆU CHÍNH		GHI CHÚ	ARCHITECTURAL DESIGN — THIẾT KẾ KIẾN TRÚC		DESIGNER - CHỦ TRÌ THIẾT KẾ	PROJECT TITLE - TÊN DỰ ÁN	DATE - NGÀY				
					- MỌI KÍCH THƯỚC CẦN ĐƯỢC KIỂM TRA THEO THỰC TẾ CÔNG TRƯỜNG	CÔNG TY TNHH KIẾN TRÚC VIỆT VACO DESIGN LẦU 1, 3bis PHAN VĂN ĐẠT - P. BẾN NGHÉ - Q.1 - TP. HCM TEL: +84-9-36223364 EMAIL: info@vacodesign.com	ThS.KTS. ĐỖ QUỐC HIỆP	CĂN HỘ 08.03- 08.04-08.05-08.06	03 - 2025				
									SCALE - TỈ LỆ				
									1:40				
									DIRECTOR - GIÁM ĐỐC	DRAWN BY - NGƯỜI VẼ	DRAWING TITLE - TÊN BẢN VẼ	DRAWING NO. - SỐ HIỆU BẢN VẼ	KÝ HIỆU BẢNG VẼ
									ThS.KTS. ĐỖ QUỐC HIỆP	KTS. TRẦN TRUNG KIẾN	MẶT ĐỨNG 1 MẶT ĐỨNG 2,3	NK-02	N

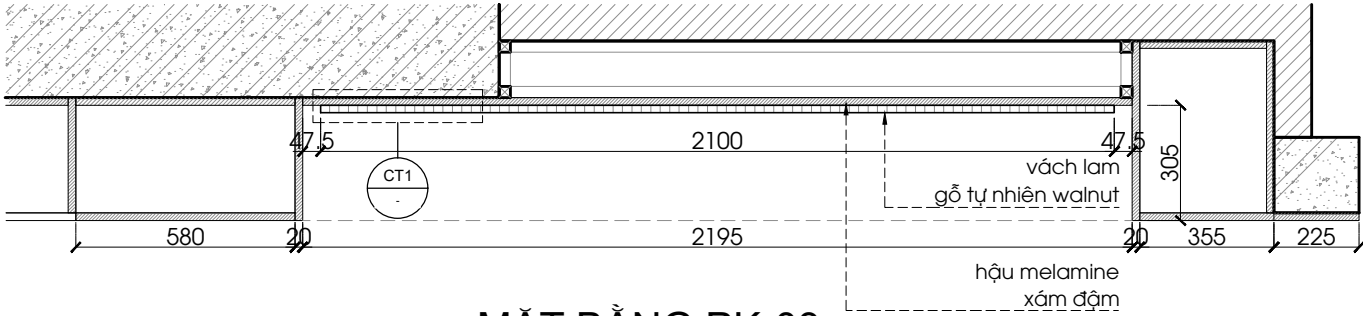

MẶT BẰNG PK-03
1:20 @A3

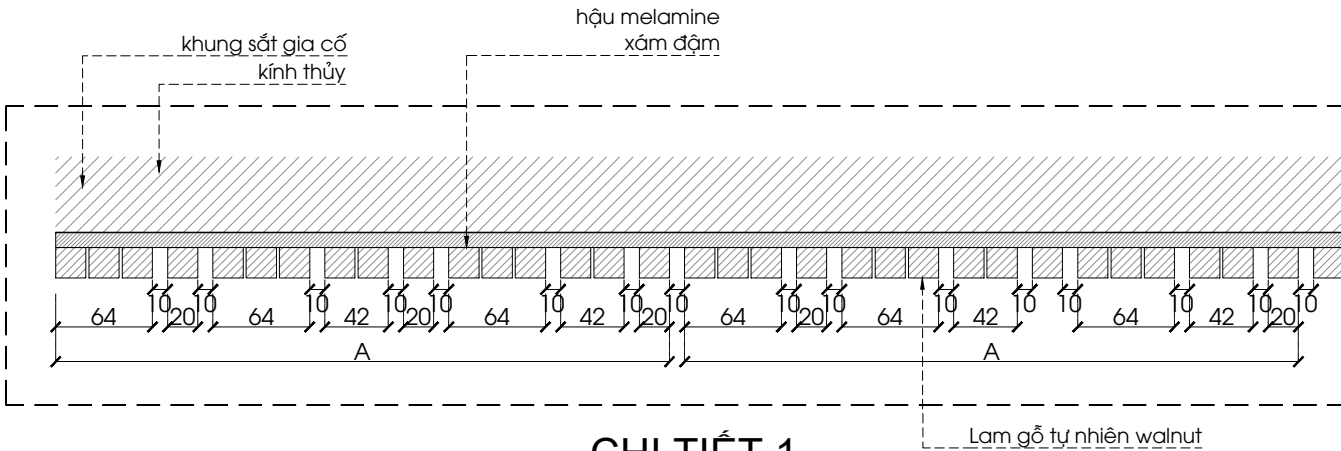


CHI TIẾT 1

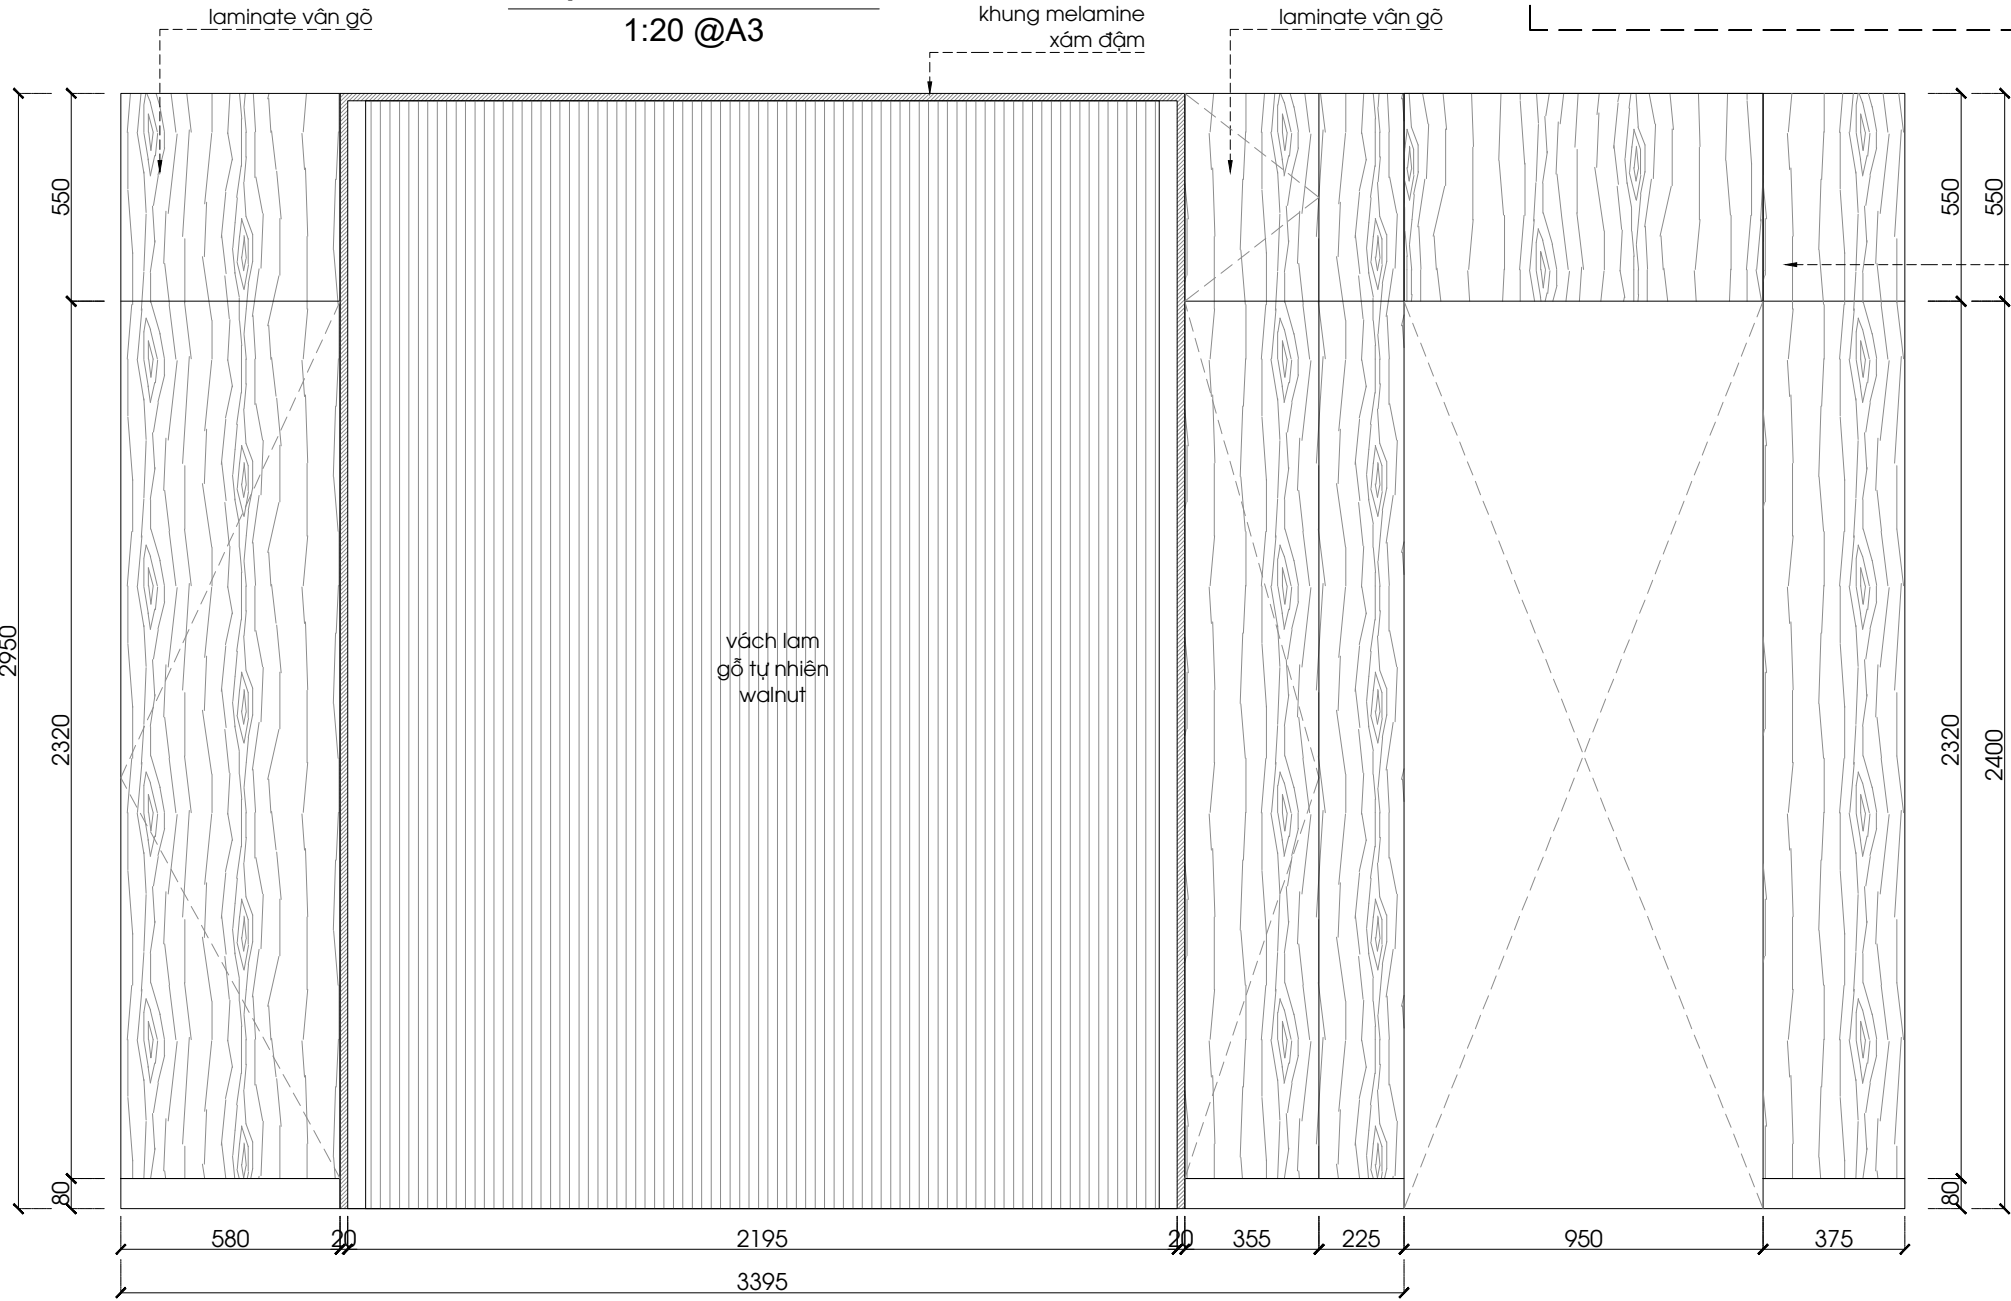


MẶT ĐỪNG PK-03
1:20 @A3

PHÁT HÀNH		HIỆU CHÍNH		GHI CHÚ	ARCHITECTURAL DESIGN — THIẾT KẾ KIẾN TRÚC		DESIGNER - CHỦ TRÌ THIẾT KẾ		PROJECT TITLE - TÊN DỰ ÁN		DATE - NGÀY	
					- MỌI KÍCH THƯỚC CẦN ĐƯỢC KIỂM TRA THEO THỰC TẾ CÔNG TRƯỜNG	CÔNG TY TNHH KIẾN TRÚC VIỆT VACO DESIGN LẦU 1, 3bis PHAN VĂN DAT - P. BẾN NGHÉ - Q.1 - TP. HCM TEL: +84-9-36223384 EMAIL: info@vacodesign.com	ThS.KTS. ĐỖ QUỐC HIỆP	CĂN HỘ 08.03- 08.04-08.05-08.06	03 - 2025	SCALE - TỈ LỆ 1:20		
				DIRECTOR - GIÁM ĐỐC	DRAWN BY - NGƯỜI VẼ		DRAWING TITLE - TÊN BẢN VẼ		DRAWING NO. - SỐ HIỆU BẢN VẼ	KÝ HIỆU BẢNG VẼ		
				ThS.KTS. ĐỖ QUỐC HIỆP	KTS. TRẦN TRUNG KIẾN		CHI TIẾT PK-03		NK-03	N		

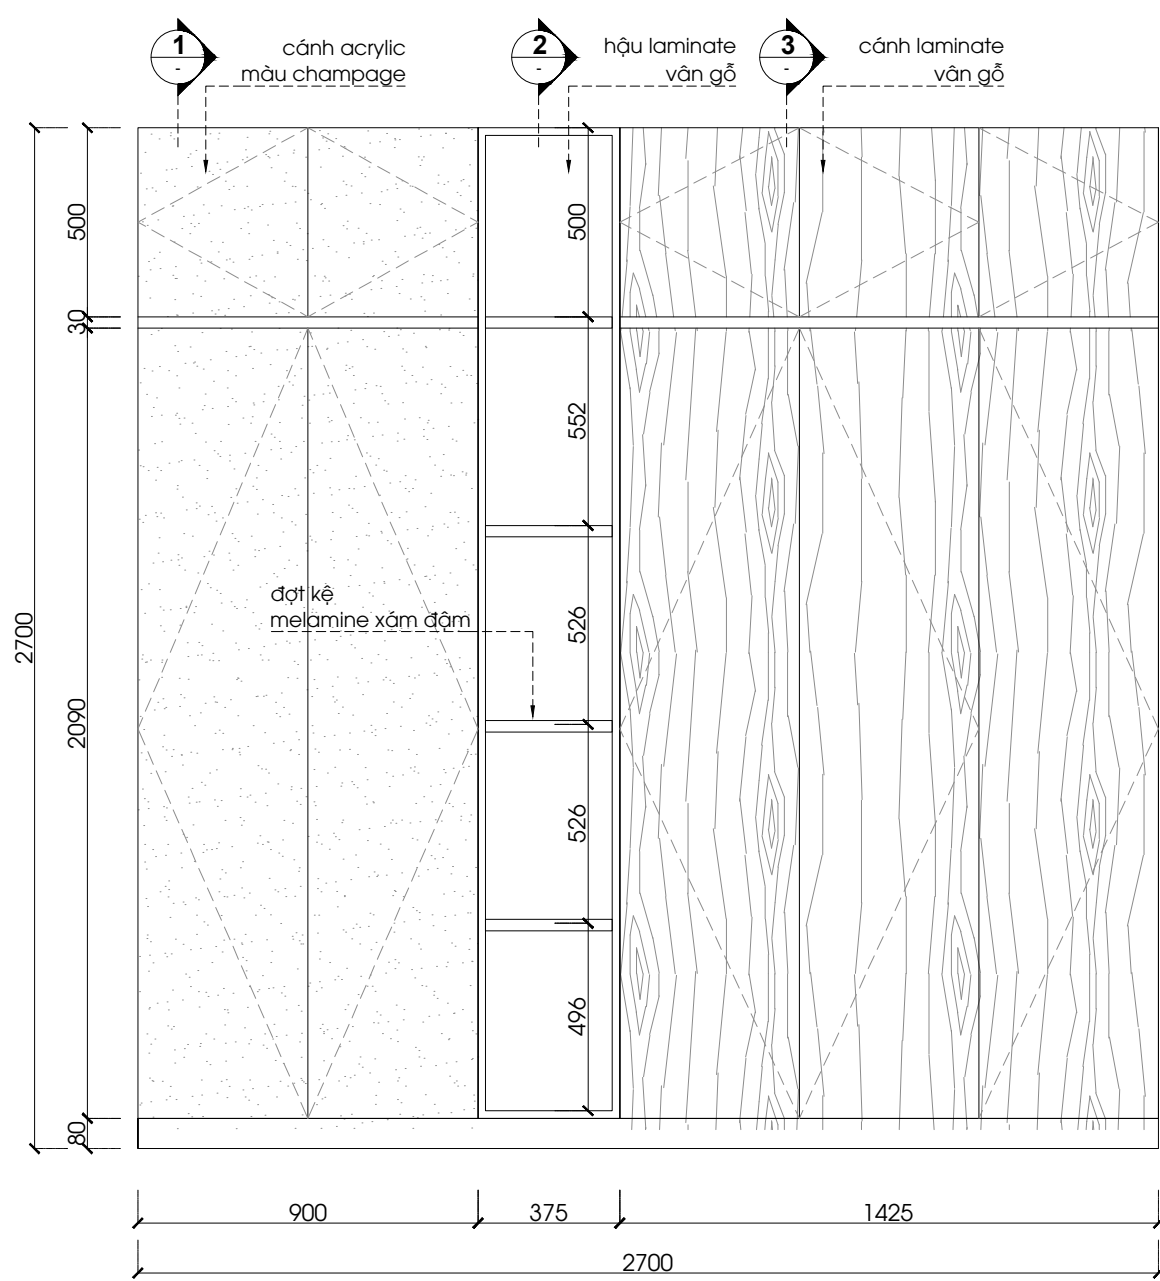


MẶT ĐỨNG S-01,02,03
1:20 @A3

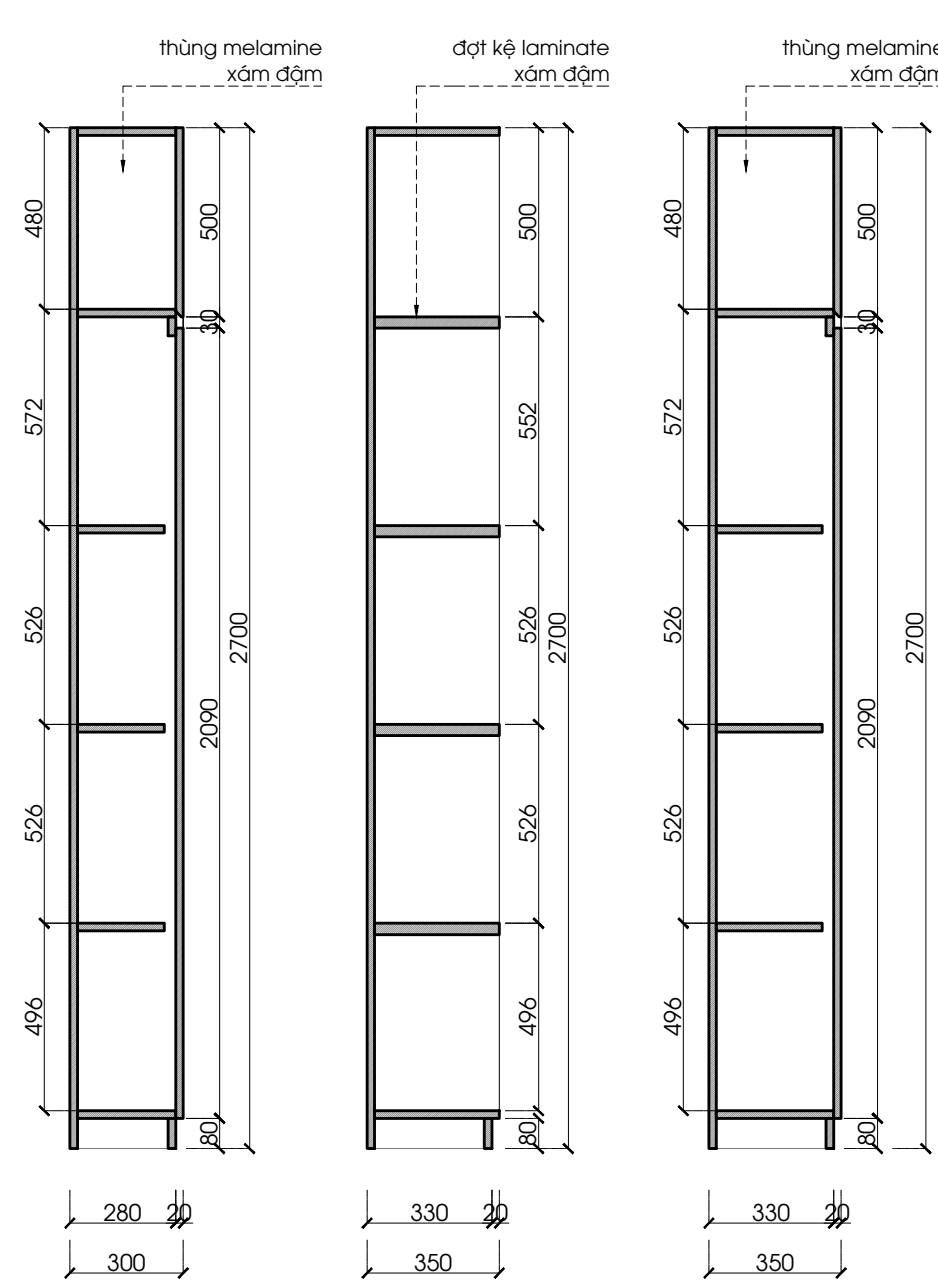


MẶT CẮT S-01
1:20 @A3

MẶT CẮT S-02
1:20 @A3

MẶT CẮT S-03
1:20 @A3

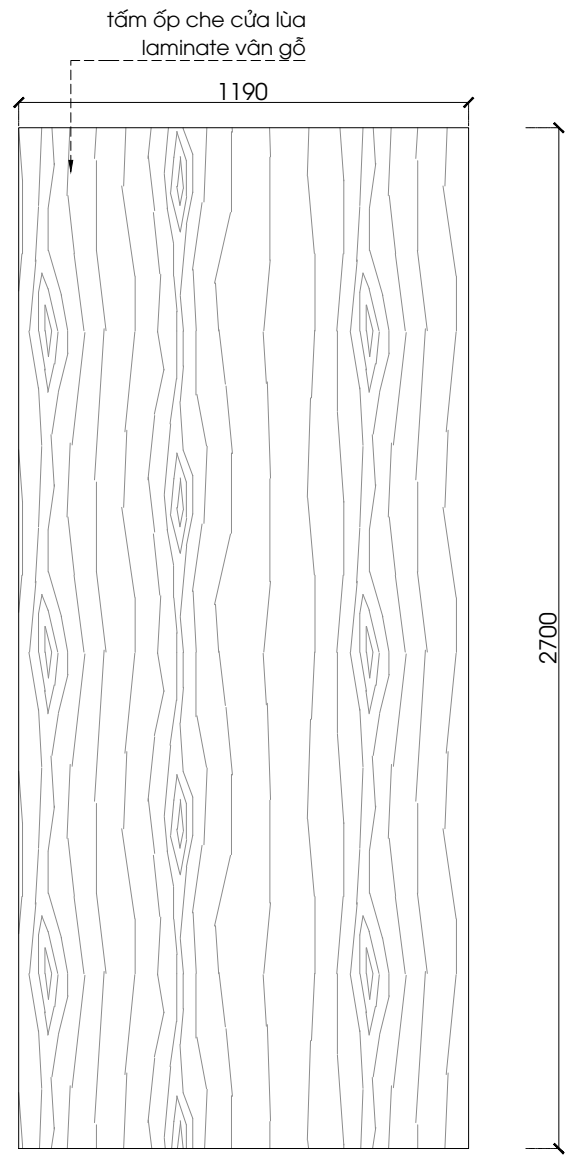

MẶT ĐỨNG S-V01
1:20 @A3

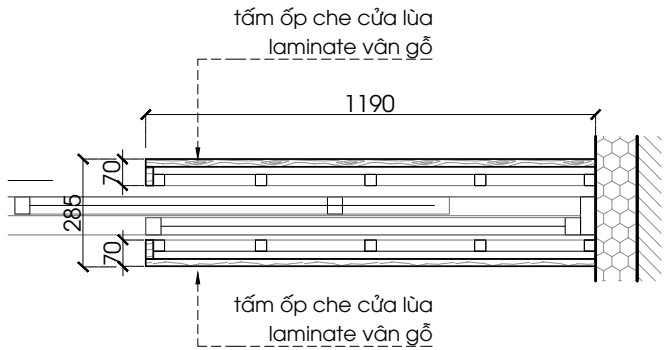


MẶT BẰNG S-V01
1:20 @A3


PHÁT HÀNH		HIỆU CHÍNH		GHI CHÚ - MỌI KÍCH THƯỚC CẦN ĐƯỢC KIỂM TRA THEO THỰC TẾ CÔNG TRƯỜNG	ARCHITECTURAL DESIGN — THIẾT KẾ KIẾN TRÚC  CÔNG TY TNHH KIẾN TRÚC VIỆT VACO DESIGN LẦU 1, 3bis PHAN VĂN ĐẠT - P. BẾN NGHÉ - Q.1 - TP. HCM TEL: +84-9-36223364 EMAIL: info@vacodesign.com		DESIGNER - CHỦ TRÌ THIẾT KẾ		PROJECT TITLE - TÊN DỰ ÁN		DATE - NGÀY 03 - 2025	
					DIRECTOR - GIÁM ĐỐC ThS.KTS. ĐỖ QUỐC HIỆP	ThS.KTS. ĐỖ QUỐC HIỆP	CĂN HỘ 08.03- 08.04-08.05-08.06	SCALE - TỈ LỆ 1:20				
					DRAWN BY - NGƯỜI VẼ	DRAWING TITLE - TÊN BẢN VẼ	DRAWING NO. - SỐ HIỆU BẢN VẼ	KÝ HIỆU BẢNG VẼ				
				ThS.KTS. ĐỖ QUỐC HIỆP	KTS. TRẦN TRUNG KIẾN	CHI TIẾT S-01,02,03,S-V1	NK-04	N				



PHÁT HÀNH		HIỆU CHỈNH		GHI CHÚ	ARCHITECTURAL DESIGN — THIẾT KẾ KIẾN TRÚC CÔNG TY TNHH KIẾN TRÚC VIỆT VACO DESIGN LẦU 1, 3b/1a PHAN VĂN DAT - P. BẾN NGHÉ - Q.1 - TP. HCM TEL: +84-9-38223384 EMAIL: info@vacodesign.com	DESIGNER - CHỦ TRÌ THIẾT KẾ	PROJECT TITLE - TÊN DỰ ÁN	DATE - NGÀY	
								03 - 2025	
								SCALE - TỈ LỆ	
								1:20	
								DRAWING NO. - SỐ HIỆU BẢN VẼ	KÝ HIỆU BẢNG VẼ
				DIRECTOR - GIÁM ĐỐC	DRAWN BY - NGƯỜI VẼ	DRAWING TITLE - TÊN BẢN VẼ	NK-05	N	
				ThS.KTS. ĐỖ QUỐC HIỆP	KTS. TRẦN TRUNG KIÊN	CHI TIẾT PK-02, PB-05			

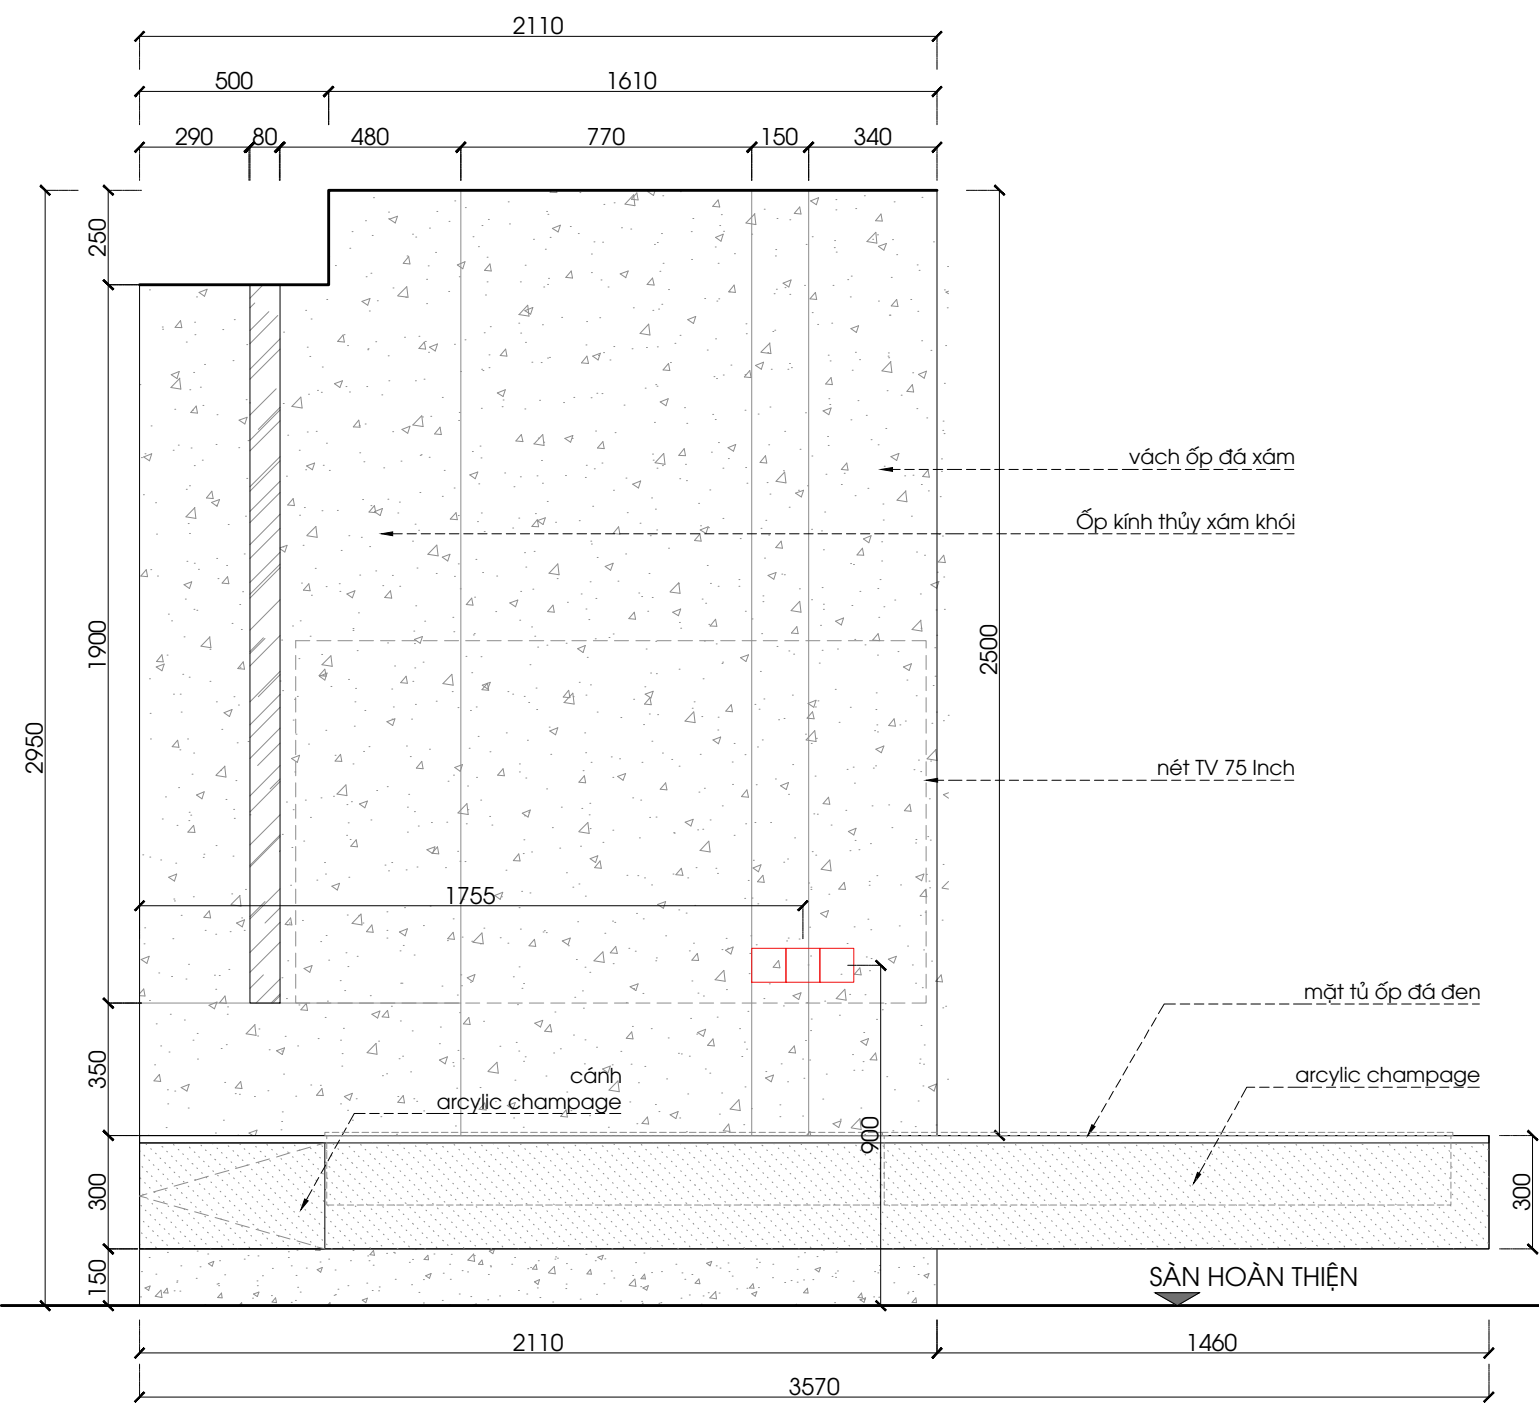


MẶT ĐỪNG 2 PK-01
1:20 @A3

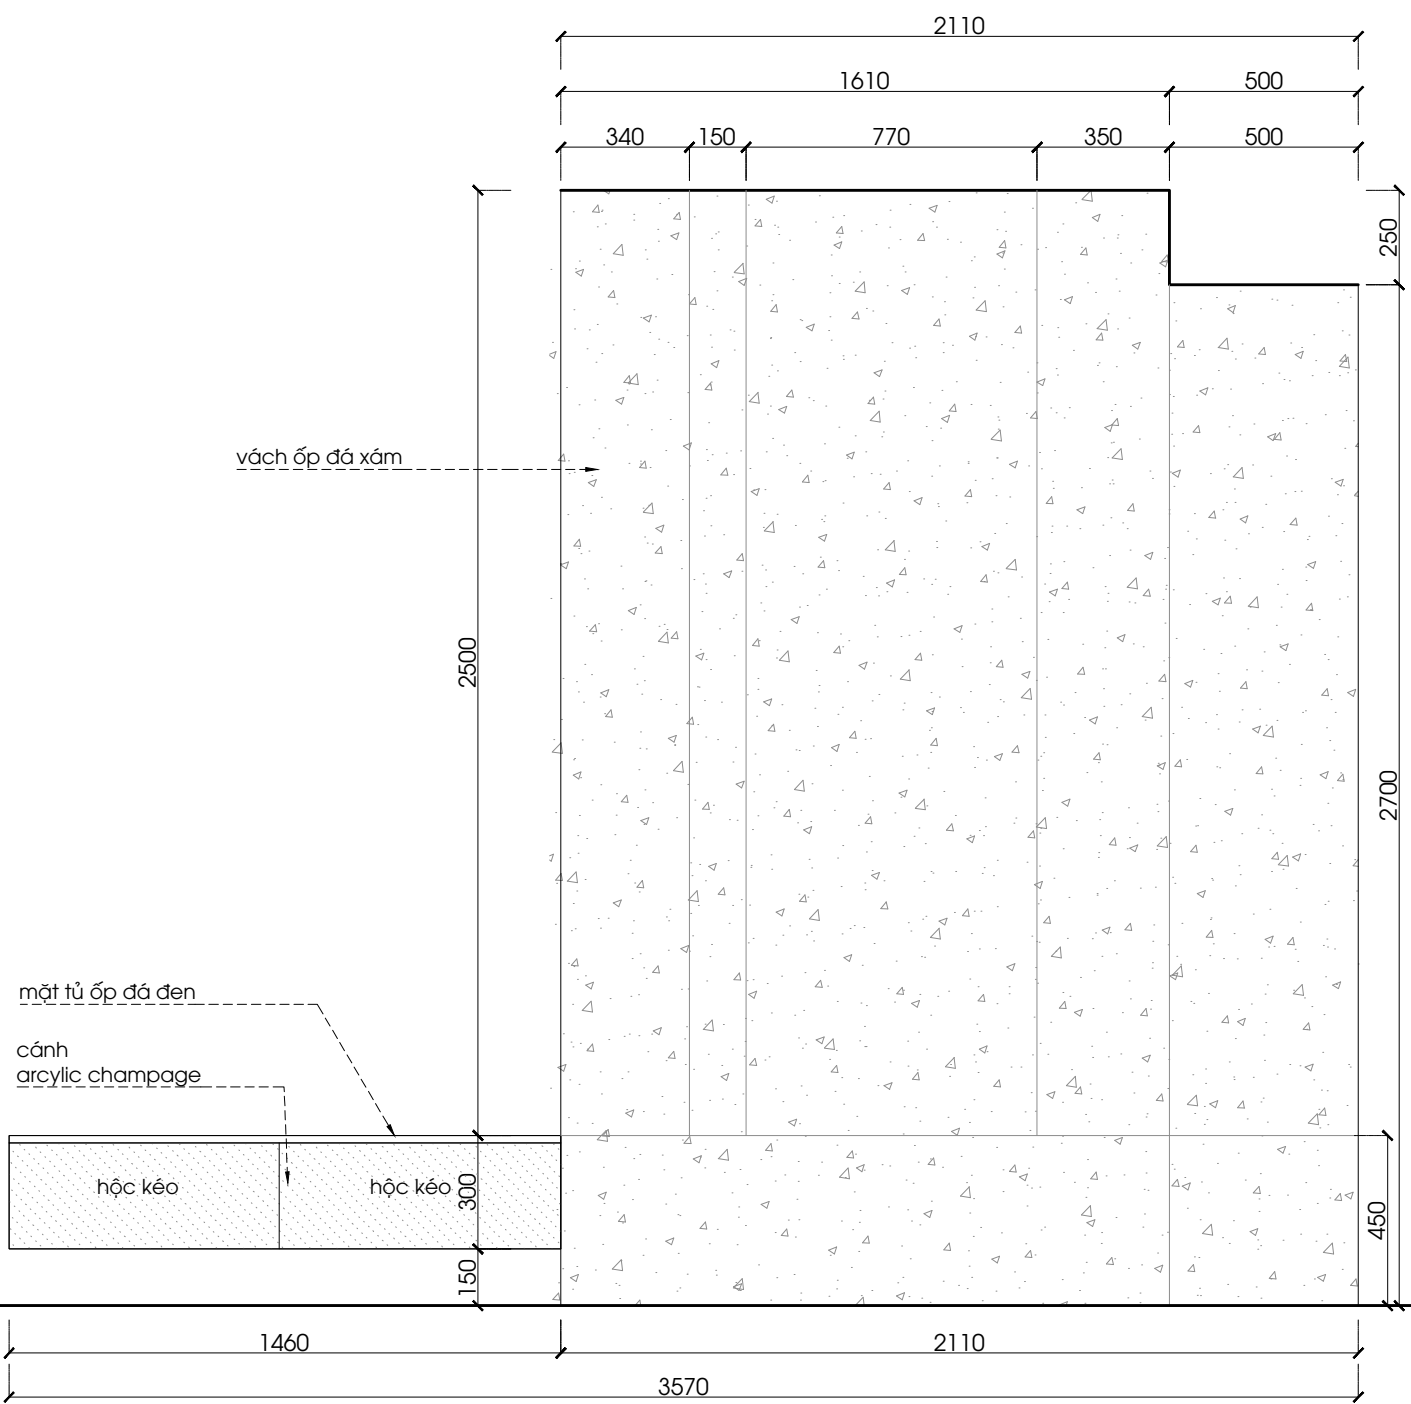



MẶT ĐỪNG 3 PK-01
1:20 @A3

PHÁT HÀNH		HIỆU CHÍNH		GHI CHÚ	ARCHITECTURAL DESIGN — THIẾT KẾ KIẾN TRÚC		DESIGNER - CHỦ TRÌ THIẾT KẾ		PROJECT TITLE - TÊN DỰ ÁN		DATE - NGÀY	
					- MỌI KÍCH THƯỚC CẦN ĐƯỢC KIỂM TRA THEO THỰC TẾ CÔNG TRƯỜNG	CÔNG TY TNHH KIẾN TRÚC VIỆT VACO DESIGN LẦU 1, 3bis PHAN VĂN ĐẠT - P. BẾN NGHÉ - Q.1 - TP. HCM TEL: +84-9-36223364 EMAIL: info@vacodesign.com	ThS.KTS. ĐỖ QUỐC HIỆP	CĂN HỘ 08.03- 08.04-08.05-08.06	03 - 2025	SCALE - TỈ LỆ 1:20		
				DIRECTOR - GIÁM ĐỐC	DRAWN BY - NGƯỜI VẼ		DRAWING TITLE - TÊN BẢN VẼ		DRAWING NO. - SỐ HIỆU BẢN VẼ	KÝ HIỆU BẢNG VẼ		
				ThS.KTS. ĐỖ QUỐC HIỆP	KTS. TRẦN TRUNG KIẾN		CHI TIẾT PK-01		NK-07	N		

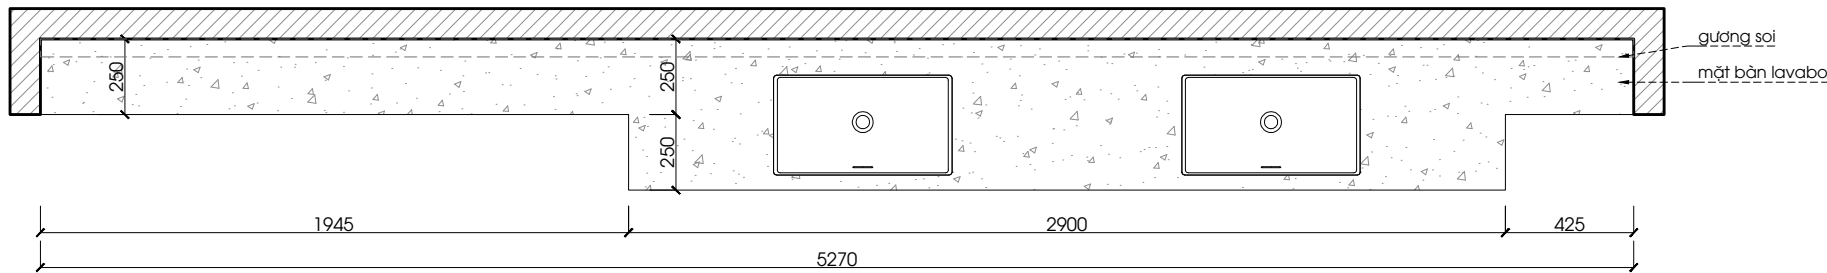


WC-01 MẶT BẰNG

1:25 @ A3

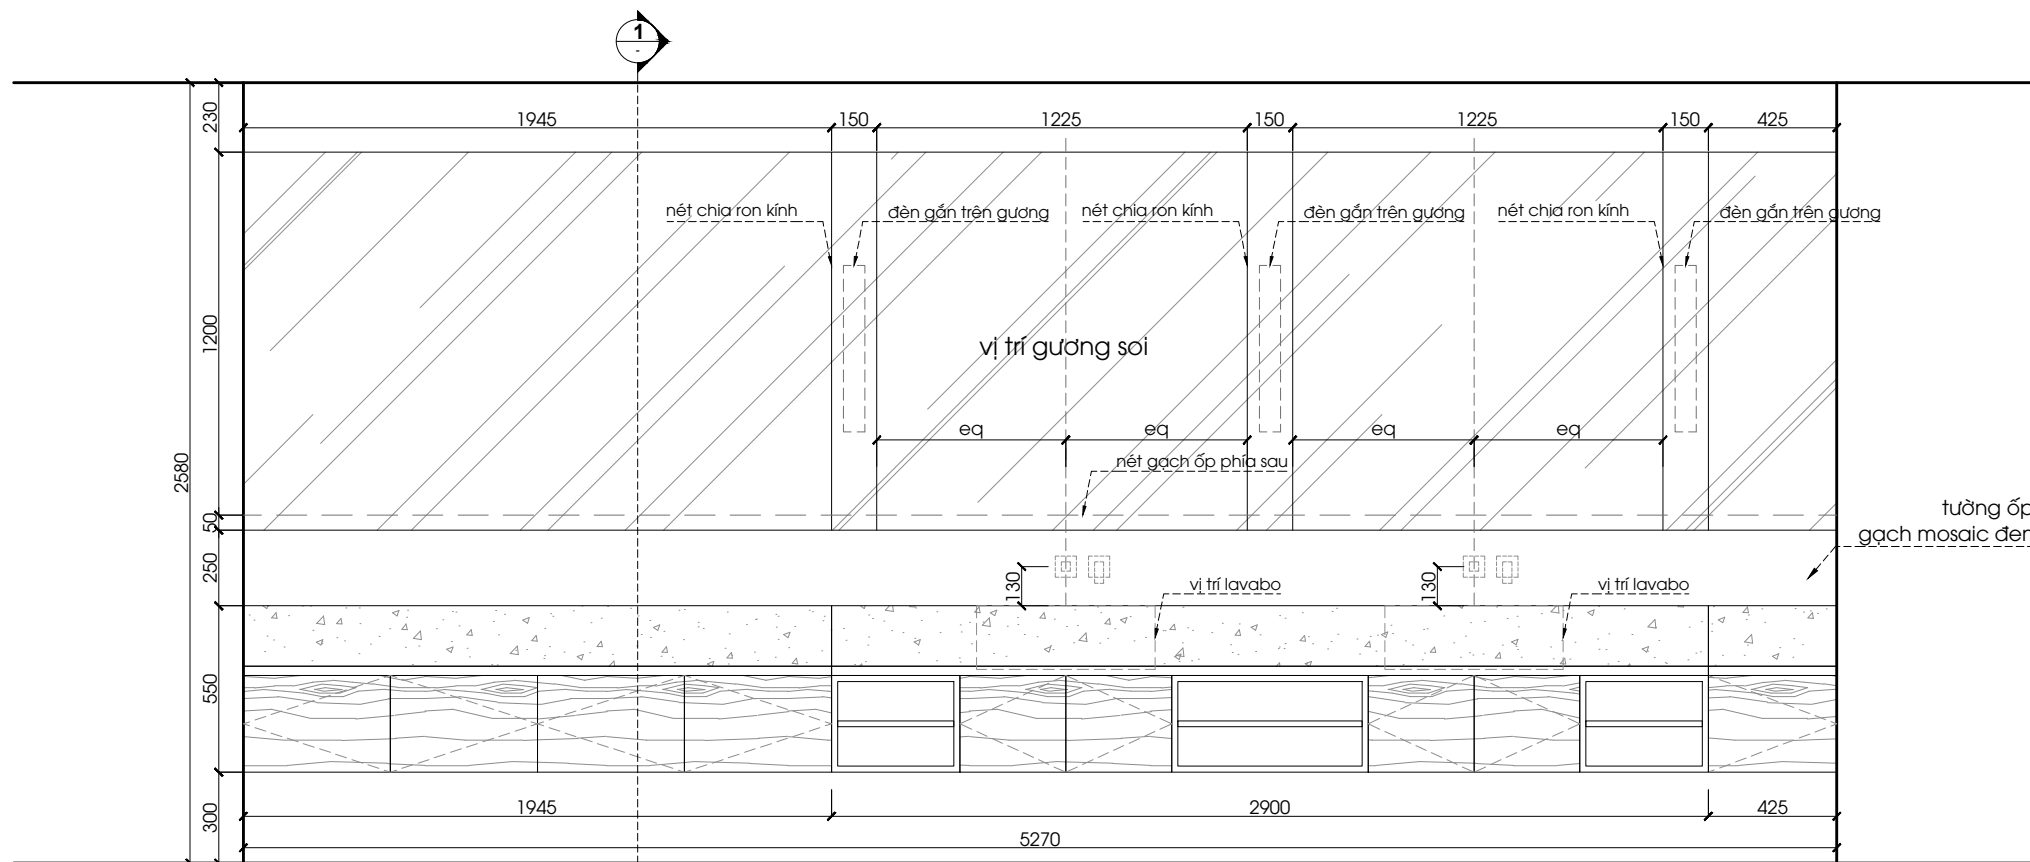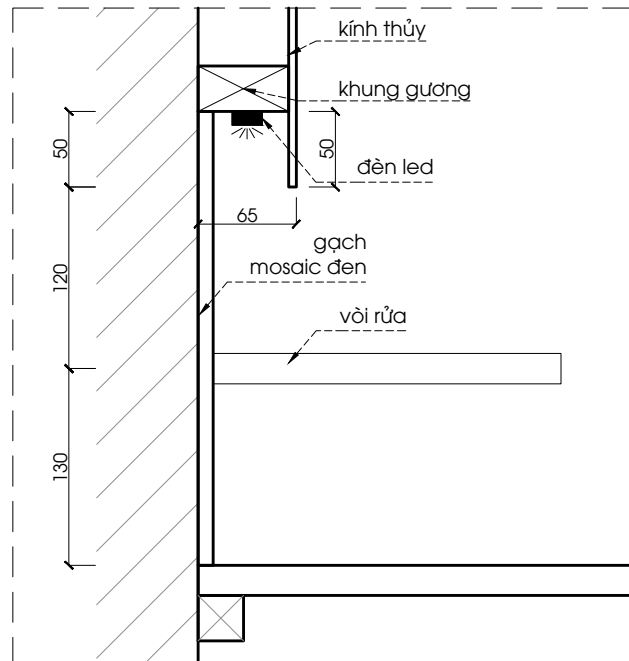

WC-01 MẶT ĐỨNG


1:25 @ A3

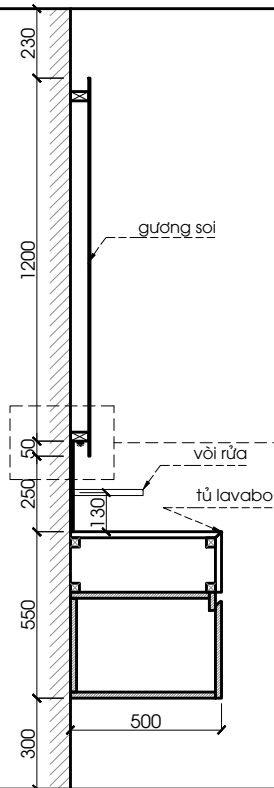

WC-01 MẶT CẮT 1


1:25 @ A3

PHÁT HÀNH		HIỆU CHỈNH		GHI CHÚ	ARCHITECTURAL DESIGN — THIẾT KẾ KIẾN TRÚC		DESIGNER - CHỦ TRÌ THIẾT KẾ		PROJECT TITLE - TÊN DỰ ÁN		DATE - NGÀY	
					- MỌI KÍCH THƯỚC CẦN ĐƯỢC KIỂM TRA THEO THỰC TẾ CÔNG TRƯỜNG	CÔNG TY TNHH KIẾN TRÚC VIỆT VACO DESIGN LẦU 1, 3bis PHAN VĂN ĐẠT - P. BẾN NGHÉ - Q.1 - TP. HCM TEL: +84-9-36223384 EMAIL: info@vacodesign.com	ThS.KTS. ĐỖ QUỐC HIỆP	CĂN HỘ 08.03- 08.04-08.05-08.06	03 - 2025	SCALE - TỈ LỆ 1:20		
				DIRECTOR - GIÁM ĐỐC	DRAWN BY - NGƯỜI VẼ	DRAWING TITLE - TÊN BẢN VẼ	DRAWING NO. - SỐ HIỆU BẢN VẼ	KÝ HIỆU BẢNG VẼ				
				ThS.KTS. ĐỖ QUỐC HIỆP	KTS. TRẦN TRUNG KIẾN	CHI TIẾT TỦ LAVABO WC CHUNG WC-01	NK-08	N				

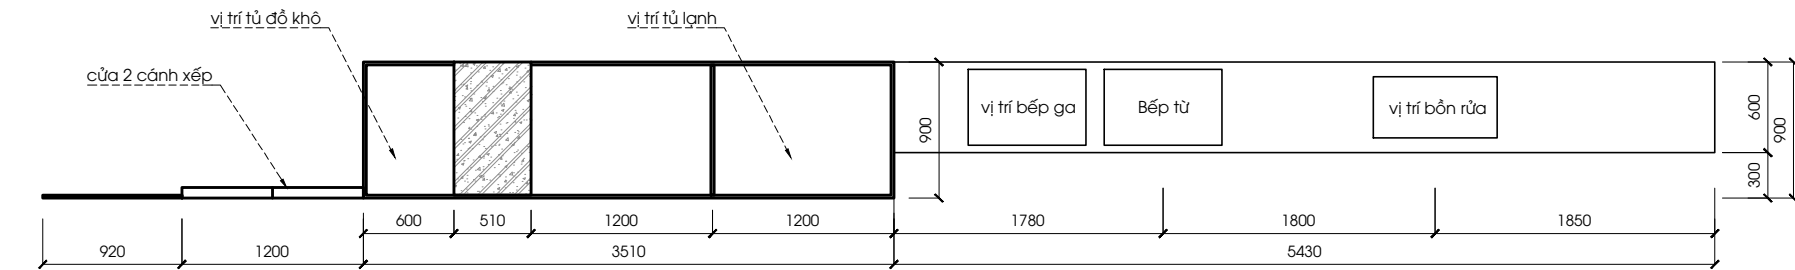

MẶT BẰNG HỆ TỦ BẾP


1:50 @ A3

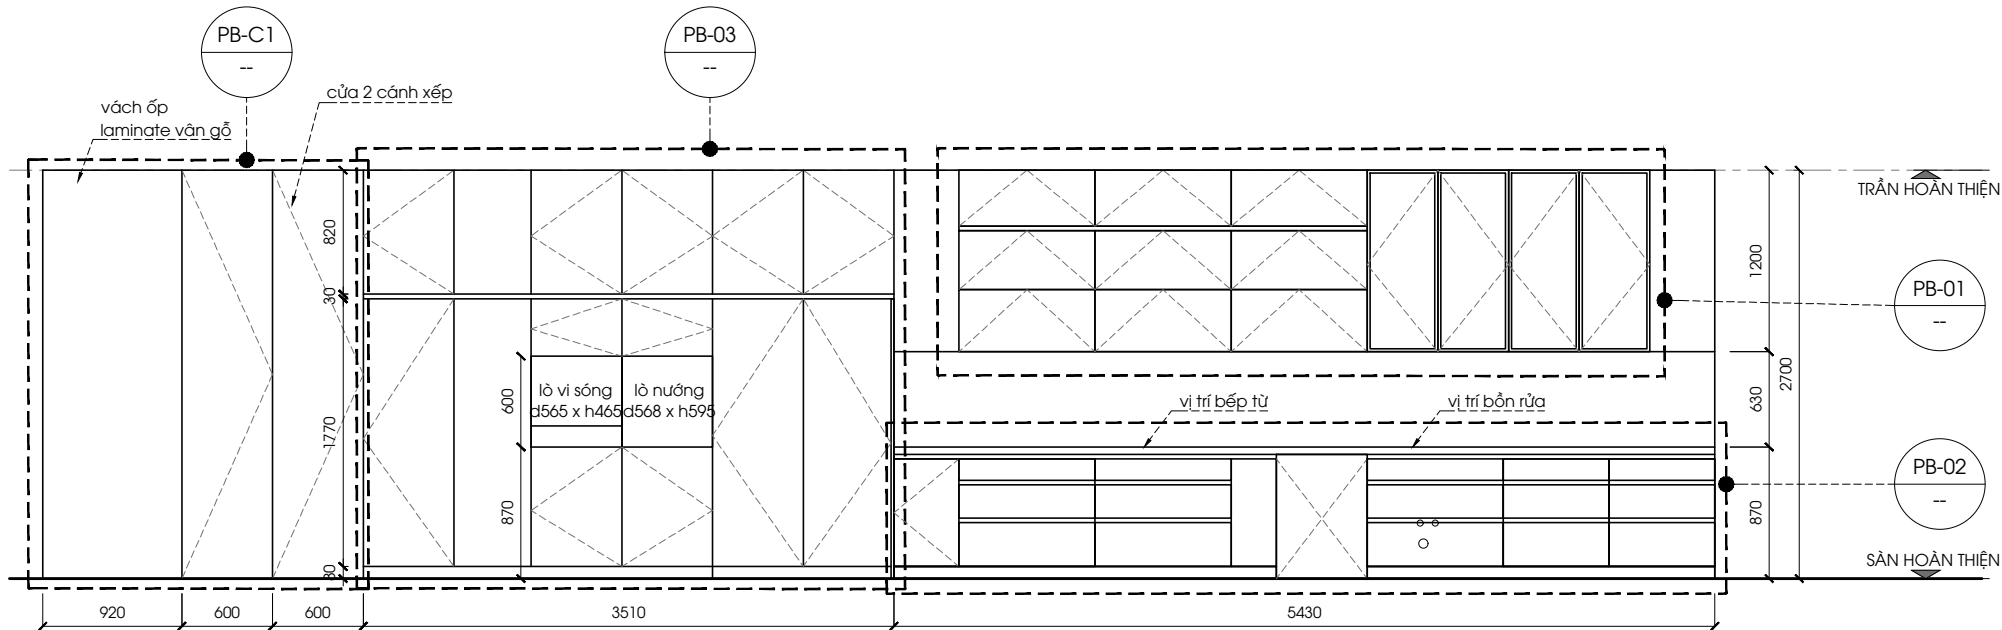


MẶT ĐỨNG HỆ TỦ BẾP

1:50 @ A3

PHÁT HÀNH		HIỆU CHÍNH		GHI CHÚ	ARCHITECTURAL DESIGN — THIẾT KẾ KIẾN TRÚC		DESIGNER - CHỦ TRÌ THIẾT KẾ		PROJECT TITLE - TÊN DỰ ÁN		DATE - NGÀY			
					- MỌI KÍCH THƯỚC CẦN ĐƯỢC KIỂM TRA THEO THỰC TẾ CÔNG TRƯỜNG	DESIGN CÔNG TY TNHH KIẾN TRÚC VIỆT VACO DESIGN LẦU 1, 38is PHAN VĂN ĐẠT - P. BẾN NGHÉ - Q.1 - TP. HCM TEL: +84-9-38223384 EMAIL: info@vacodesign.com	ThS.KTS. ĐỖ QUỐC HIỆP	CĂN HỘ 08.03- 08.04-08.05-08.06	03 - 2025	SCALE - TỈ LỆ				
										DIRECTOR - GIÁM ĐỐC	DRAWN BY - NGƯỜI VẼ	DRAWING TITLE - TÊN BẢN VẼ	DRAWING NO. - SỐ HIỆU BẢN VẼ	KÝ HIỆU BẢNG VẼ
										ThS.KTS. ĐỖ QUỐC HIỆP	KTS. TRẦN TRUNG KIẾN	CHI TIẾT HỆ TỦ BẾP	NB-01	N

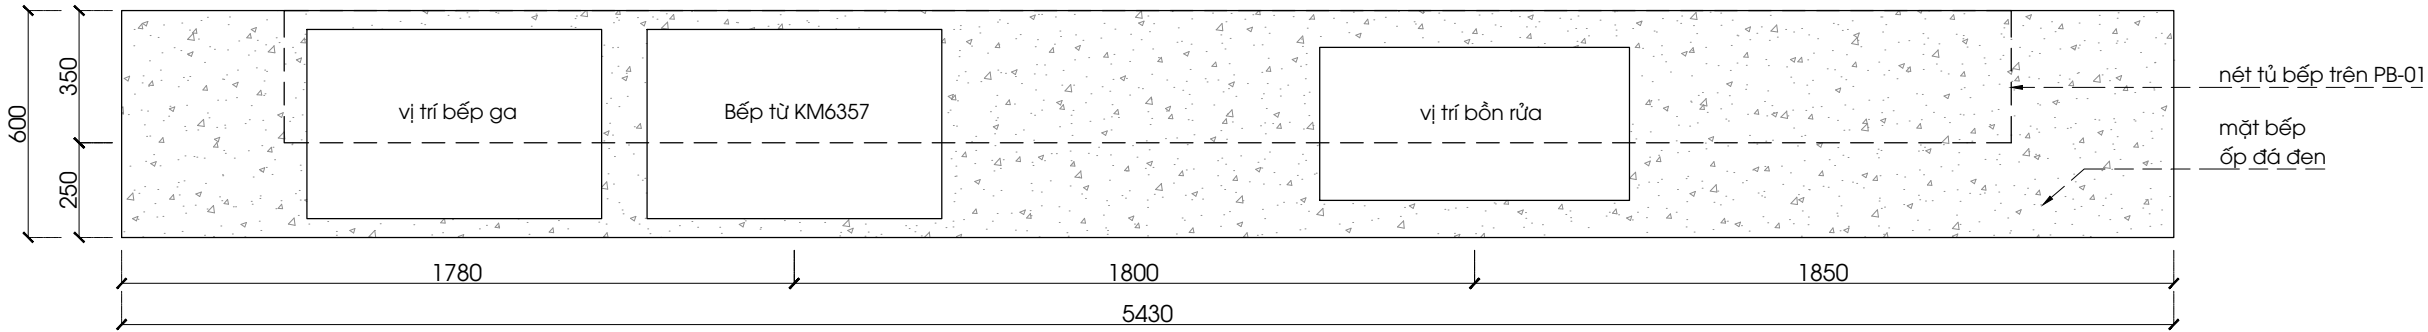


PB-02 - MẶT BẰNG
1:20 @ A3

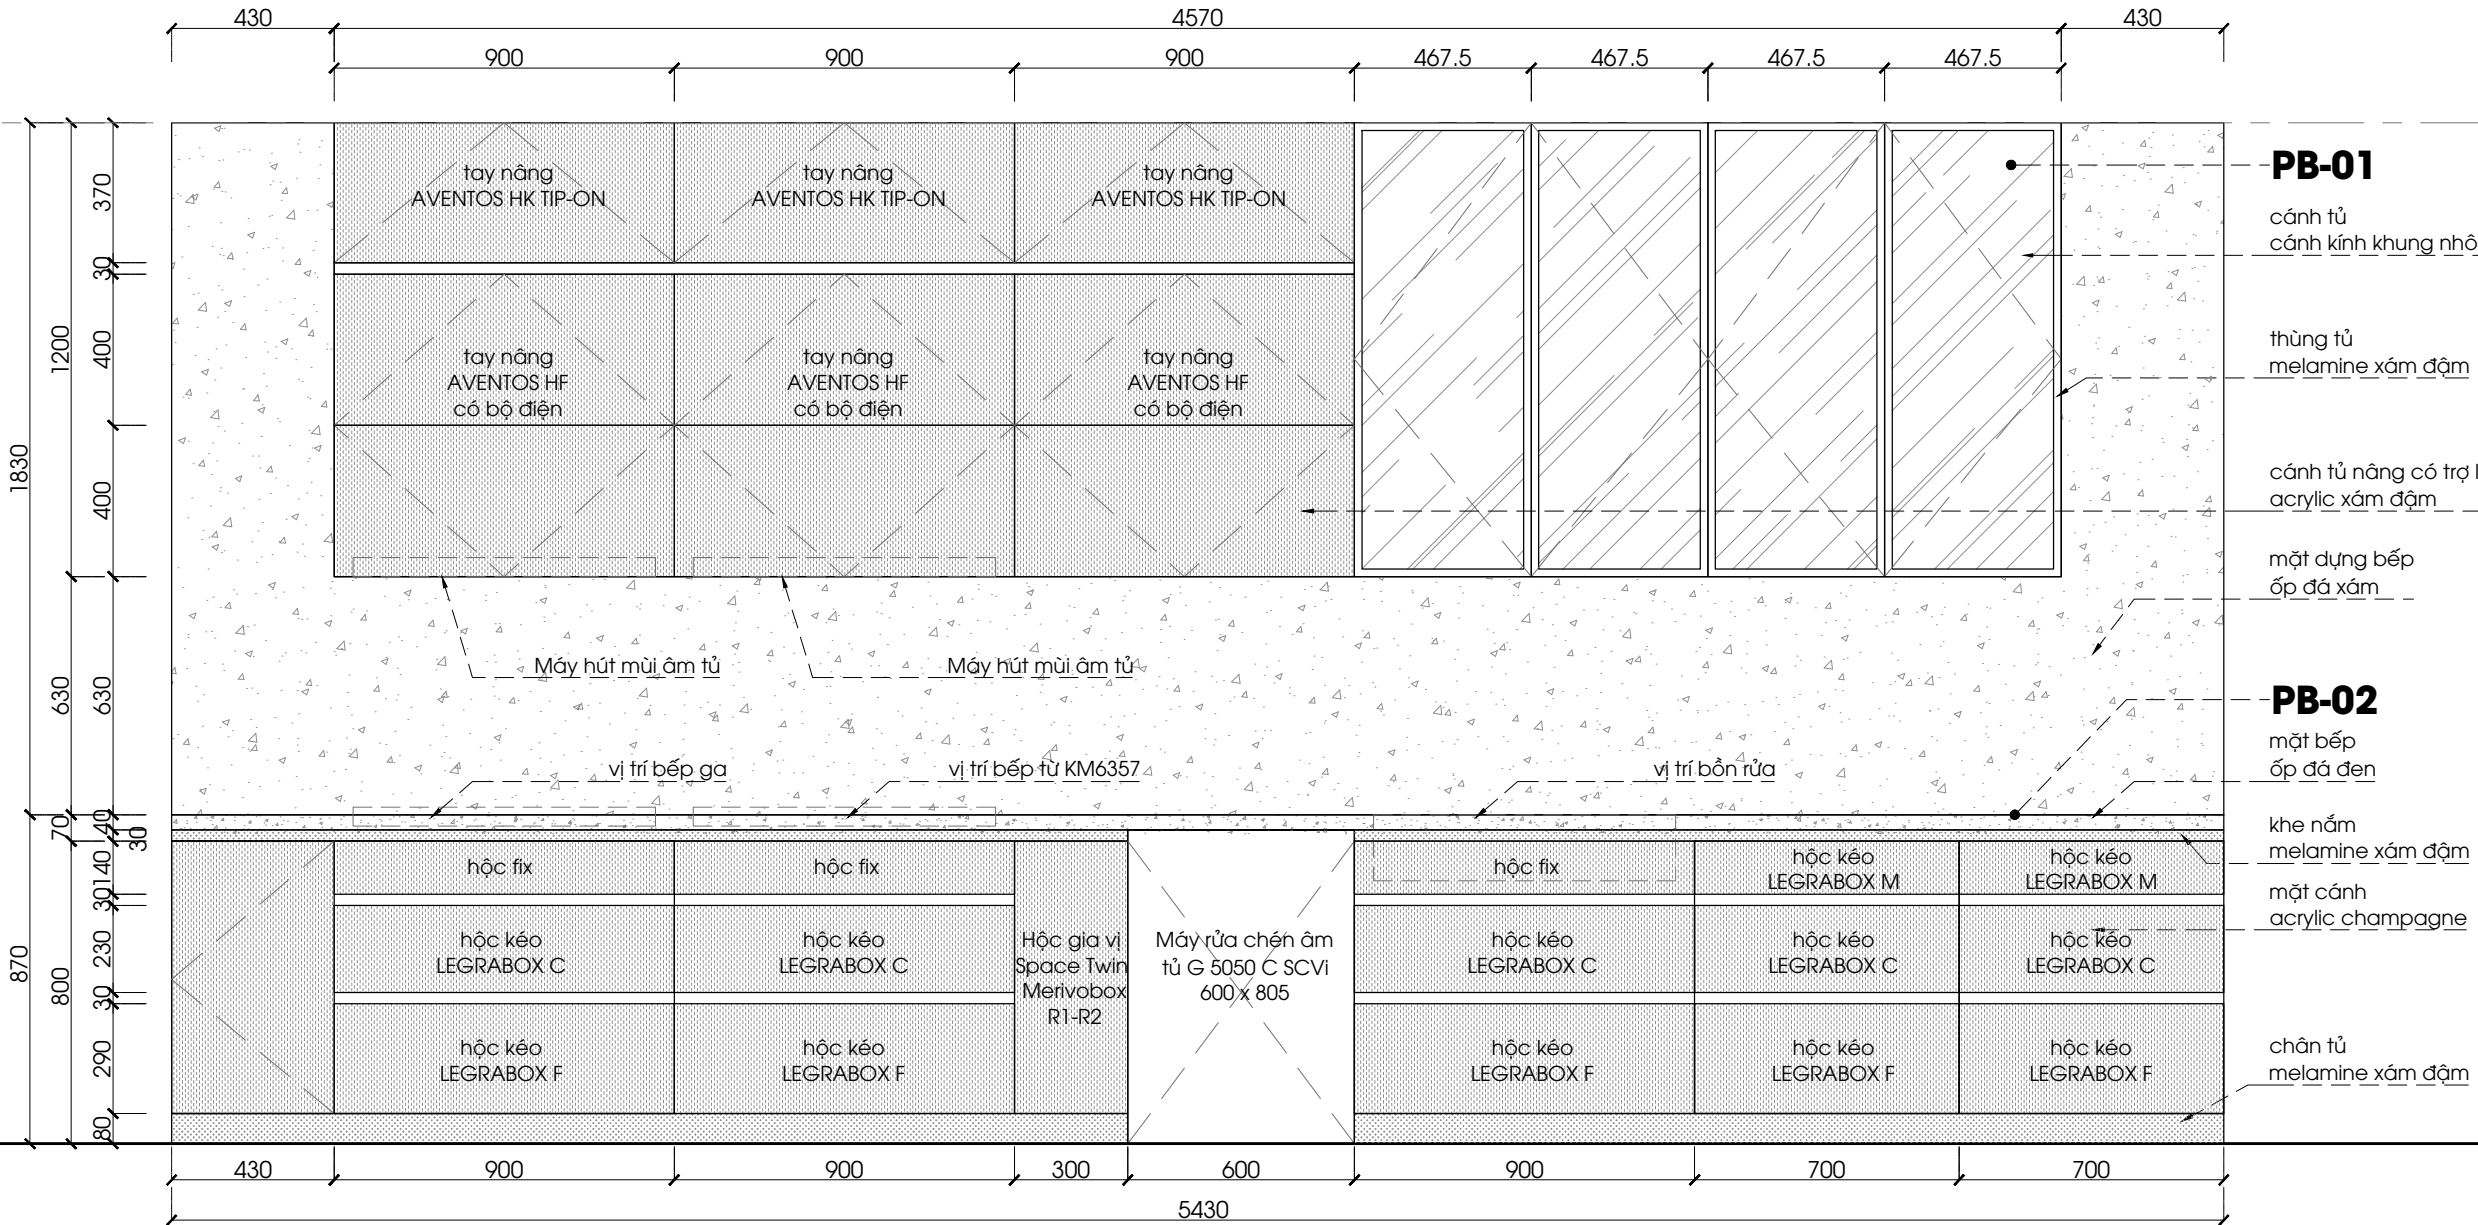

PB-01 & PB-02 - MẶT ĐỨNG
1:20 @ A3


PHÁT HÀNH		HIỆU CHÍNH		GHI CHÚ	ARCHITECTURAL DESIGN — THIẾT KẾ KIẾN TRÚC  CÔNG TY TNHH KIẾN TRÚC VIỆT VACO DESIGN LẦU 1, 38b PHAN VĂN ĐẠT - P. BẾN NGHÉ - Q.1 - TP. HCM TEL: +84-9-36223384 EMAIL: info@vacodesign.com	DESIGNER - CHỦ TRÌ THIẾT KẾ	PROJECT TITLE - TÊN DỰ ÁN	DATE - NGÀY		
								03 - 2025		
								SCALE - TỈ LỆ		
								1:20		
								DRAWING TITLE - TÊN BẢN VẼ	DRAWING NO. - SỐ HIỆU BẢN VẼ	KÝ HIỆU BẢNG VẼ
				DIRECTOR - GIÁM ĐỐC	DRAWN BY - NGƯỜI VẼ	CHI TIẾT TỦ BẾP PB-01	NB-02	N		
				ThS.KTS. ĐỖ QUỐC HIỆP	KTS. TRẦN TRUNG KIẾN	CHI TIẾT QUẦY BẾP PB-02				

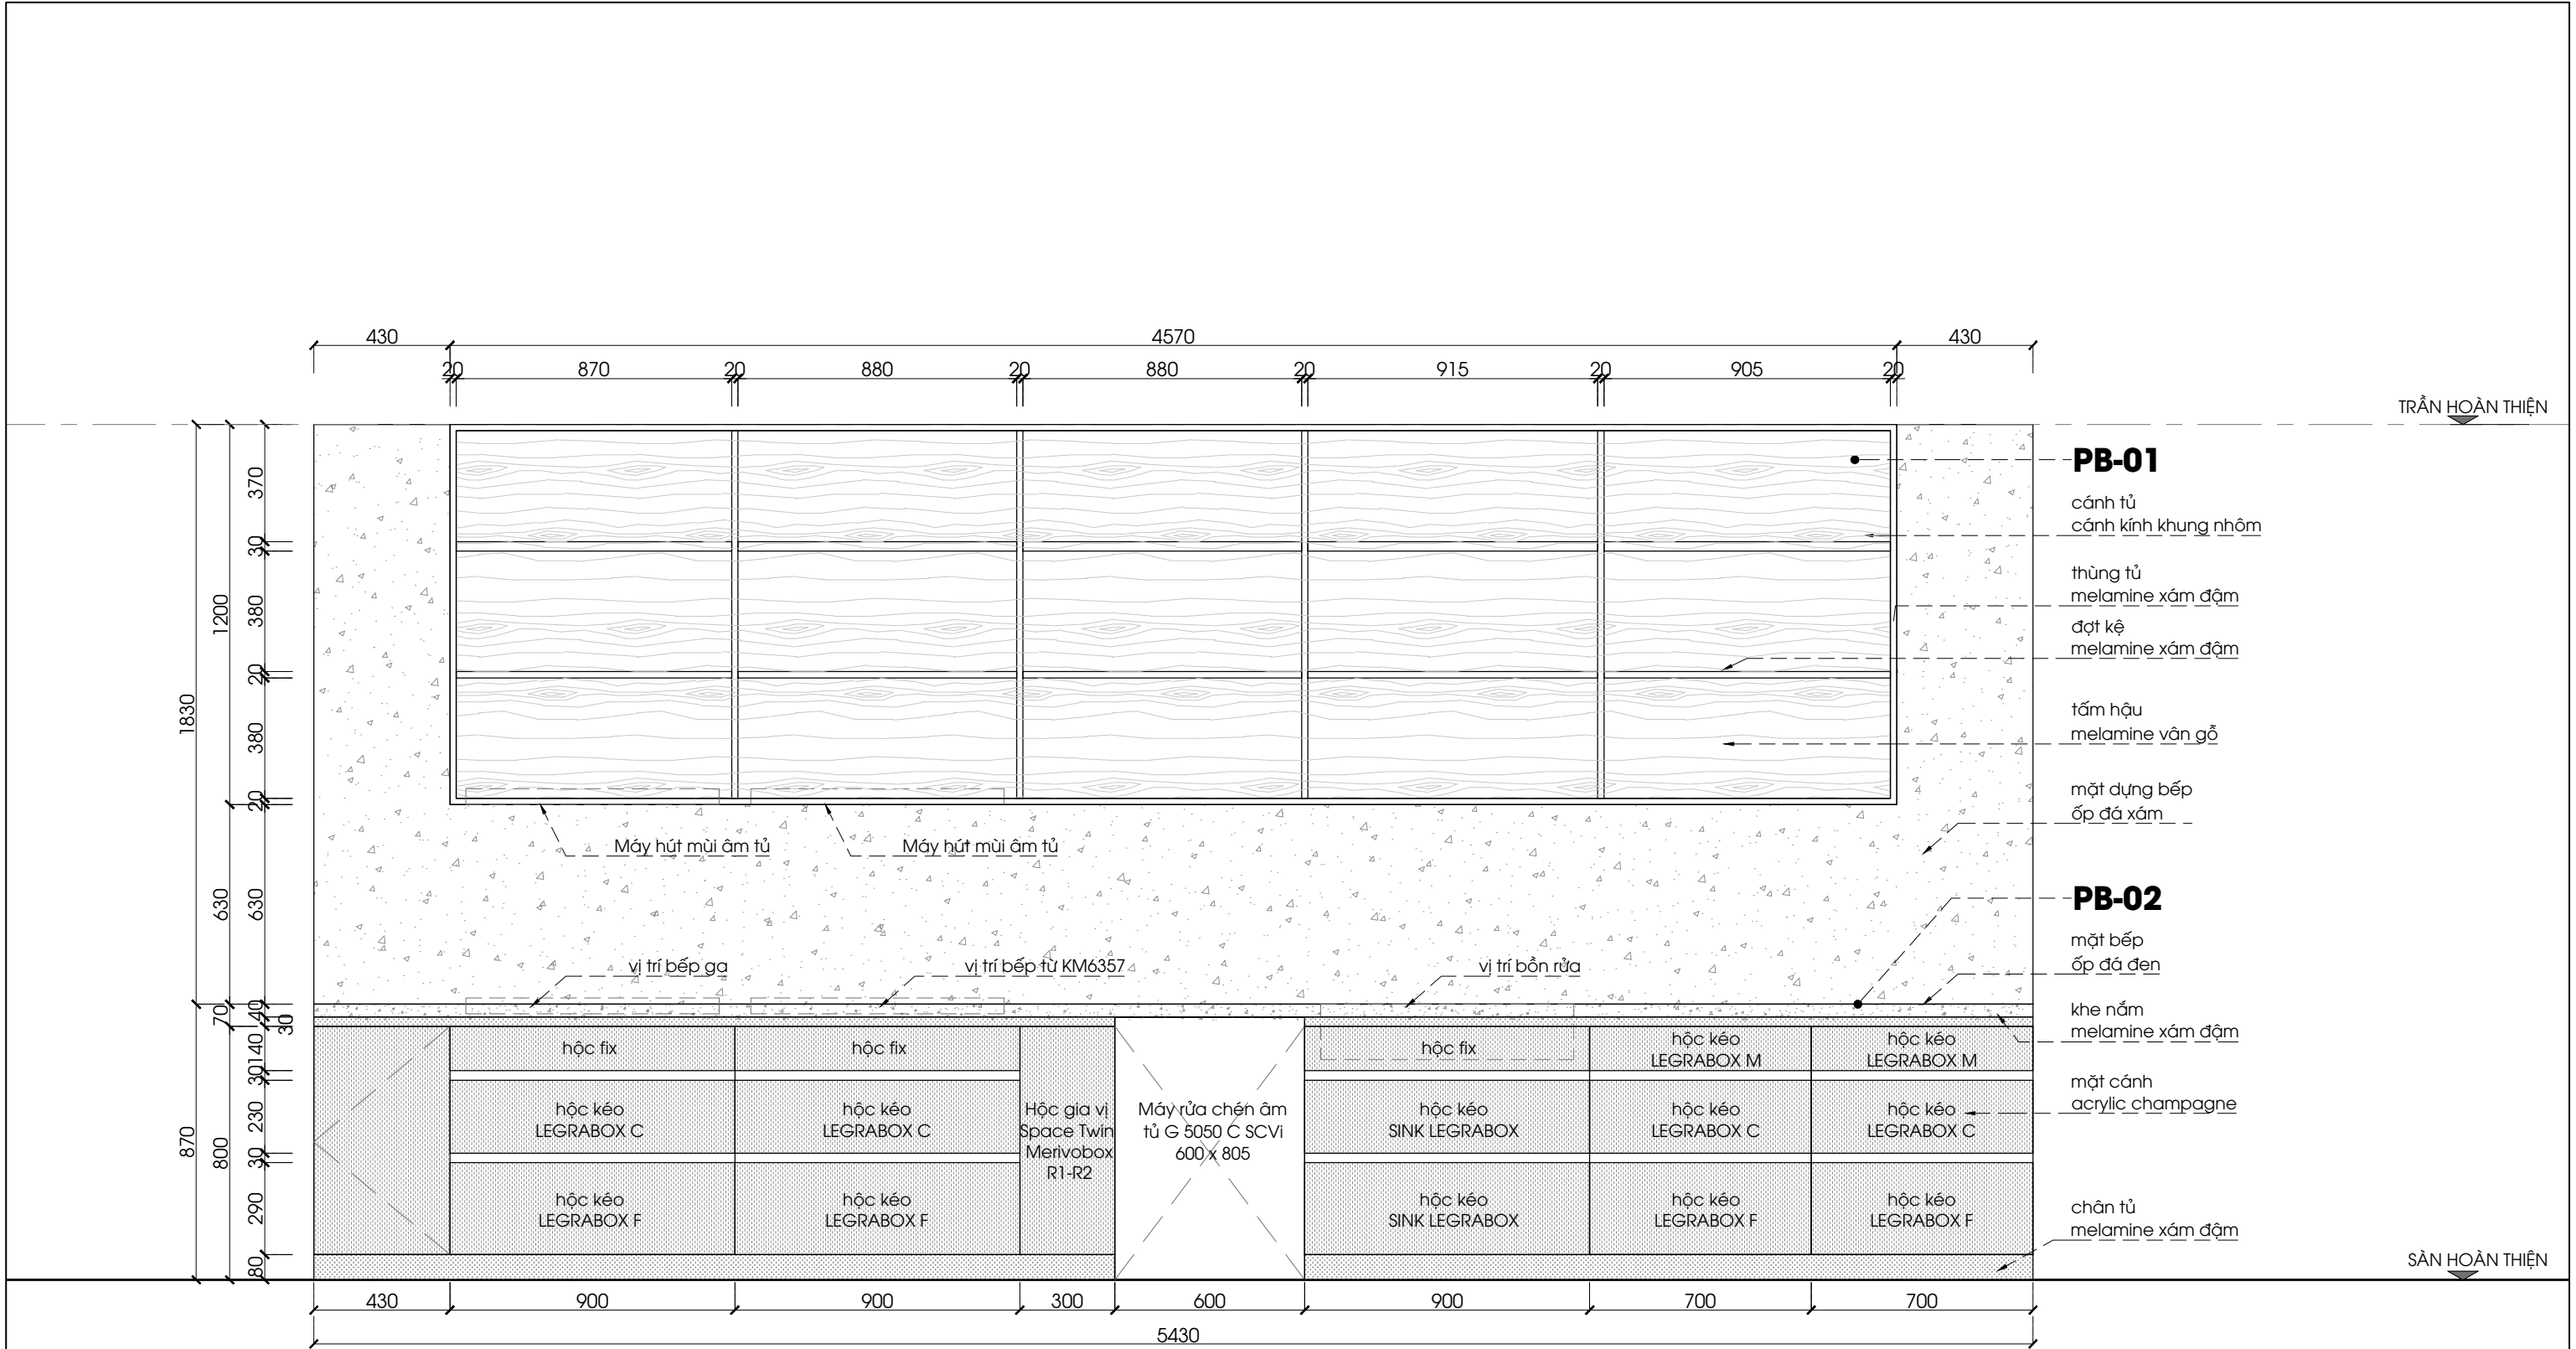


PB-01 & PB-02 - MẶT ĐỪNG - KHÔNG CẢNH

1:20 @ A3

PHÁT HÀNH		HIỆU CHỈNH		GHI CHÚ	ARCHITECTURAL DESIGN — THIẾT KẾ KIẾN TRÚC		DESIGNER - CHỦ TRÌ THIẾT KẾ	PROJECT TITLE - TÊN DỰ ÁN	DATE - NGÀY	
					CÔNG TY TNHH KIẾN TRÚC VIỆT VACO DESIGN LẦU 1, 38b PHAN VĂN ĐẠT - P. BẾN NGHÉ - Q.1 - TP. HCM TEL: +84-9-36233584 EMAIL: info@vacodesign.com				03 - 2025	
							ThS.KTS. ĐỖ QUỐC HIỆP	CĂN HỘ 08.03- 08.04-08.05-08.06	SCALE - TỈ LỆ	
									1:20	
									DRAWING NO. - SỐ HIỆU BẢN VẼ	KÝ HIỆU BẢNG VẼ
									NB-03	N
				- MỌI KÍCH THƯỚC CẦN ĐƯỢC KIỂM TRA THEO THỰC TẾ CÔNG TRƯỜNG	ThS.KTS. ĐỖ QUỐC HIỆP	DIRECTOR - GIÁM ĐỐC	KTS. TRẦN TRUNG KIẾN	CHI TIẾT TỦ BẾP PB-01	CHI TIẾT QUẦY BẾP PB-02	

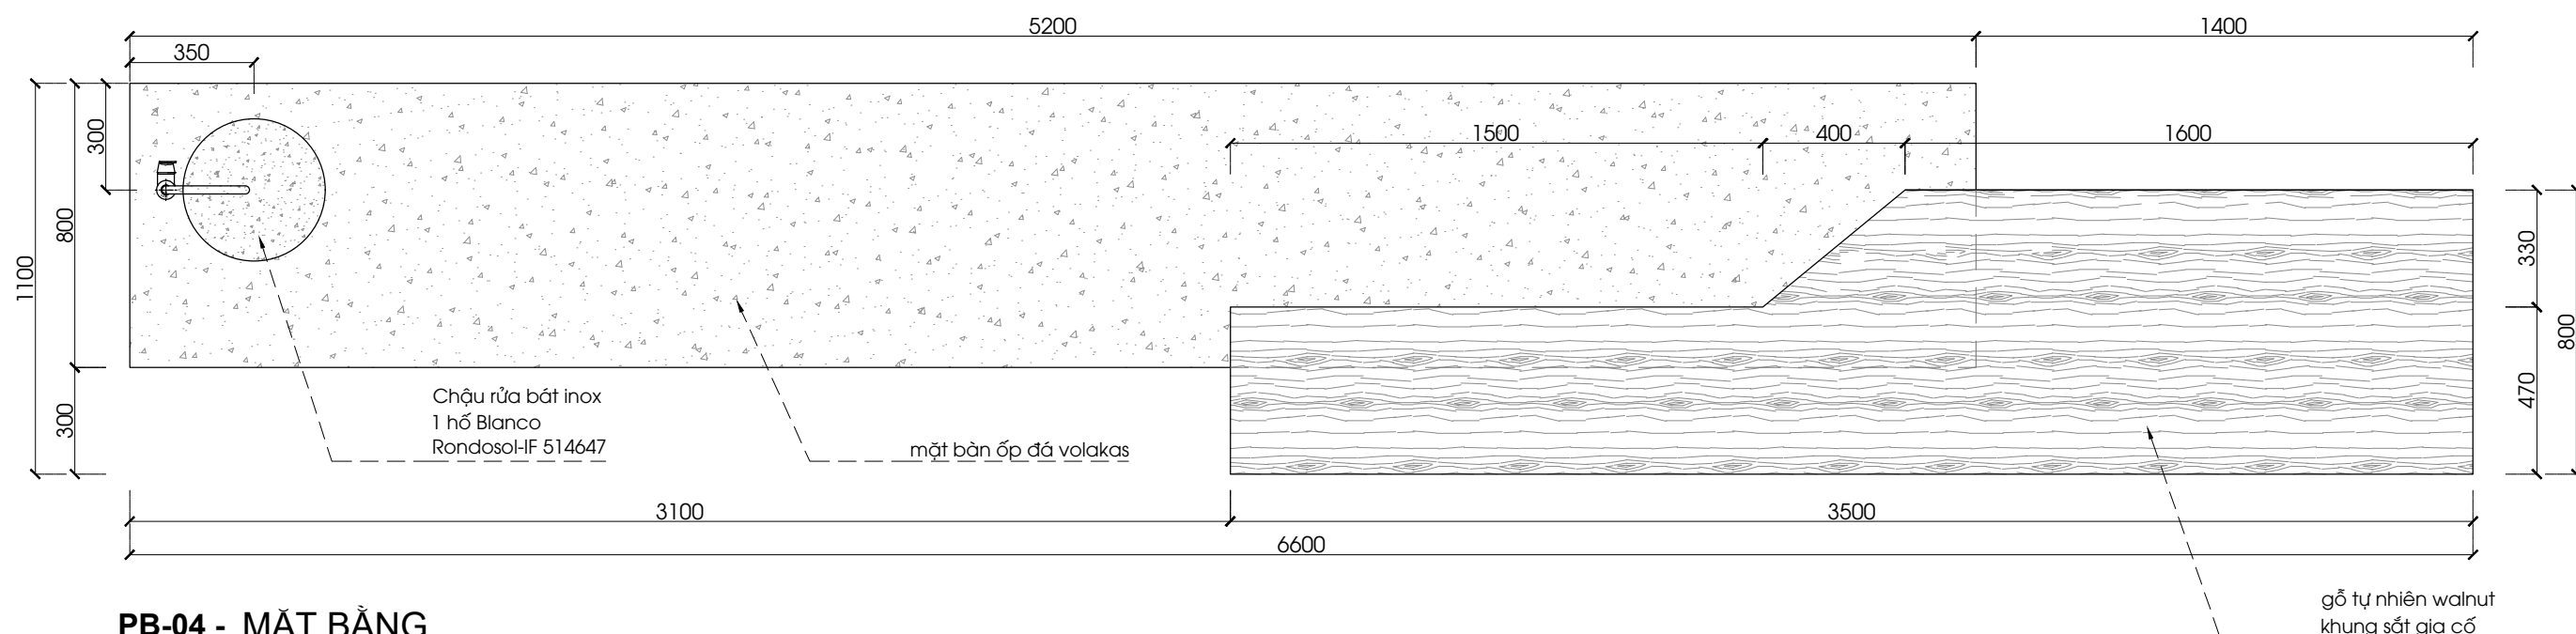

1:20 @ A3

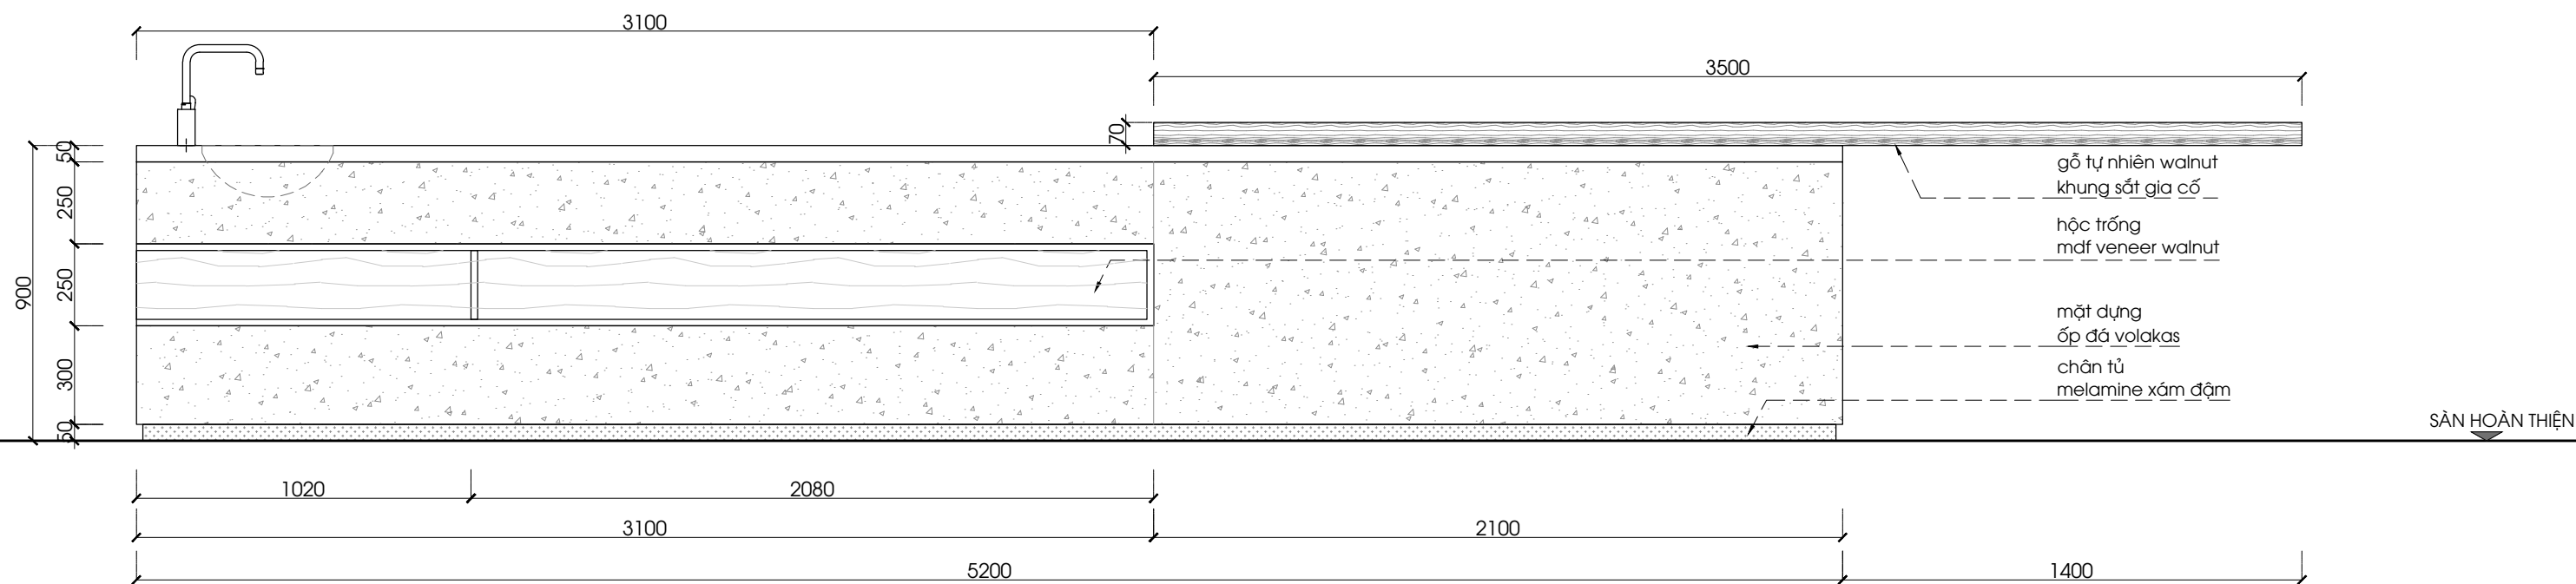

1:20 @ A3

PHÁT HÀNH		HIỆU CHỈNH		GHI CHÚ	ARCHITECTURAL DESIGN — THIẾT KẾ KIẾN TRÚC CÔNG TY TNHH KIẾN TRÚC VIỆT VACO DESIGN LẦU 1, 3b/1a PHAN VĂN DAT - P. BẾN NGHÉ - Q.1 - TP. HCM TEL: +84-9-38223384 EMAIL: info@vacodesign.com DESIGN DIRECTOR - GIÁM ĐỐC ThS.KTS. ĐỖ QUỐC HIỆP	DESIGNER - CHỦ TRÌ THIẾT KẾ		PROJECT TITLE - TÊN DỰ ÁN		DATE - NGÀY	
						CĂN HỘ 08.03- 08.04-08.05-08.06	SCALE - TỈ LỆ	03 - 2025			
								1:20			
						ThS.KTS. ĐỖ QUỐC HIỆP	DRAWING TITLE - TÊN BẢN VẼ	DRAWING NO. - SỐ HIỆU BẢN VẼ	KÝ HIỆU BẢNG VẼ		
						KTS. TRẦN TRUNG KIÊN	CHI TIẾT NỘI THẤT	NB-05	N		
					CHI TIẾT ĐẢO BẾP PB-04						


The drawing shows a kitchen island with a front elevation on the left and a side elevation on the right. The front elevation has a total width of 1100mm and a total height of 900mm. It features a 300mm wide top section with a 30mm gap, a 1300mm high central section, a 250mm high middle section, and a 300mm high base section. The side elevation shows a total width of 800mm and a total height of 900mm. It includes three drawers (hộc kéo) with heights of 220mm, 250mm, and 230mm. The island is supported by four legs (chân tủ) with a height of 300mm. The materials specified are natural walnut wood (gỗ tự nhiên walnut), melamine laminate (melamine xám đậm), and acrylic champagne (acrylic champagne). The top surface is made of melamine laminate (mặt bàn ốp đá volakas).

Front Elevation (Left):

- Top section: 300mm wide, 30mm gap, 800mm wide.
- Central section: 1300mm high.
- Middle section: 250mm high.
- Base section: 300mm high.
- Legs (chân tủ): 300mm high.
- Materials: gỗ tự nhiên walnut, khung sắt gia cố, mặt dựng ốp đá volakas, thùng tủ melamine xám đậm, chân tủ melamine xám đậm.

Side Elevation (Right):


- Top section: 30mm gap, 800mm wide.
- Drawers (hộc kéo): 220mm, 250mm, and 230mm high.
- Legs (chân tủ): 300mm high.
- Materials: mặt bàn ốp đá volakas, gỗ tự nhiên walnut, khung sắt gia cố, tấm hậu mặt veneer walnut, thùng tủ melamine xám đậm, chân tủ melamine xám đậm.

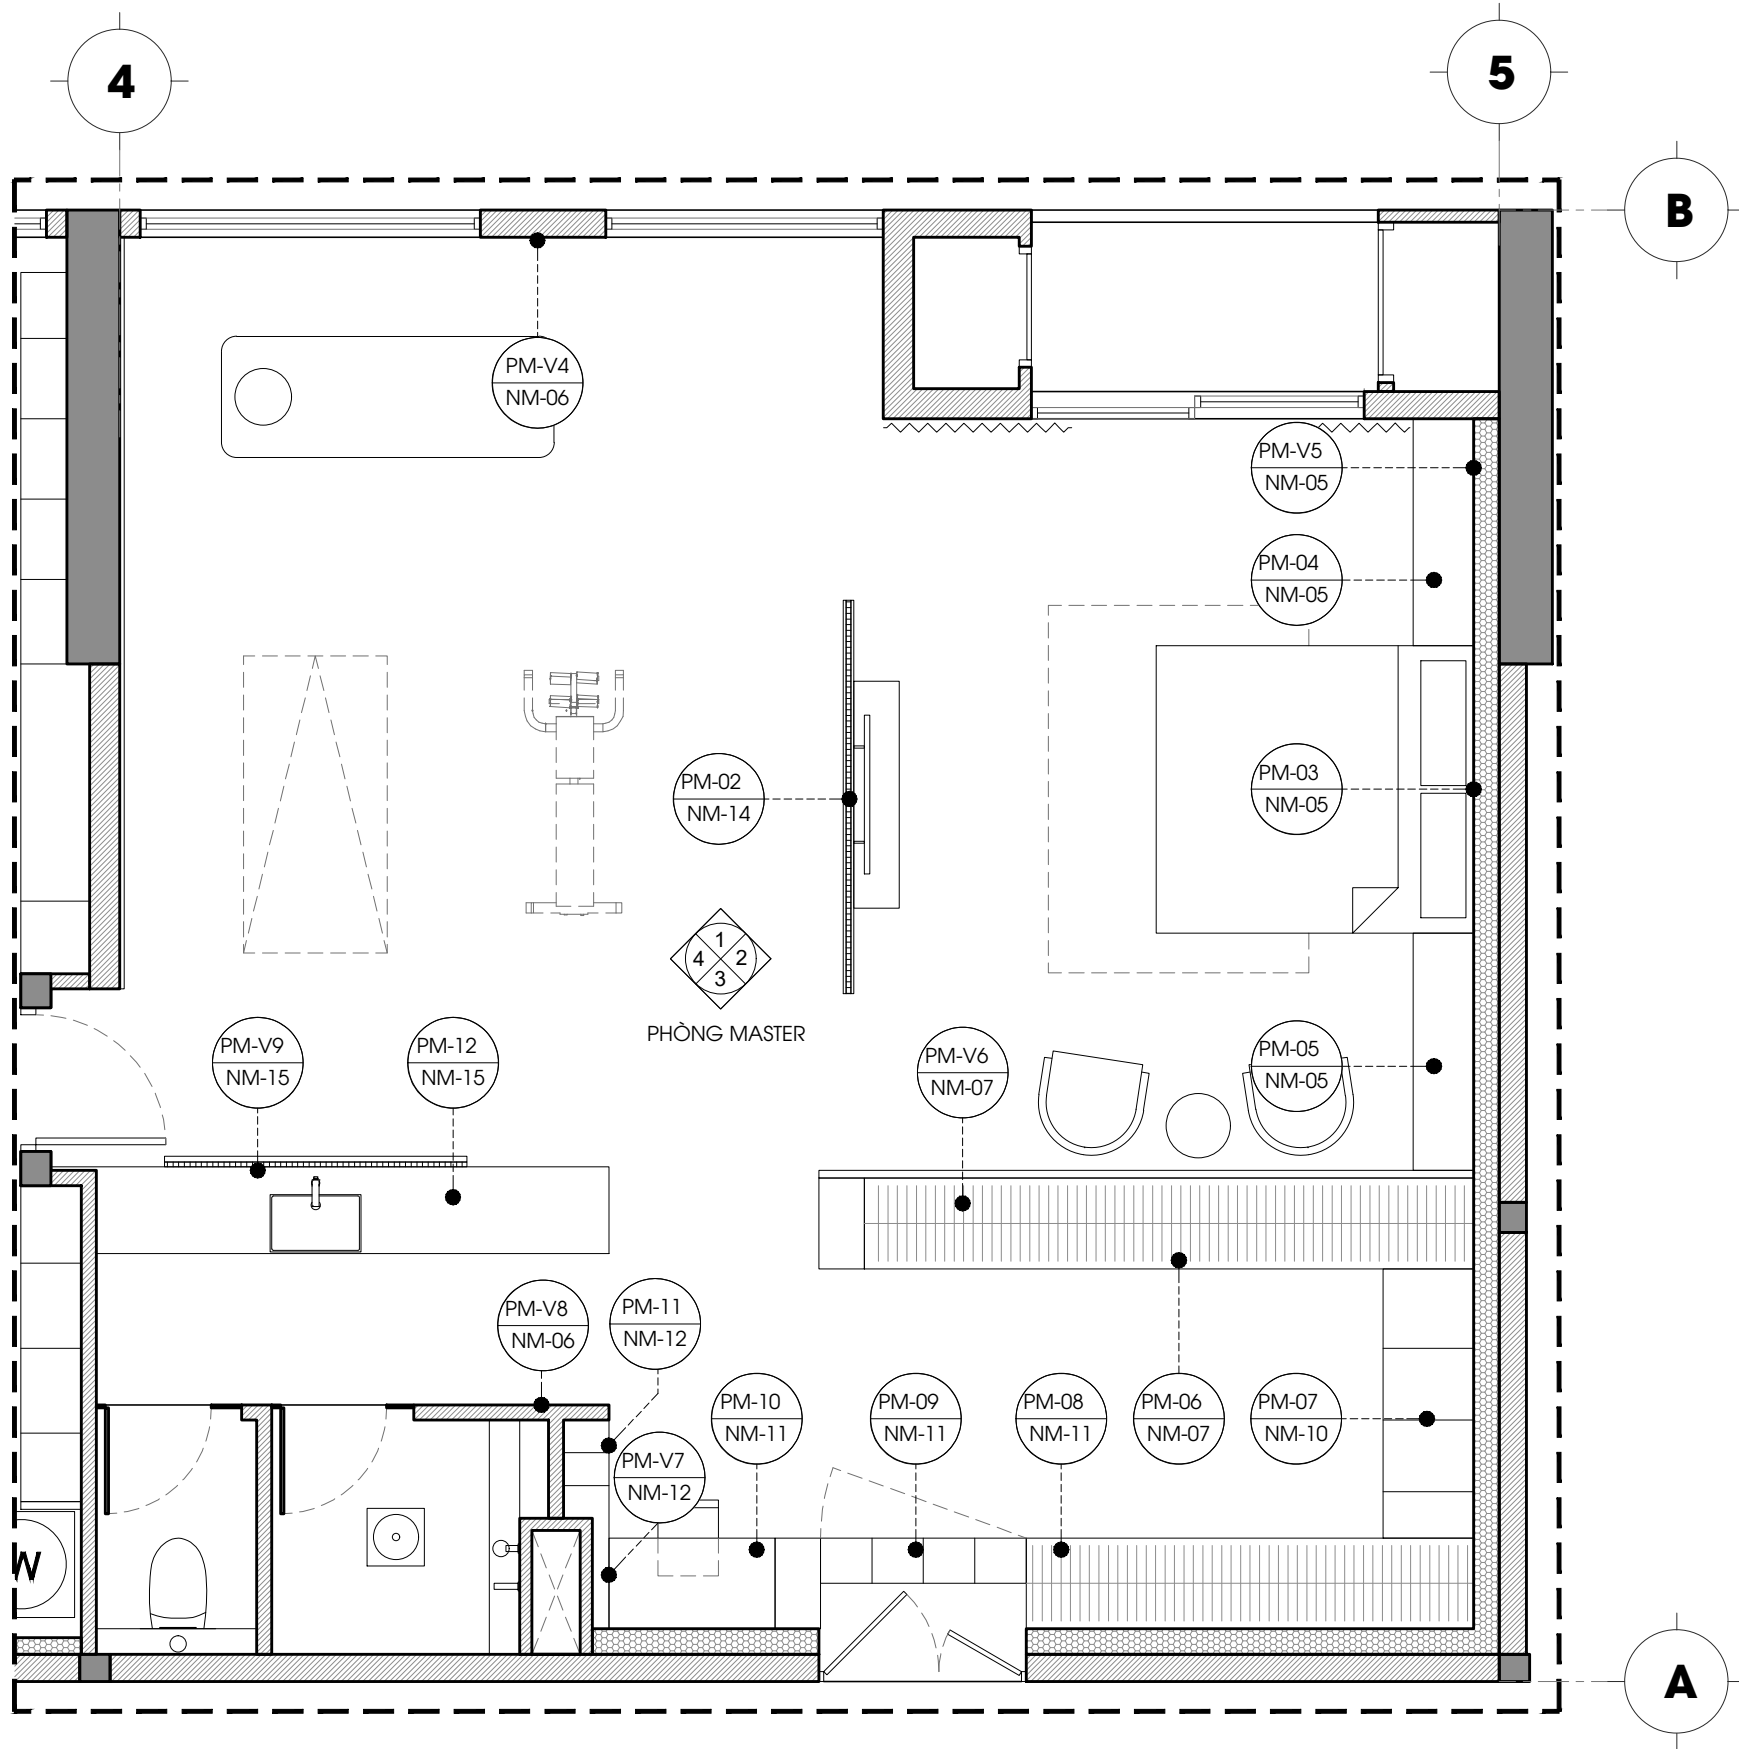



- PM-01** - TỦ TRANG TRÍ
- KHUNG THÉP ỚP GỖ TỰ NHIÊN
- PM-02** - VÁCH TIVI
- KHUNG SẮT GIA CỐ
- KÍNH THỦY, VÁCH MDF SƠN XĂM
- PM-03** - VÁCH ĐẦU GIƯỜNG
- KHUNG MELAMINE XĂM ĐẬM, BỌC NỈ
- ĐÈN LED HẮT
- PM-04** - TÁP ĐẦU GIƯỜNG
- THÙNG MELAMINE XĂM
- PM-05** - CÁCH LAMINATE XĂM
- MẶT TRÊN ĐÁ XĂM
- PM-06** - HỆ TỦ ÁO&TÚI XÁCH
- THÙNG MELAMINE XĂM ĐẬM
- ĐÓT NHÔM KÍNH
- HẬU LAMINATE VÂN ĐÁ, ĐÈN LED HẮT
- VÁCH ỚP LAMINATE VÂN VẢI
- PM-07** - TỦ TRANG TRÍ
- THÙNG MELAMINE XĂM ĐẬM
- CÁCH LAMINATE
- HẬU LAMINATE VÂN ĐÁ
- PM-08** - TỦ QUẦN ÁO
- THÙNG MELAMINE XĂM ĐẬM
- CÁCH CÁCH NHÔM KÍNH,
- HẬU LAMINATE VÂN ĐÁ
- PM-09** - TỦ TRANG TRÍ 1
- CÁCH LAMINATE VÂN GỖ
- TỦ TRANG TRÍ 2
- THÙNG MELAMINE XĂM ĐẬM
- CÁCH LAMINATE
- HẬU LAMINATE VÂN ĐÁ
- PM-V4** - VÁCH ỚP
- LAMINATE VÂN GỖ
- PM-V5** - VÁCH ỚP
- LAMINATE VÂN GỖ
- PM-V6** - VÁCH ỚP
- LAMINATE VÂN GỖ
- PM-V7** - VÁCH ỚP
- LAMINATE VÂN GỖ
- PM-V8** - VÁCH ỚP
- LAMINATE VÂN GỖ
- PM-V9** - VÁCH ỚP
- LAM MDF SƠN XĂM
- KHUN SẮT: LAVABO+VÁCH LAM

PM MẶT BẰNG BỐ TRÍ NỘI THẤT PHÒNG MASTER
1:50 @ A3


PHÁT HÀNH		HIỆU CHÍNH		GHI CHÚ	ARCHITECTURAL DESIGN — THIẾT KẾ KIẾN TRÚC		DESIGNER - CHỦ TRÌ THIẾT KẾ	PROJECT TITLE - TÊN DỰ ÁN	DATE - NGÀY				
					- MỌI KÍCH THƯỚC CẦN ĐƯỢC KIỂM TRA THEO THỰC TẾ CÔNG TRƯỜNG	CÔNG TY TNHH KIẾN TRÚC VIỆT VACO DESIGN LẦU 1, 3bis PHAN VĂN ĐẠT - P. BẾN NGHÉ - Q.1 - TP. HCM TEL: +84-9-36233584 EMAIL: info@vacodesign.com	ThS.KTS. ĐỖ QUỐC HIỆP	CĂN HỘ 08.03- 08.04-08.05-08.06	03 - 2025				
									SCALE - TỈ LỆ				
									1:50				
									DIRECTOR - GIÁM ĐỐC	DRAWN BY - NGƯỜI VẼ	DRAWING TITLE - TÊN BẢN VẼ	DRAWING NO. - SỐ HIỆU BẢN VẼ	KÝ HIỆU BẢN VẼ
				ThS.KTS. ĐỖ QUỐC HIỆP	KTS. TRẦN TRUNG KIẾN	MẶT BẰNG BỐ TRÍ NỘI THẤT PHÒNG MASTER	NM-01	N					

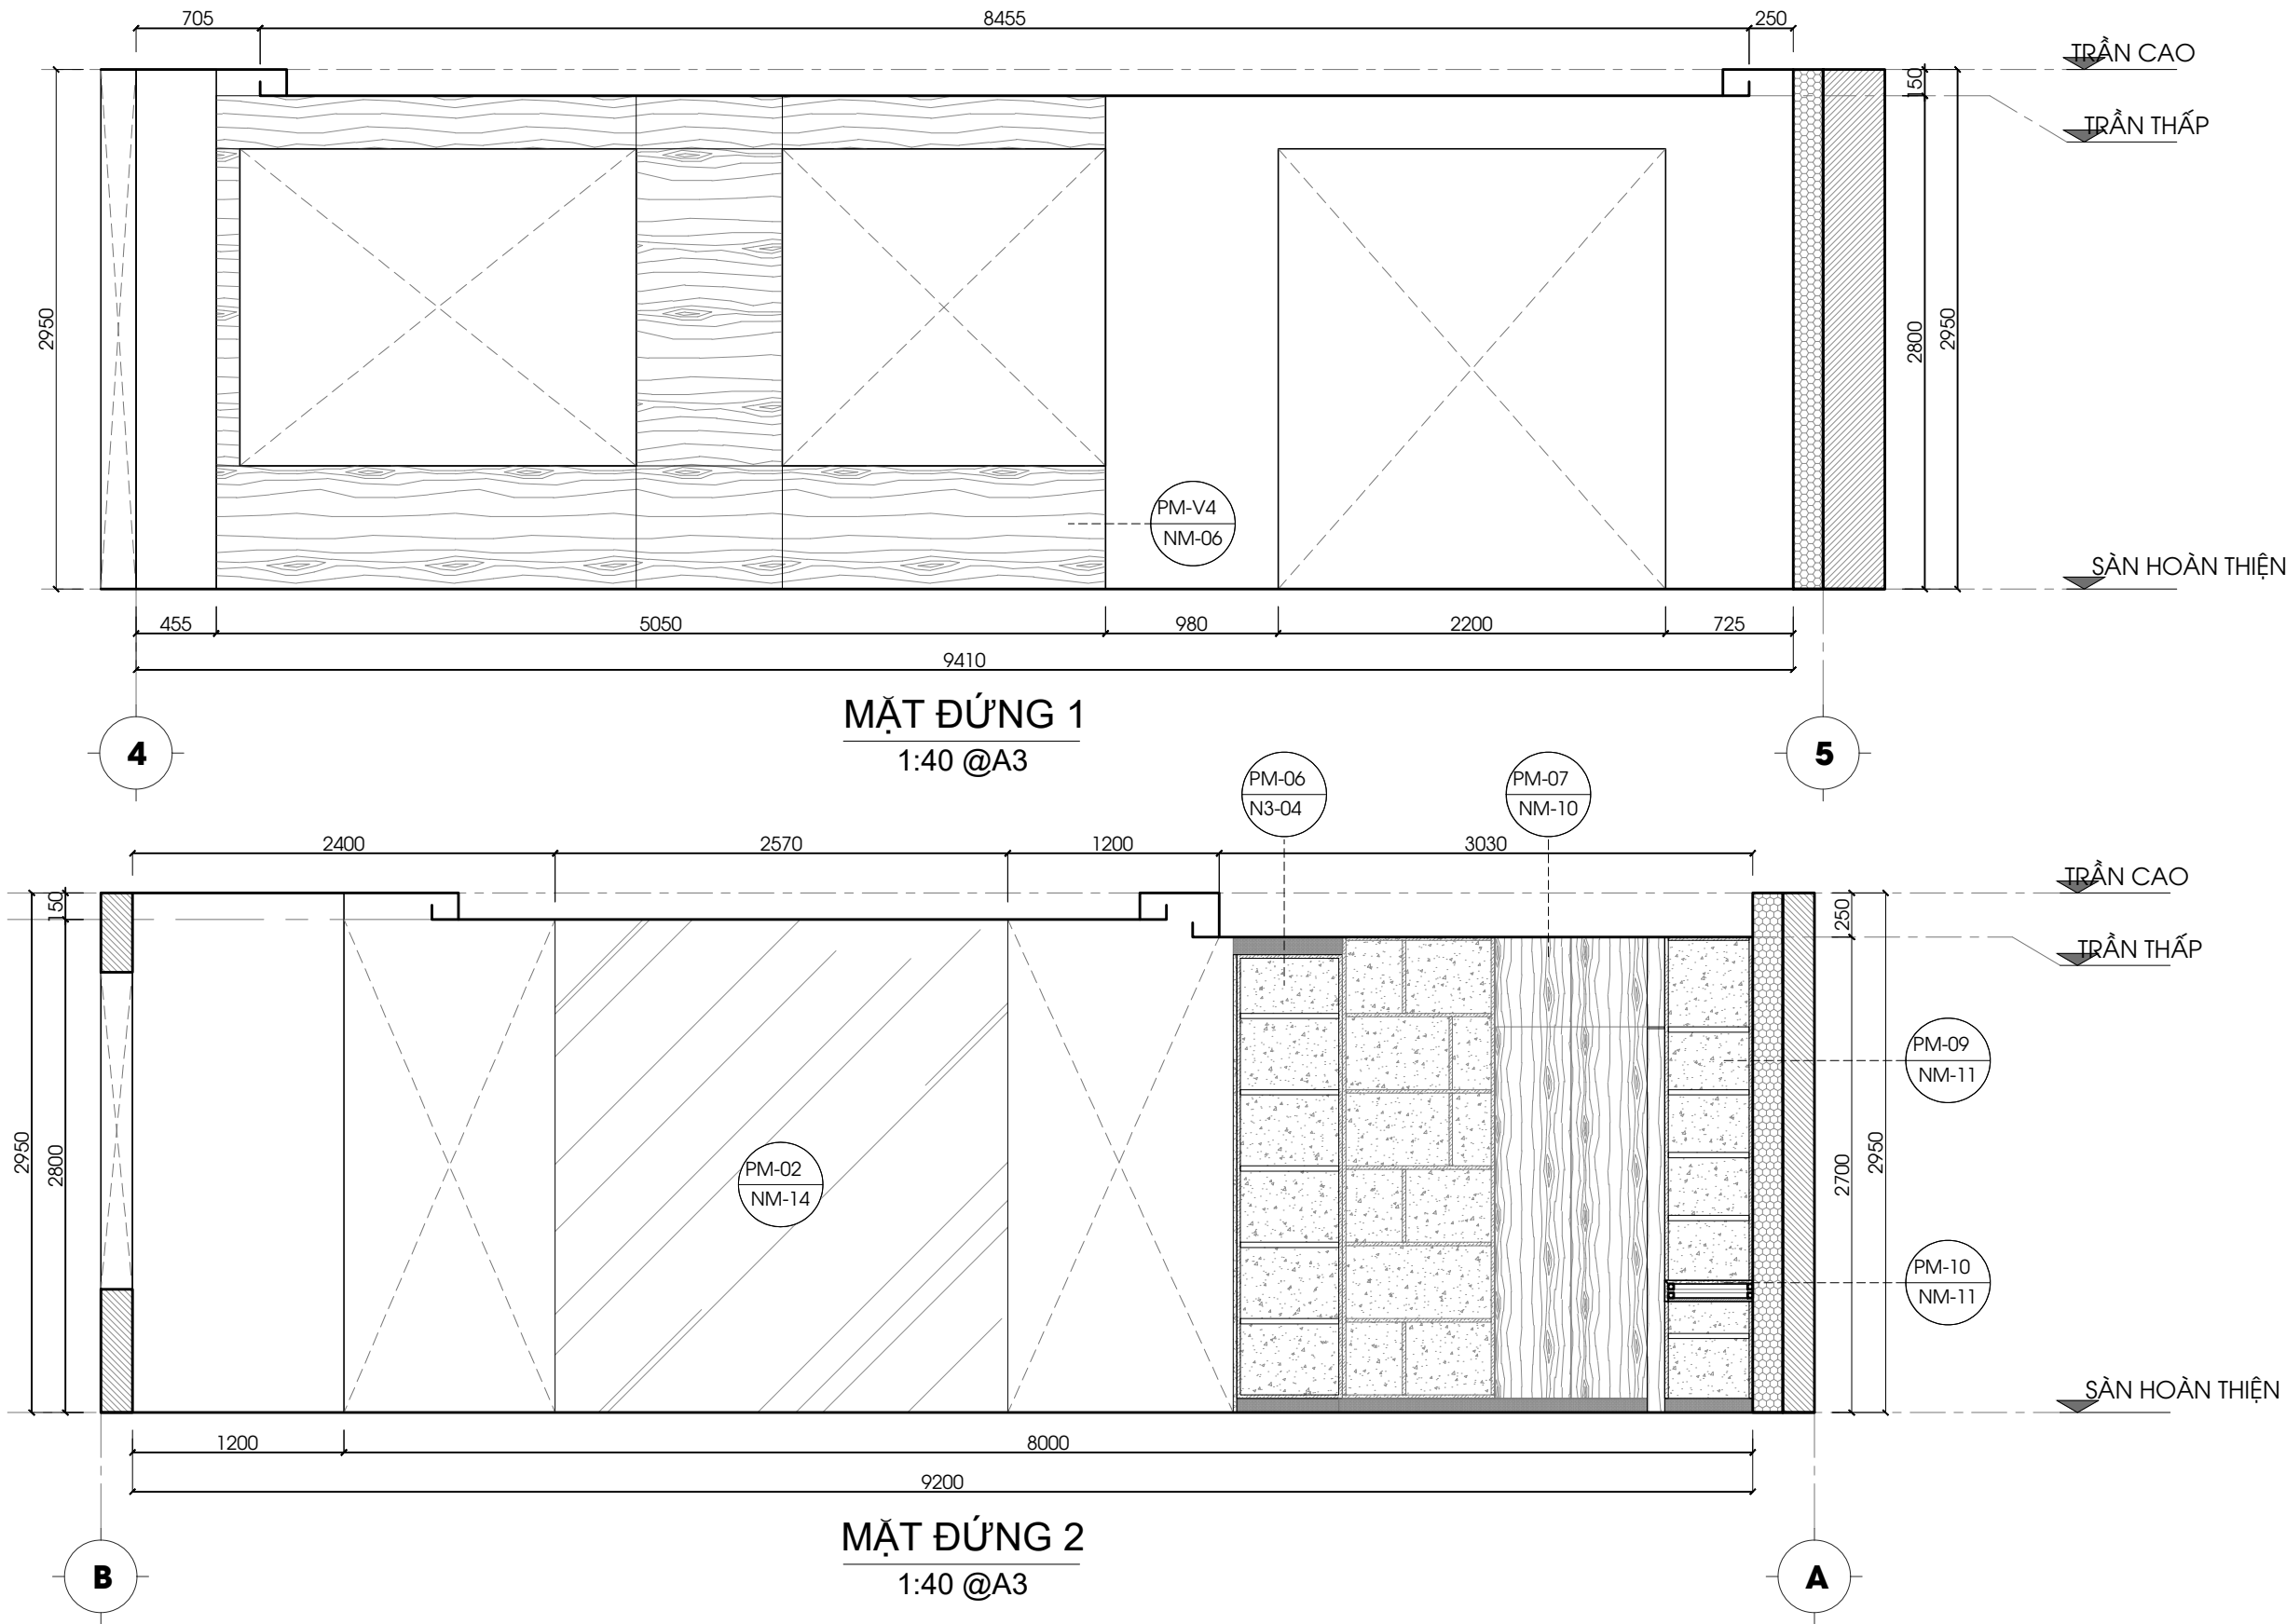

PHÁT HÀNH		HIỆU CHÍNH		GHI CHÚ	ARCHITECTURAL DESIGN — THIẾT KẾ KIẾN TRÚC		DESIGNER - CHỦ TRÌ THIẾT KẾ		PROJECT TITLE - TÊN DỰ ÁN		DATE - NGÀY	
					- MỌI KÍCH THƯỚC CẦN ĐƯỢC KIỂM TRA THEO THỰC TẾ CÔNG TRƯỜNG	CÔNG TY TNHH KIẾN TRÚC VIỆT VACO DESIGN LẦU 1, 3bis PHAN VĂN ĐẠT - P. BẾN NGHÉ - Q.1 - TP. HCM TEL: +84-9-36233584 EMAIL: info@vacodesign.com	ThS.KTS. ĐỖ QUỐC HIỆP	CĂN HỘ 08.03- 08.04-08.05-08.06	03 - 2025	SCALE - TỈ LỆ 1:40		
				DIRECTOR - GIÁM ĐỐC	DRAWN BY - NGƯỜI VẼ	DRAWING TITLE - TÊN BẢN VẼ	DRAWING NO. - SỐ HIỆU BẢN VẼ	KÝ HIỆU BẢNG VẼ				
				ThS.KTS. ĐỖ QUỐC HIỆP	KTS. TRẦN TRUNG KIẾN	MẶT ĐỨNG 1 MẶT ĐỨNG 2	NM-02	N				

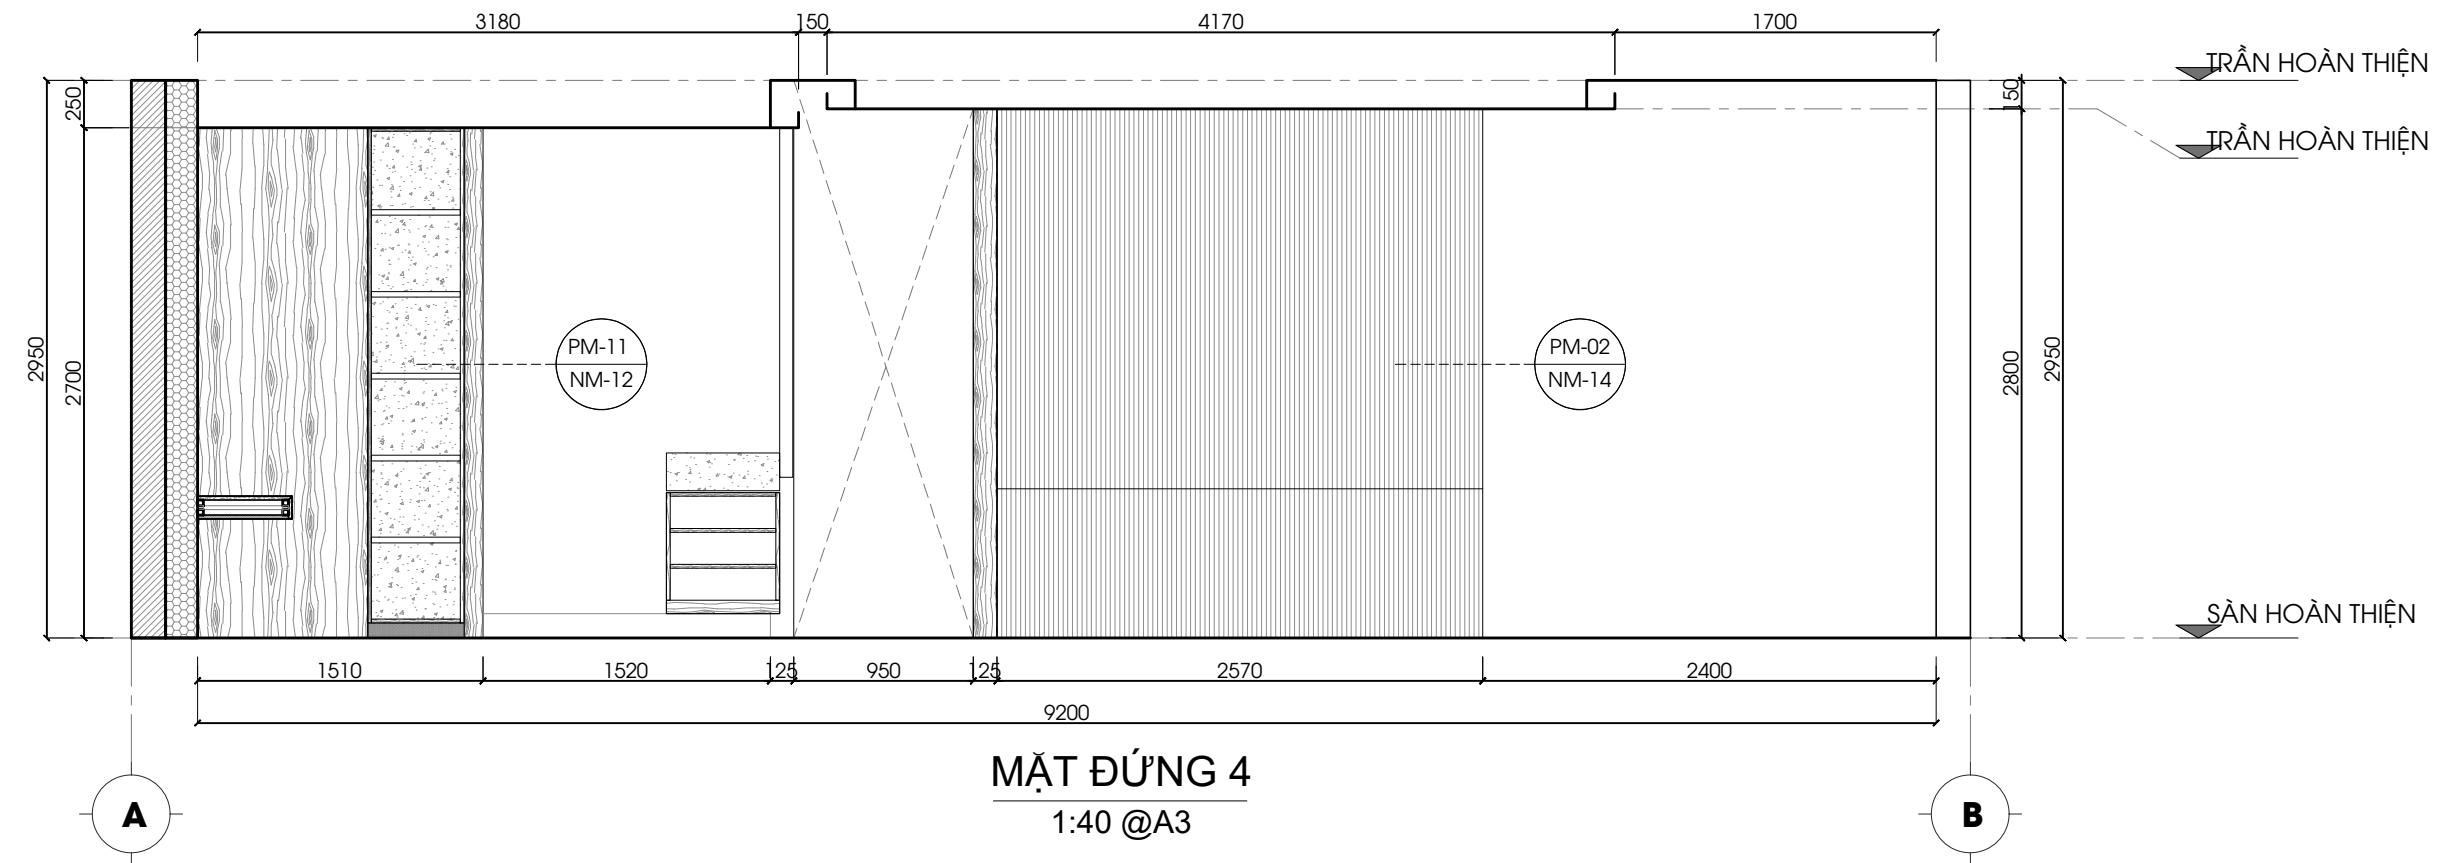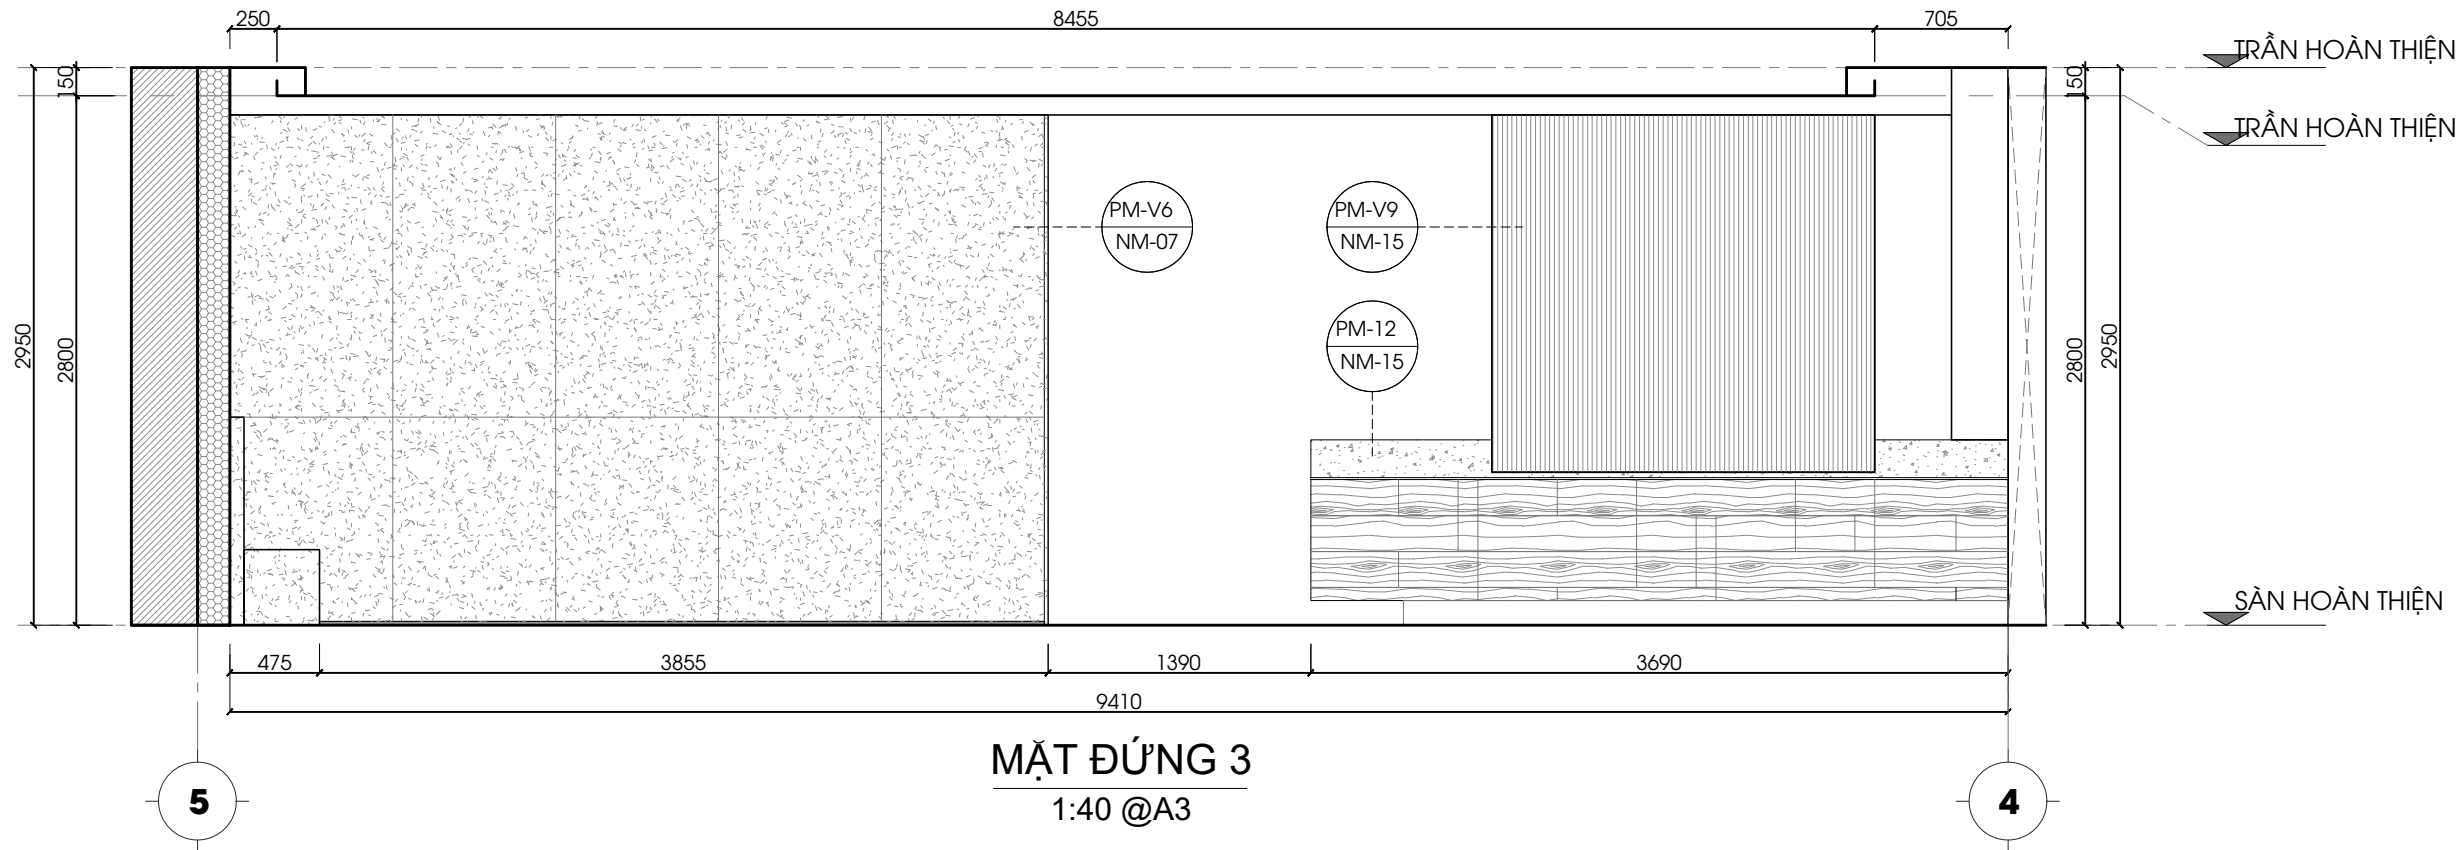


PHÁT HÀNH		HIỆU CHÍNH		GHI CHÚ	ARCHITECTURAL DESIGN — THIẾT KẾ KIẾN TRÚC		DESIGNER - CHỦ TRÌ THIẾT KẾ		PROJECT TITLE - TÊN DỰ ÁN		DATE - NGÀY	
					- MỌI KÍCH THƯỚC CẦN ĐƯỢC KIỂM TRA THEO THỰC TẾ CÔNG TRƯỜNG	CÔNG TY TNHH KIẾN TRÚC VIỆT VACO DESIGN LẦU 1, 3bis PHAN VĂN ĐẠT - P. BẾN NGHÉ - Q.1 - TP. HCM TEL: +84-9-38223384 EMAIL: info@vacodesign.com	ThS.KTS. ĐỖ QUỐC HIỆP	CĂN HỘ 08.03- 08.04-08.05-08.06	ThS.KTS. ĐỖ QUỐC HIỆP	CĂN HỘ 08.03- 08.04-08.05-08.06	DATE - NGÀY	
											SCALE - TỈ LỆ	
											1:40	
											DRAWING NO. - SỐ HIỆU BẢN VẼ	KÝ HIỆU BẢNG VẼ
											DRAWING TITLE - TÊN BẢN VẼ	
				MẶT ĐỨNG 3 MẶT ĐỨNG 4								
				ThS.KTS. ĐỖ QUỐC HIỆP		KTS. TRẦN TRUNG KIẾN				NM-03		
										N		

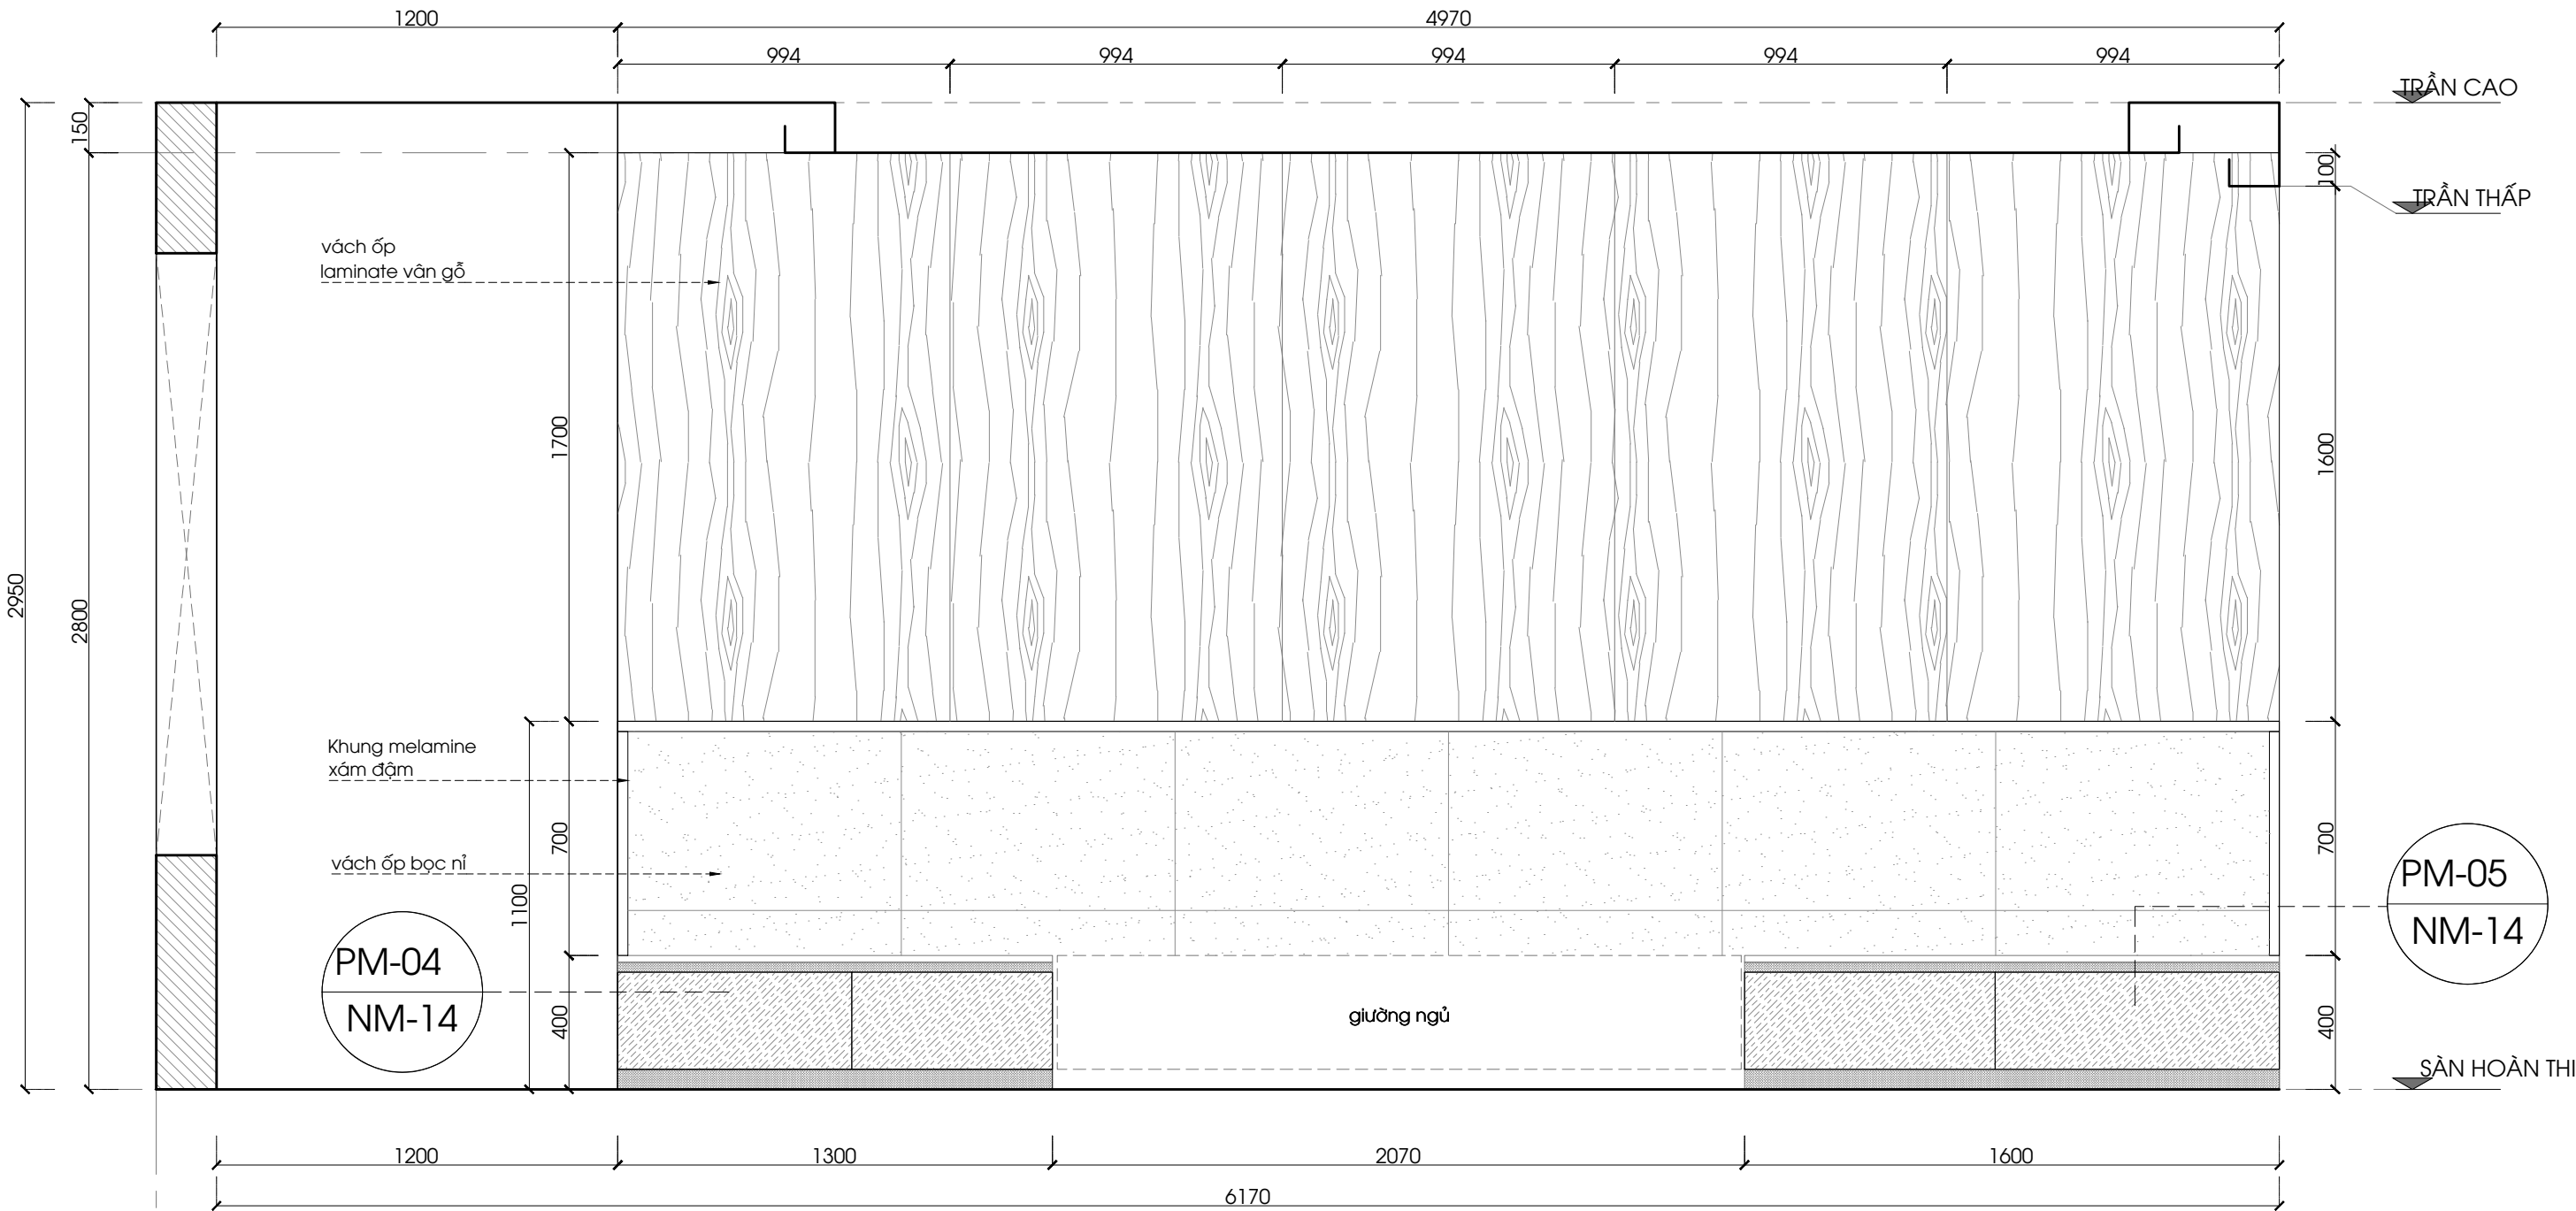


MẶT ĐỨNG 2'
1:20 @A3

PHÁT HÀNH		HIỆU CHÍNH		GHI CHÚ	ARCHITECTURAL DESIGN — THIẾT KẾ KIẾN TRÚC CÔNG TY TNHH KIẾN TRÚC VIỆT VACO DESIGN LẦU 1, 3bis PHAN VĂN ĐẠT - P. BẾN NGHÉ - Q.1 - TP. HCM TEL: +84-9-36223364 EMAIL: info@vacodesign.com DESIGN DIRECTOR - GIÁM ĐỐC ThS.KTS. ĐỖ QUỐC HIỆP	DESIGNER - CHỦ TRÌ THIẾT KẾ ThS.KTS. ĐỖ QUỐC HIỆP DRAWN BY - NGƯỜI VẼ KTS. TRẦN TRUNG KIẾN	PROJECT TITLE - TÊN DỰ ÁN CĂN HỘ 08.03- 08.04-08.05-08.06	DATE - NGÀY	
								03 - 2025	
							SCALE - TỈ LỆ		
							1:20		
							DRAWING TITLE - TÊN BẢN VẼ MẶT ĐỨNG 2'	DRAWING NO. - SỐ HIỆU BẢN VẼ NM-04	KÝ HIỆU BẢNG VẼ N

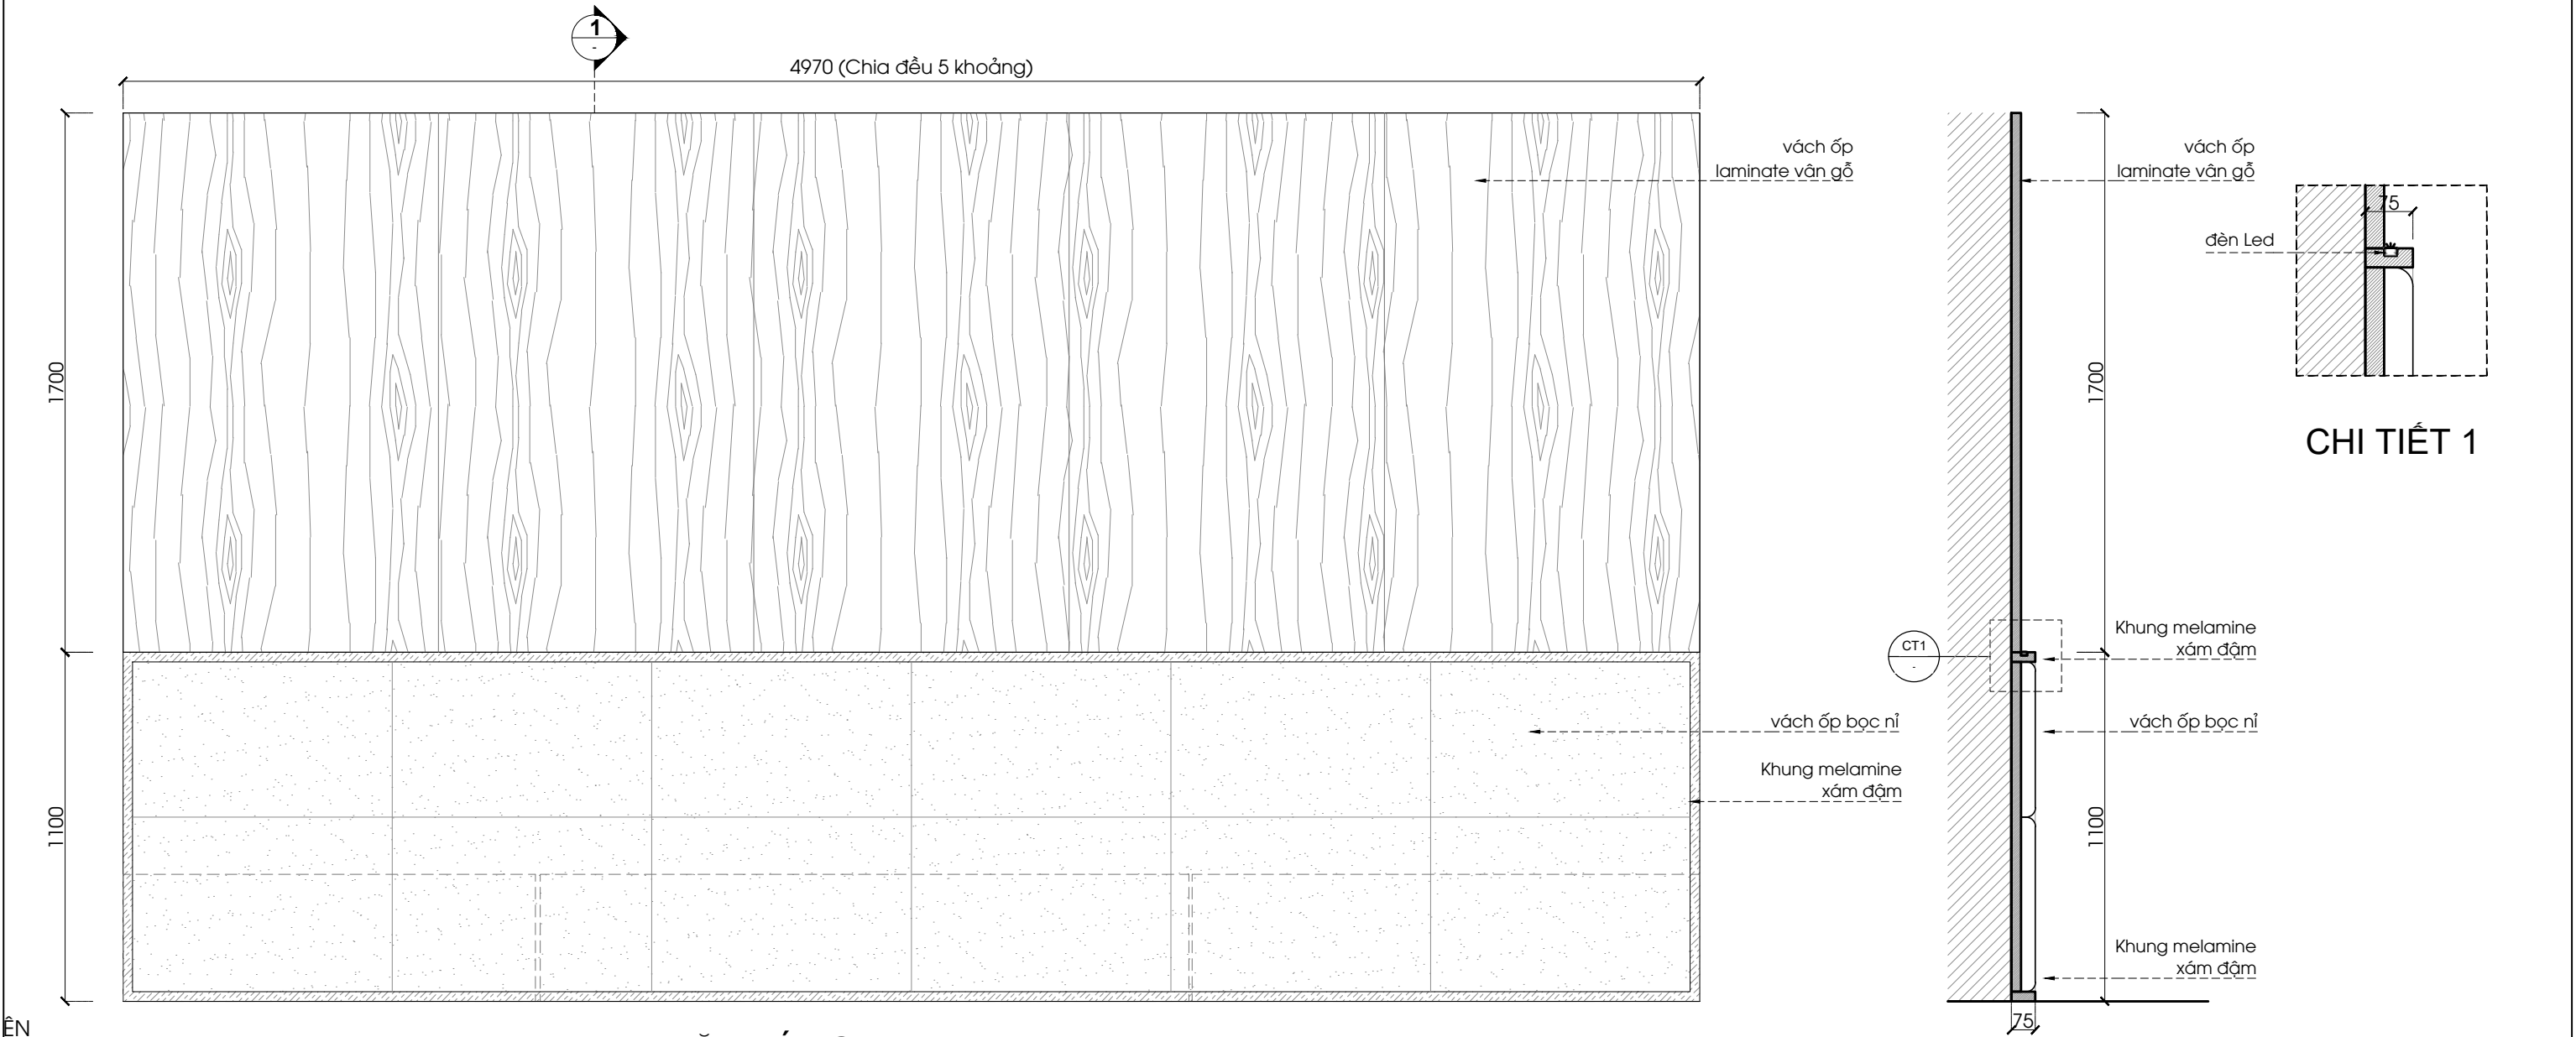


MẶT ĐỪNG PM-V4, PM-03
1:20 @A3


MẶT CẮT 1
1:20 @A3

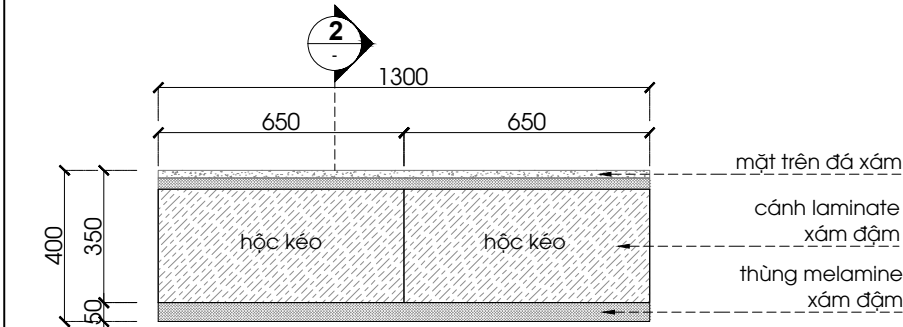

MẶT ĐỪNG PM-04
1:20 @A3

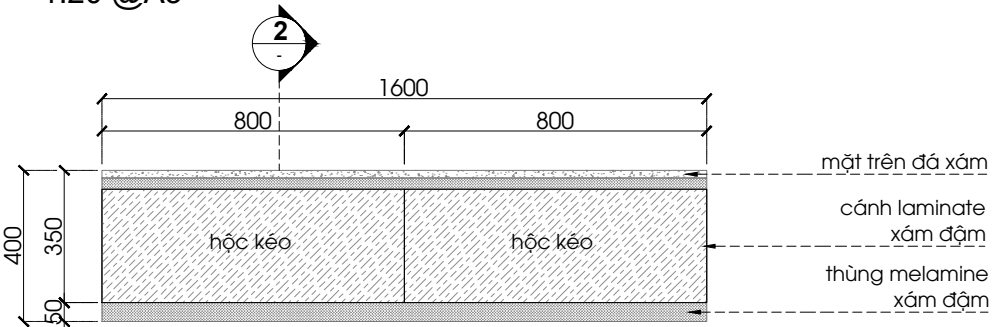


MẶT ĐỪNG PM-05
1:20 @A3

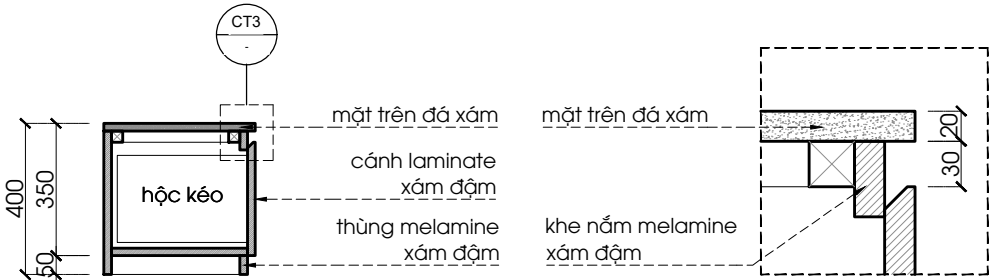

MẶT CẮT 2
1:20 @A3


CHI TIẾT 3

PHÁT HÀNH		HIỆU CHỈNH		GHI CHÚ	ARCHITECTURAL DESIGN — THIẾT KẾ KIẾN TRÚC		DESIGNER - CHỦ TRÌ THIẾT KẾ		PROJECT TITLE - TÊN DỰ ÁN		DATE - NGÀY	
					- MỌI KÍCH THƯỚC CẦN ĐƯỢC KIỂM TRA THEO THỰC TẾ CÔNG TRƯỜNG	CÔNG TY TNHH KIẾN TRÚC VIỆT VACO DESIGN LẦU 1, 38/6 PHAN VĂN DAT - P. BẾN NGHÉ - Q.1 - TP. HCM TEL: +84-9-36223364 EMAIL: info@vacodesign.com	ThS.KTS. ĐỖ QUỐC HIỆP	CĂN HỘ 08.03- 08.04-08.05-08.06	03 - 2025	SCALE - TỈ LỆ 1:20		
				DIRECTOR - GIÁM ĐỐC	DRAWN BY - NGƯỜI VẼ	DRAWING TITLE - TÊN BẢN VẼ	DRAWING NO. - SỐ HIỆU BẢN VẼ	KÝ HIỆU BẢNG VẼ				
				ThS.KTS. ĐỖ QUỐC HIỆP	KTS. TRẦN TRUNG KIẾN	CHI TIẾT PM-V04, PM-03, PM-04, 05	NM-05	N				

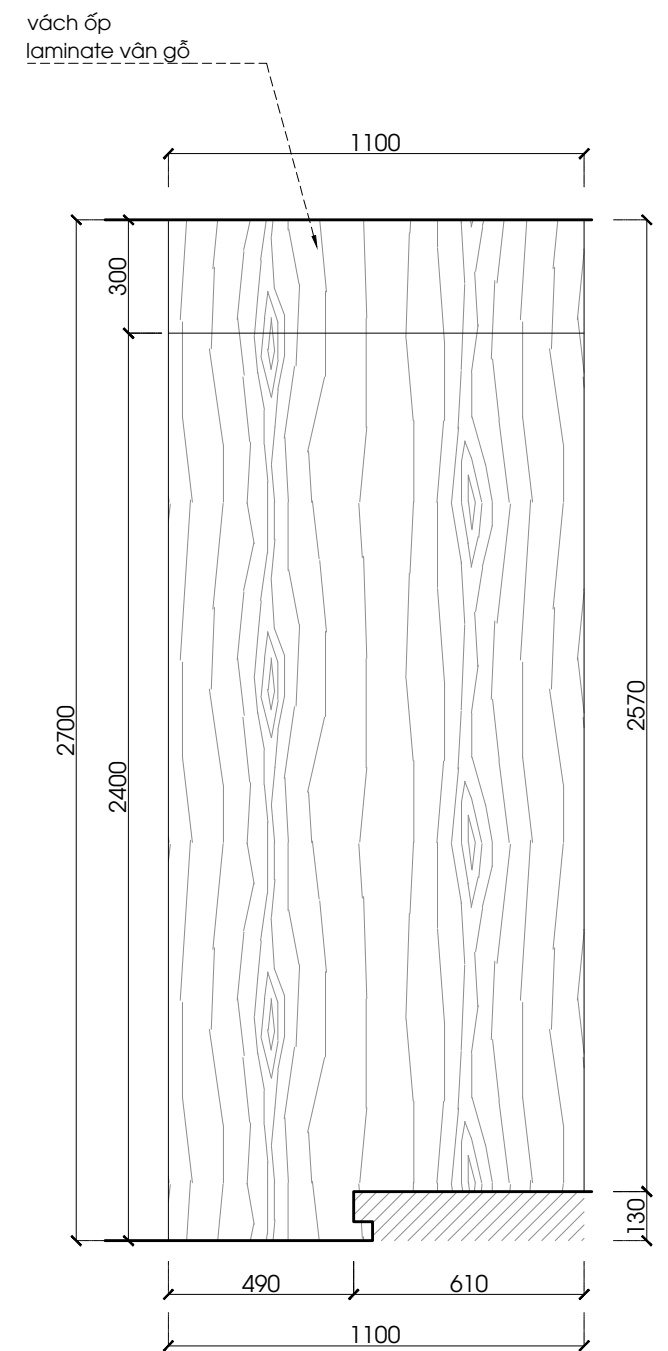


MẶT ĐÚNG PM-V8
1:20 @A3

PHÁT HÀNH		HIỆU CHỈNH		GHI CHÚ - MỌI KÍCH THƯỚC CẦN ĐƯỢC KIỂM TRA THEO THỰC TẾ CÔNG TRƯỜNG	ARCHITECTURAL DESIGN — THIẾT KẾ KIẾN TRÚC DESIGN CÔNG TY TNHH KIẾN TRÚC VIỆT VACO DESIGN LẦU 1, 3b/6 PHAN VĂN DÁT - P. BẾN NGHÉ - Q.1 - TP. HCM TEL: +84-8-38223384 EMAIL: info@vacodesign.com		DESIGNER - CHỦ TRÌ THIẾT KẾ	PROJECT TITLE - TÊN DỰ ÁN	DATE - NGÀY 03 - 2025		
					SCALE - TỈ LỆ 1:20						
					DRAWING NO. - SỐ HIỆU BẢN VẼ	KÝ HIỆU BẢNG VẼ					
				DIRECTOR - GIÁM ĐỐC	ThS.KTS. ĐỖ QUỐC HIỆP	DRAWN BY - NGƯỜI VẼ	KTS. TRẦN TRUNG KIẾN	DRAWING TITLE - TÊN BẢN VẼ	CHI TIẾT PM-V4, PM-V8	NM-06	N

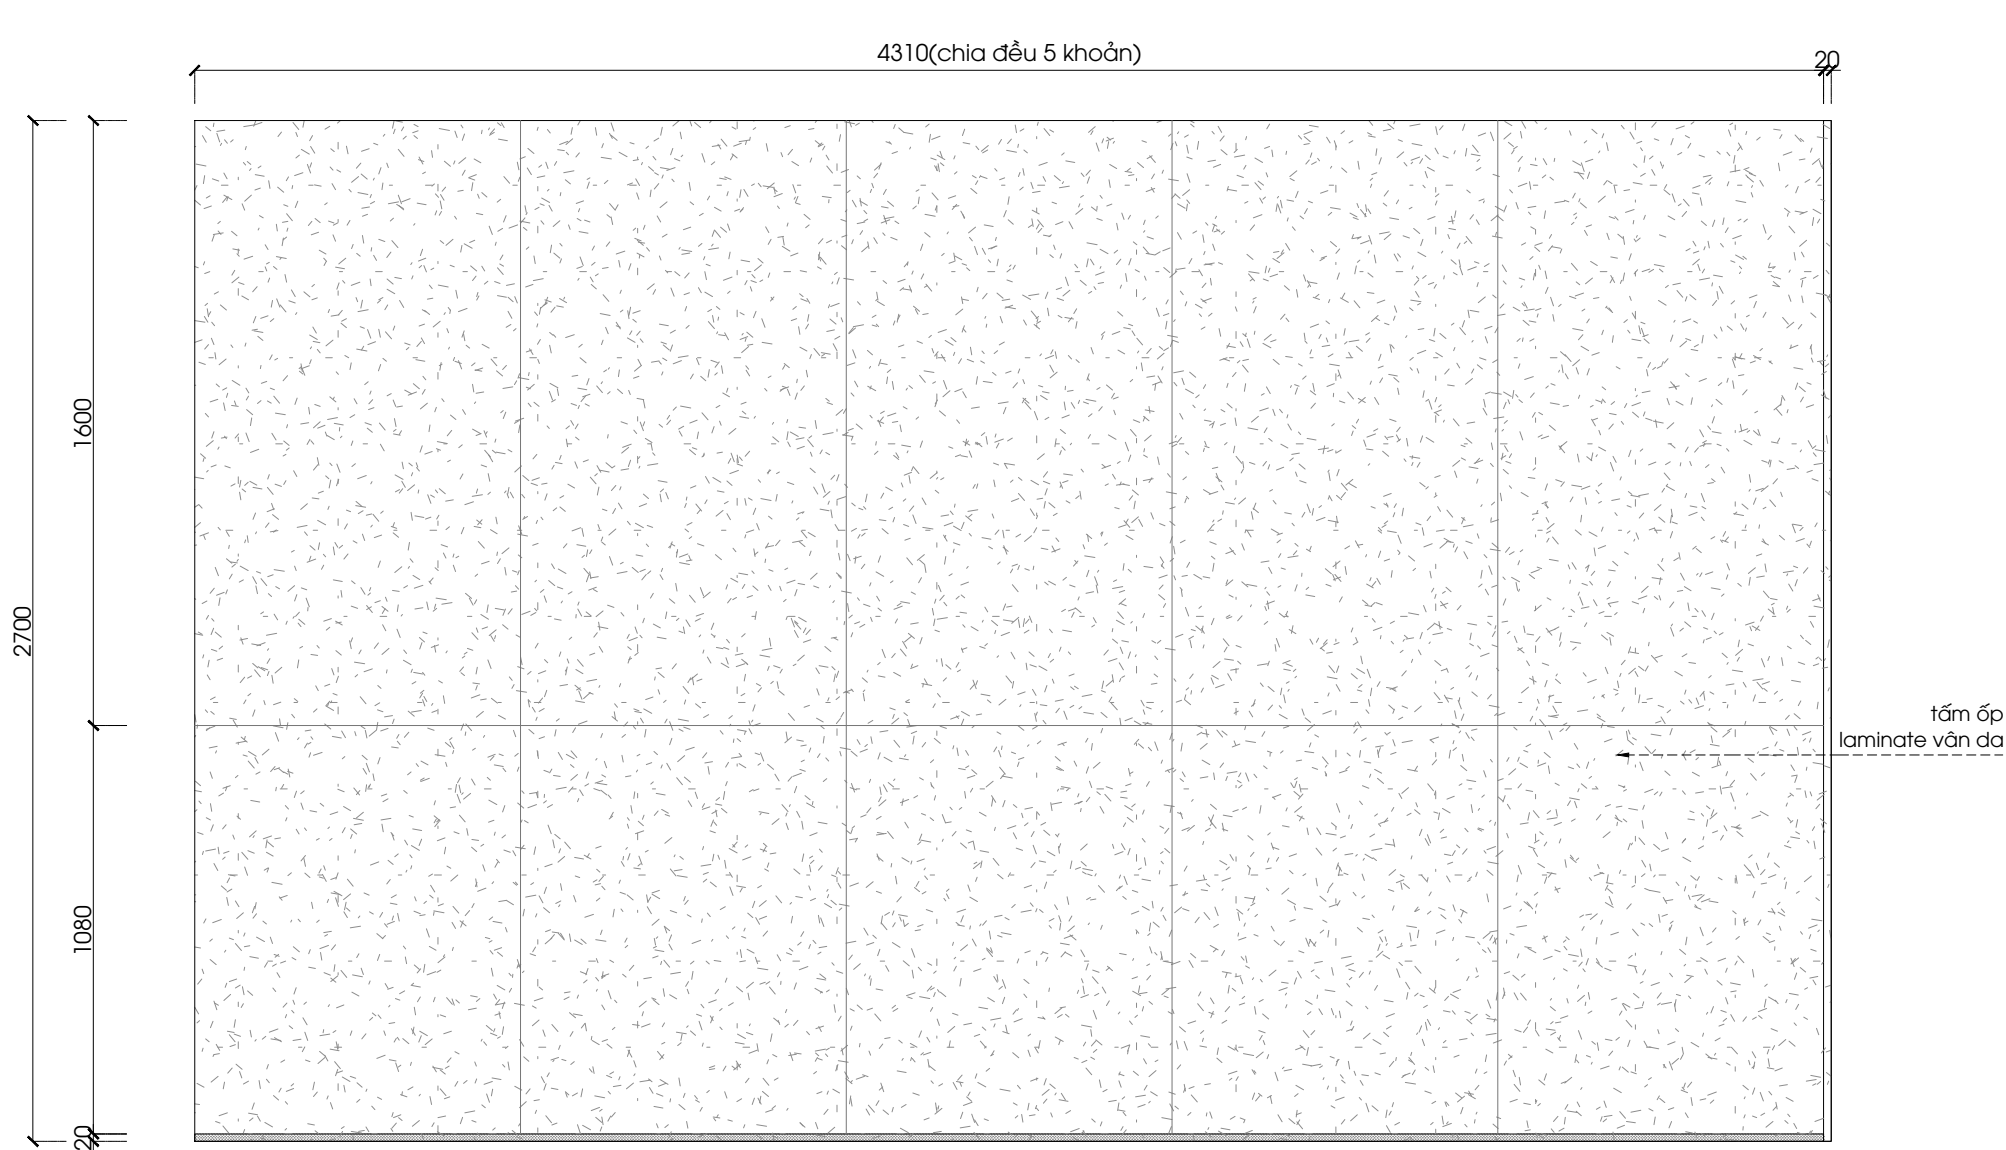


MẶT ĐỪNG PM-V6
1:20 @A3

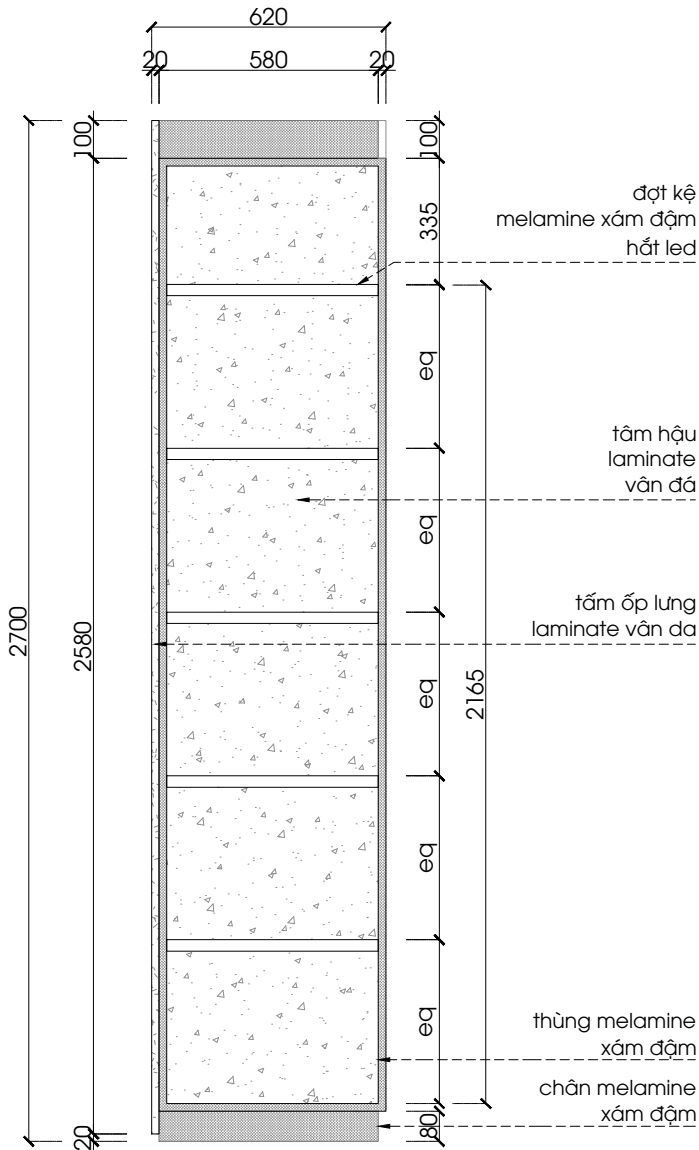


MẶT ĐỪNG PM-06
1:20 @A3

PHÁT HÀNH		HIỆU CHỈNH		GHI CHÚ	ARCHITECTURAL DESIGN — THIẾT KẾ KIẾN TRÚC		DESIGNER - CHỦ TRÌ THIẾT KẾ		PROJECT TITLE - TÊN DỰ ÁN		DATE - NGÀY	
					CÔNG TY TNHH KIẾN TRÚC VIỆT VACO DESIGN LẦU 1, 3bis PHAN VĂN ĐẠT - P. BẾN NGHÉ - Q.1 - TP. HCM TEL: +84-8-36233364 EMAIL: info@vacodesign.com			CĂN HỘ 08.03- 08.04-08.05-08.06	SCALE - TỈ LỆ	1:20		
- MỌI KÍCH THƯỚC CẦN ĐƯỢC KIỂM TRA THEO THỰC TẾ CÔNG TRƯỜNG					DIRECTOR - GIÁM ĐỐC	DRAWN BY - NGƯỜI VẼ	DRAWING TITLE - TÊN BẢN VẼ	DRAWING NO. - SỐ HIỆU BẢN VẼ	KÝ HIỆU BẢNG VẼ			
				ThS.KTS. ĐỖ QUỐC HIỆP	KTS. TRẦN TRUNG KIẾN	CHI TIẾT PM-V6, PM-06	NM-07	N				

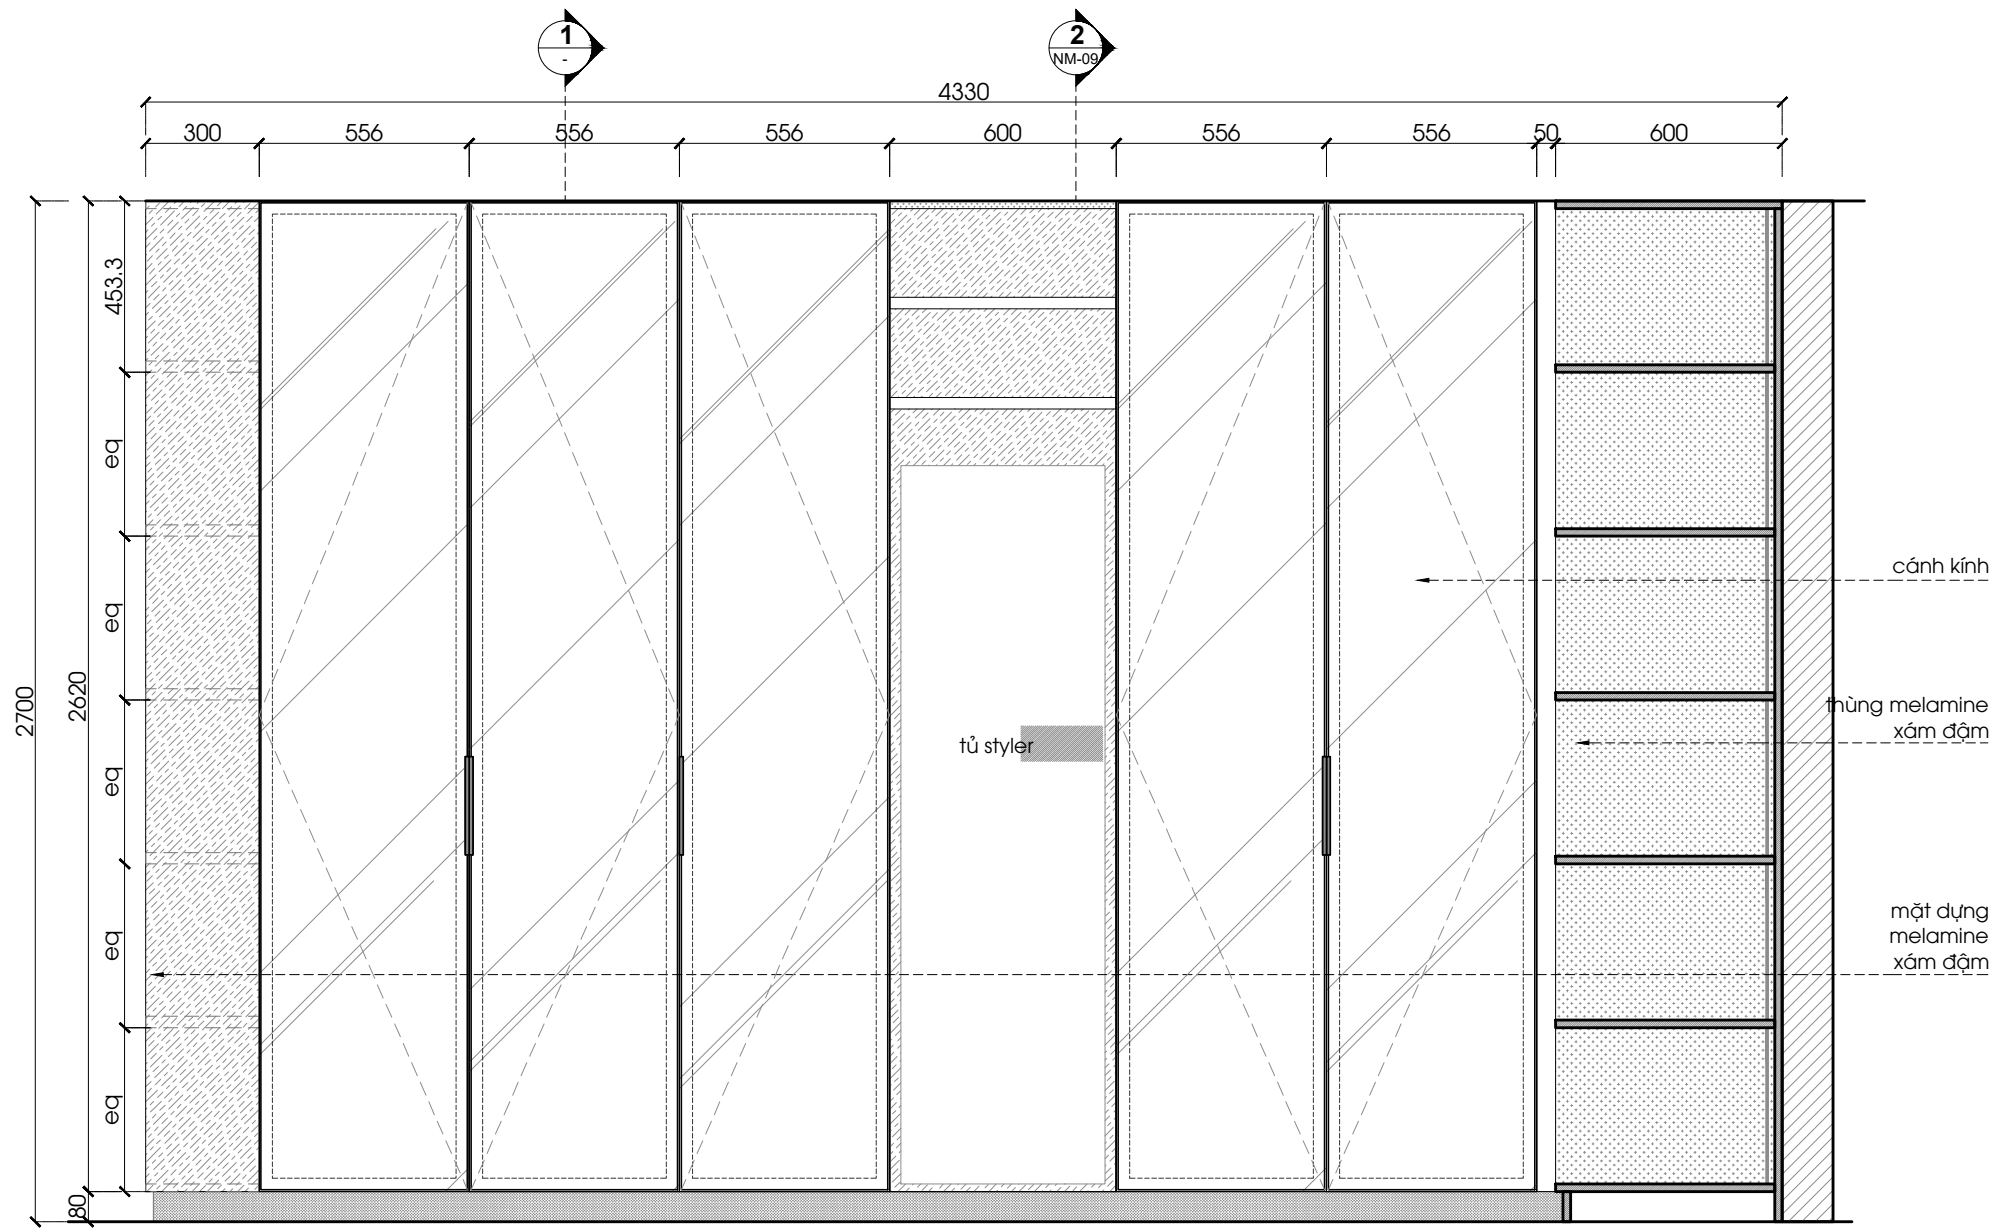


MẶT ĐỨNG PM-06
1:20 @A3

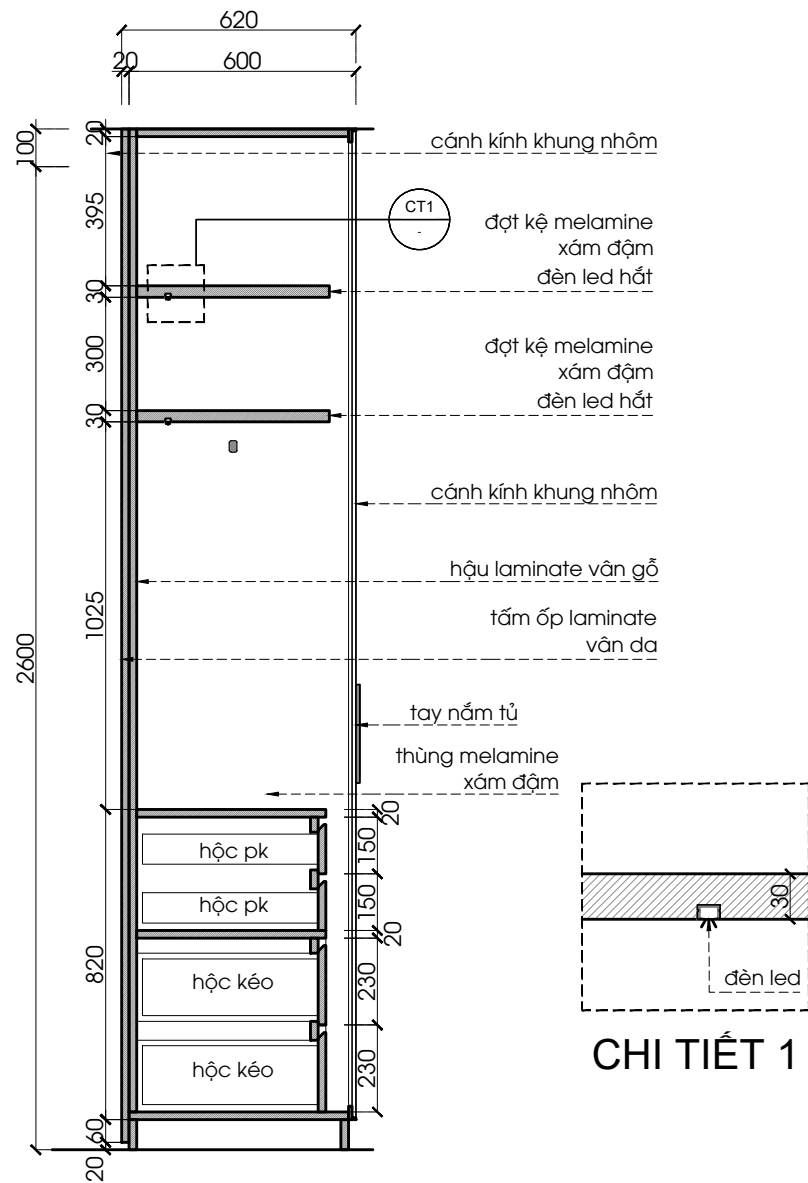

MẶT CẮT 1
1:20 @A3


PHÁT HÀNH		HIỆU CHÍNH		GHI CHÚ - MỌI KÍCH THƯỚC CẦN ĐƯỢC KIỂM TRA THEO THỰC TẾ CÔNG TRƯỜNG	ARCHITECTURAL DESIGN — THIẾT KẾ KIẾN TRÚC CÔNG TY TNHH KIẾN TRÚC VIỆT VACO DESIGN LẦU 1, 3bis PHAN VĂN ĐẠT - P. BẾN NGHÉ - Q.1 - TP. HCM TEL: +84-9-36223384 EMAIL: info@vacodesign.com	DESIGNER - CHỦ TRÌ THIẾT KẾ ThS.KTS. ĐỖ QUỐC HIỆP	PROJECT TITLE - TÊN DỰ ÁN CĂN HỘ 08.03- 08.04-08.05-08.06	DATE - NGÀY 03 - 2025	
								SCALE - TỈ LỆ 1:20	
								DRAWING NO. - SỐ HIỆU BẢN VẼ NM-08	KÝ HIỆU BẢNG VẼ N
					ThS.KTS. ĐỖ QUỐC HIỆP	KTS. TRẦN TRUNG KIẾN	CHI TIẾT PM-06		

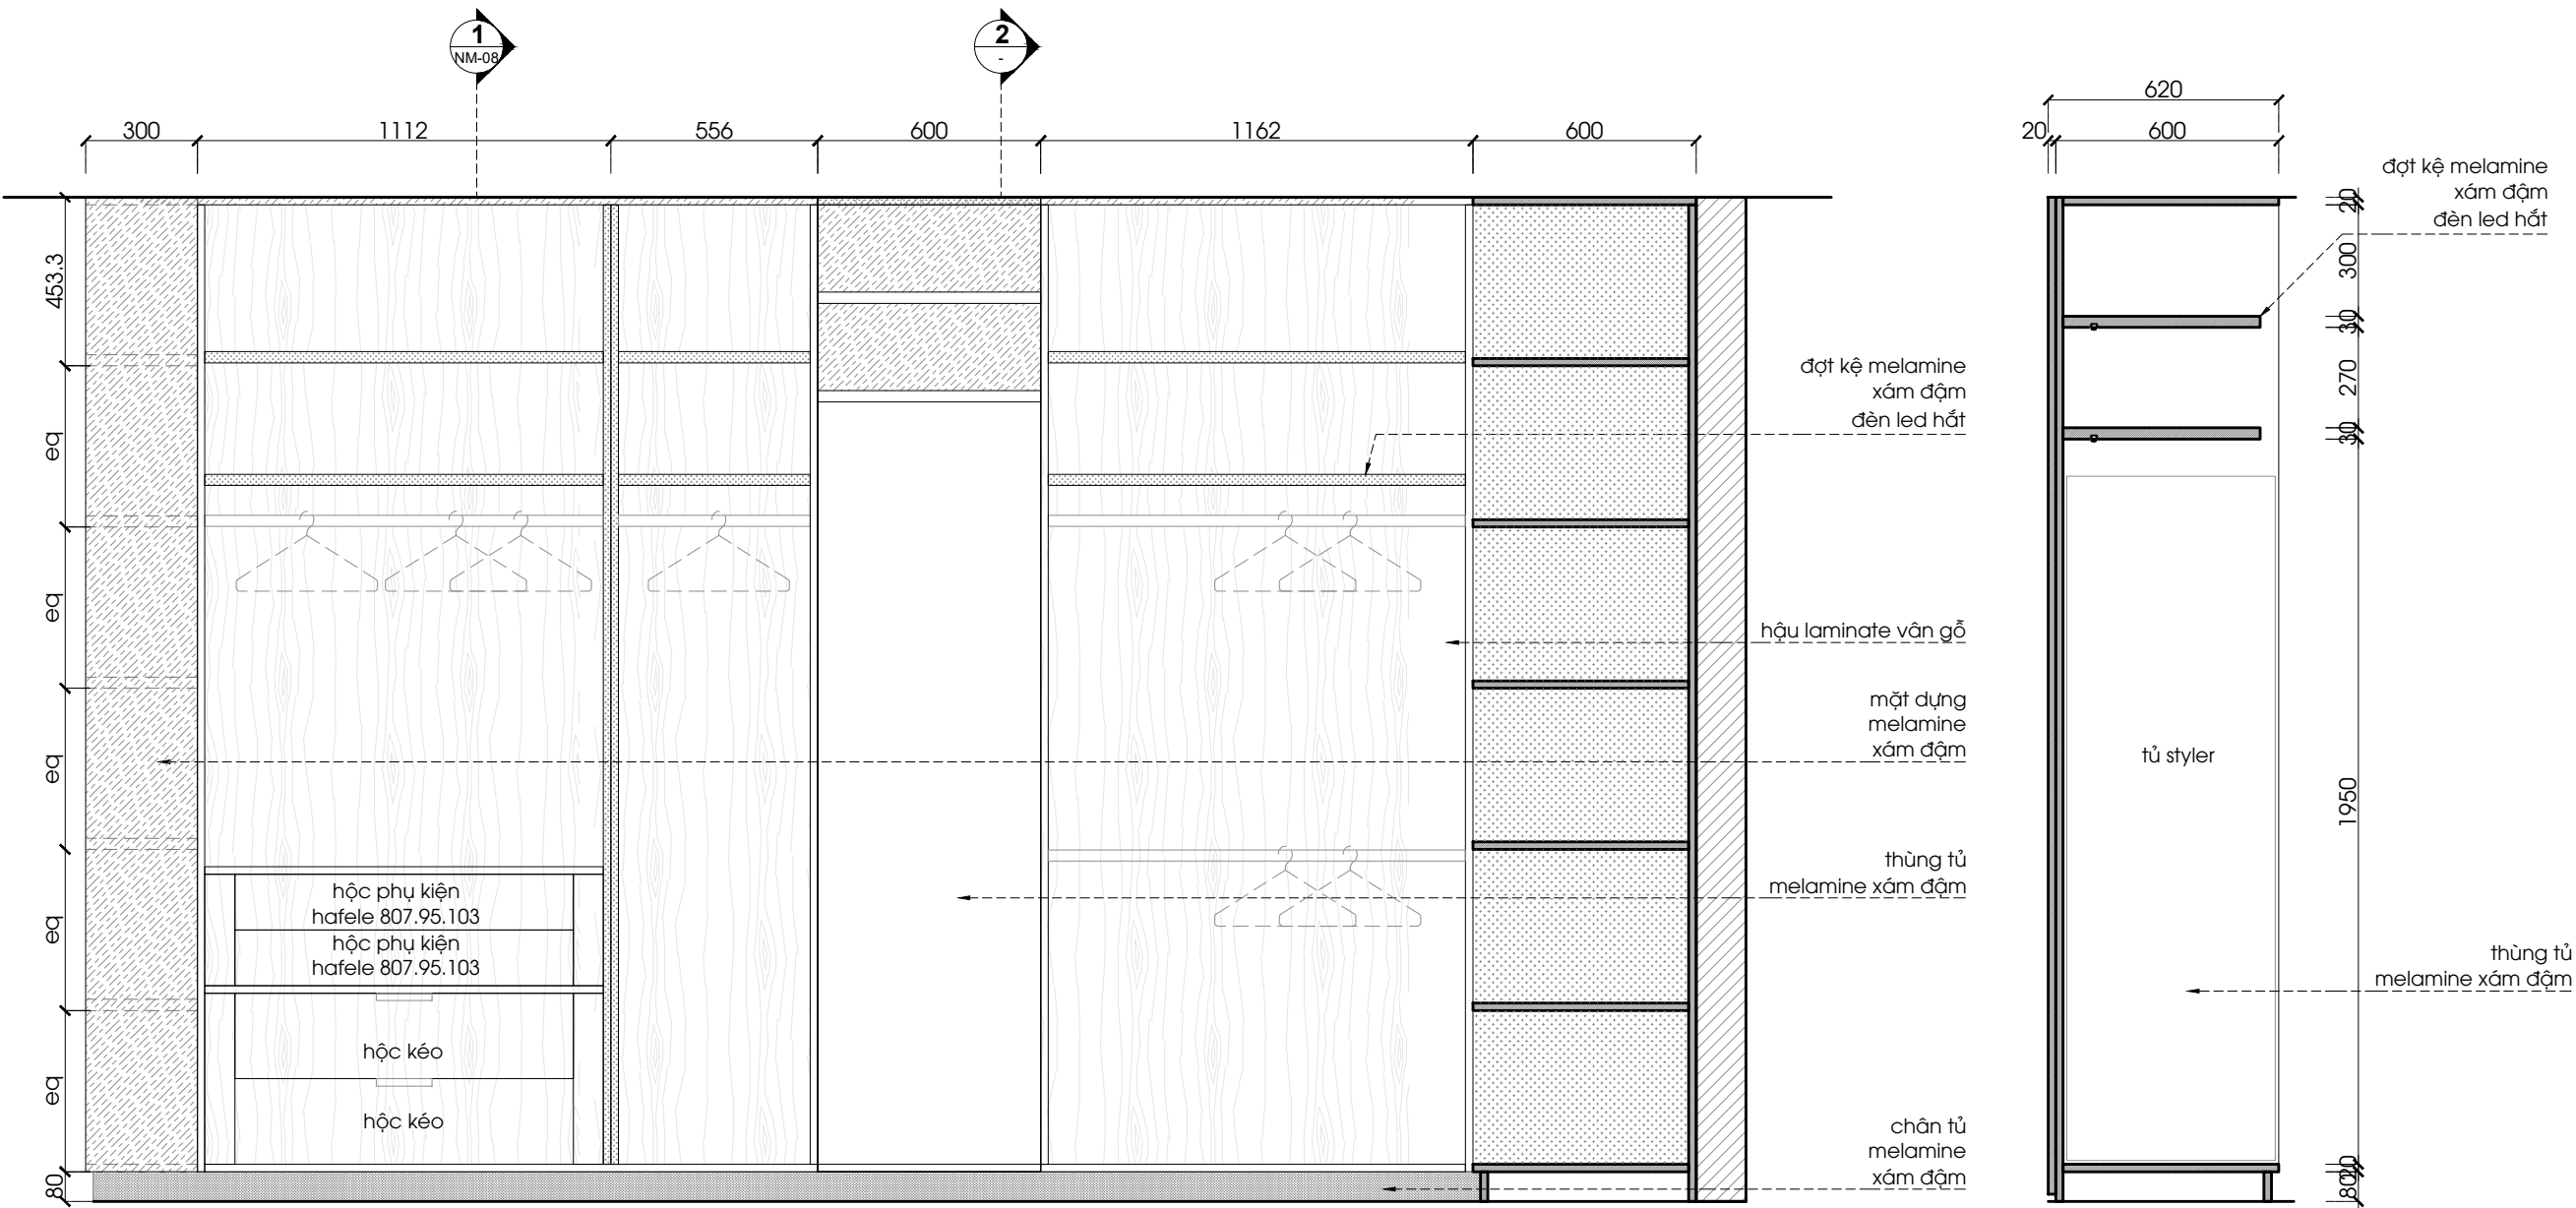


MẶT ĐỨNG THÙNG TỦ PM-06
1:20 @A3

MẶT CẮT 2
1:20 @A3


PHÁT HÀNH		HIỆU CHÍNH		GHI CHÚ	ARCHITECTURAL DESIGN – THIẾT KẾ KIẾN TRÚC		DESIGNER - CHỦ TRÌ THIẾT KẾ		PROJECT TITLE - TÊN DỰ ÁN		DATE - NGÀY	
					CÔNG TY TNHH KIẾN TRÚC VIỆT VACO DESIGN LẦU 1, 38a PHAN VĂN ĐẠT - P. BẾN NGHÉ - Q.1 - TP. HCM TEL: +84-9-36223364 EMAIL: info@vacodesign.com				CĂN HỘ 08.03- 08.04-08.05-08.06		03 - 2025	
							ThS.KTS. ĐỖ QUỐC HIỆP		SCALE - TỈ LỆ		1:20	
									DRAWING TITLE - TÊN BẢN VẼ		DRAWING NO. - SỐ HIỆU BẢN VẼ	
									CHI TIẾT PM-06		NM-09	
						ThS.KTS. ĐỖ QUỐC HIỆP	KTS. TRẦN TRUNG KIẾN				KÝ HIỆU BẢNG VẼ	
				- MỌI KÍCH THƯỚC CẦN ĐƯỢC KIỂM TRA THEO THỰC TẾ CÔNG TRƯỜNG							N	

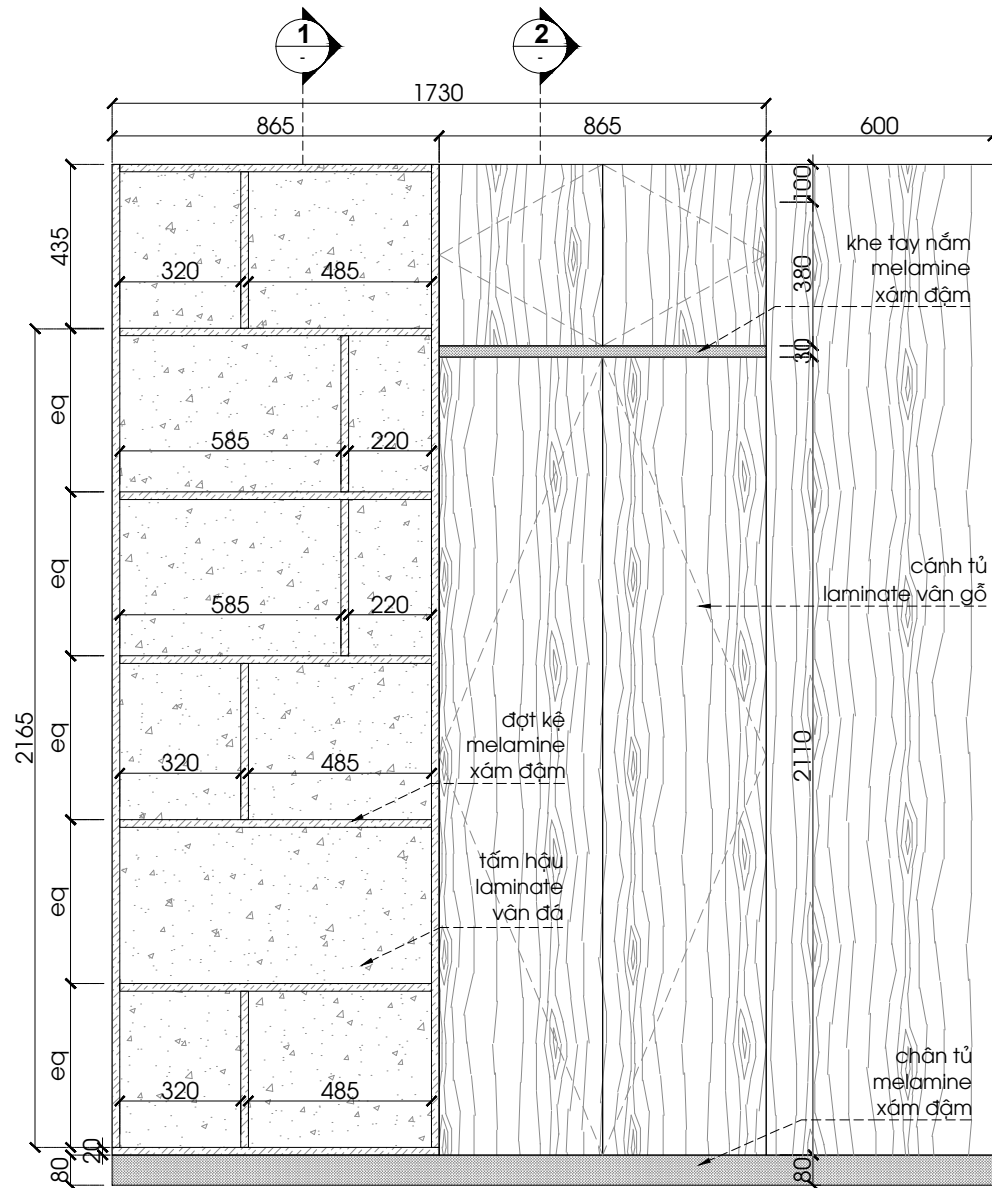


MẶT ĐỨNG PM-07
1:20 @A3

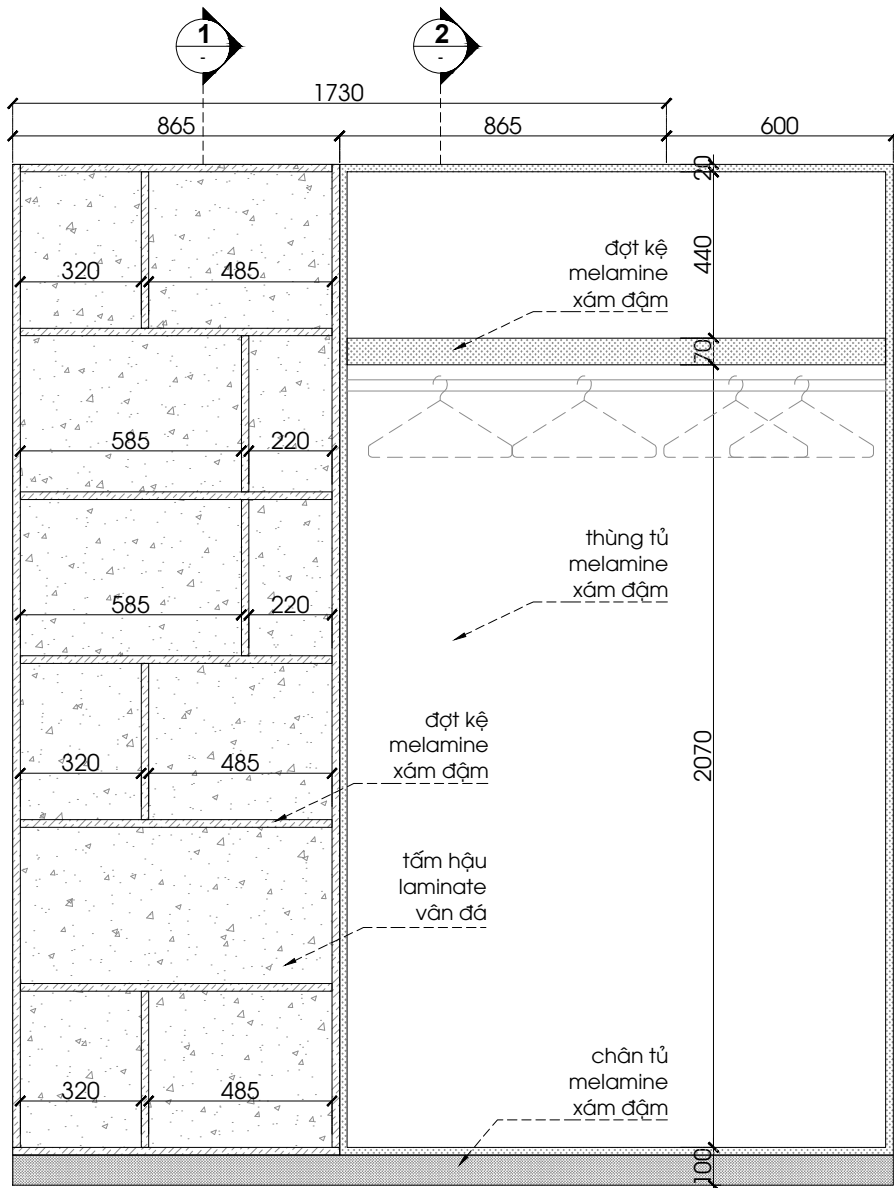

MẶT ĐỨNG - KHÔNG CÁNH PM-07
1:20 @A3

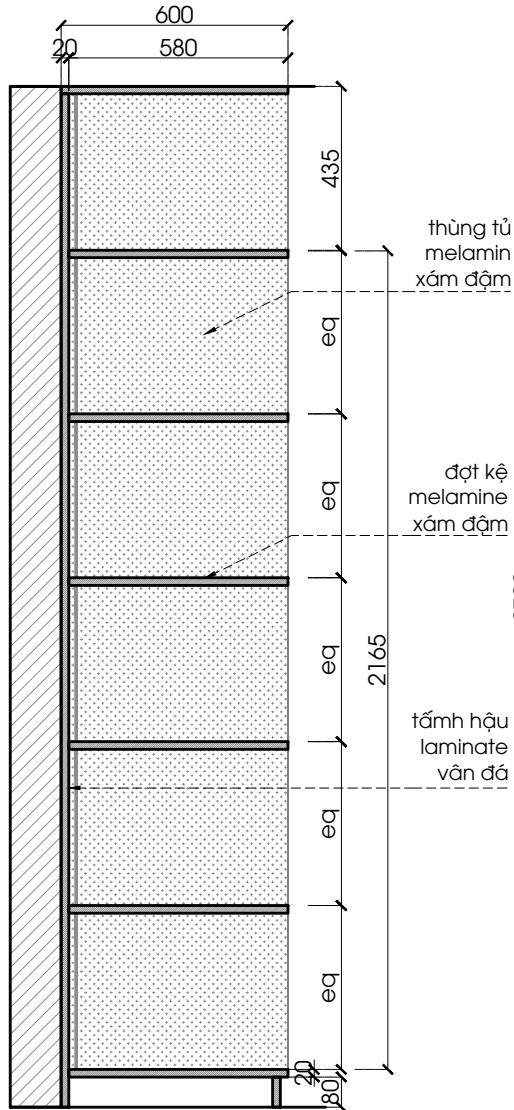


MẶT CẮT 1
1:20 @A3

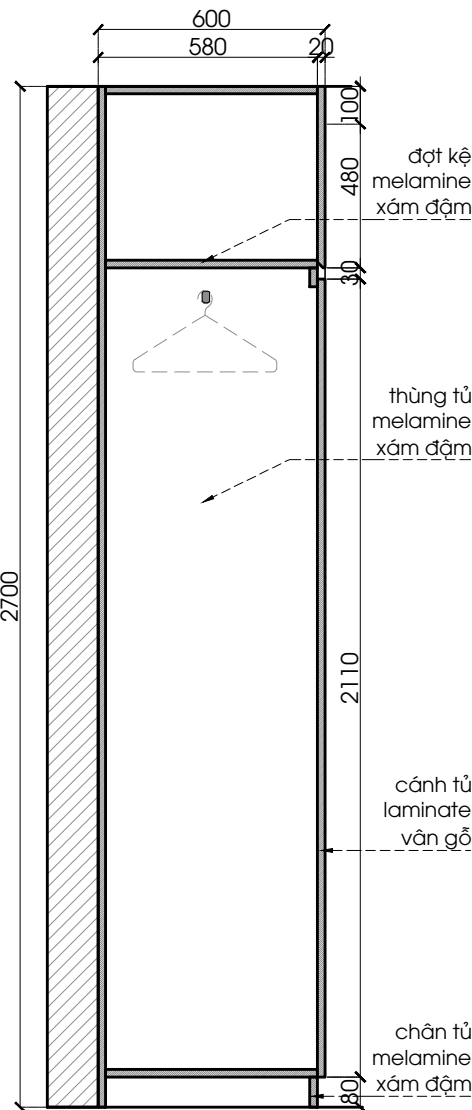


MẶT CẮT 2
1:20 @A3

PHÁT HÀNH		HIỆU CHÍNH		GHI CHÚ	ARCHITECTURAL DESIGN — THIẾT KẾ KIẾN TRÚC		DESIGNER - CHỦ TRÌ THIẾT KẾ		PROJECT TITLE - TÊN DỰ ÁN		DATE - NGÀY	
					CÔNG TY TNHH KIẾN TRÚC VIỆT VACO DESIGN LẦU 1, 3bis PHAN VĂN ĐẠT - P. BẾN NGHÉ - Q.1 - TP. HCM TEL: +84-9-36223364 EMAIL: info@vacodesign.com		ThS.KTS. ĐỖ QUỐC HIỆP		CĂN HỘ 08.03- 08.04-08.05-08.06		03 - 2025	
											SCALE - TỈ LỆ	
											1:20	
											DRAWING NO. - SỐ HIỆU BẢN VẼ	
				- MỌI KÍCH THƯỚC CẦN ĐƯỢC KIỂM TRA THEO THỰC TẾ CÔNG TRƯỜNG	ThS.KTS. ĐỖ QUỐC HIỆP		KTS. TRẦN TRUNG KIẾN		CHI TIẾT PM-07		NM-10	
											KÝ HIỆU BẢNG VẼ	
											N	

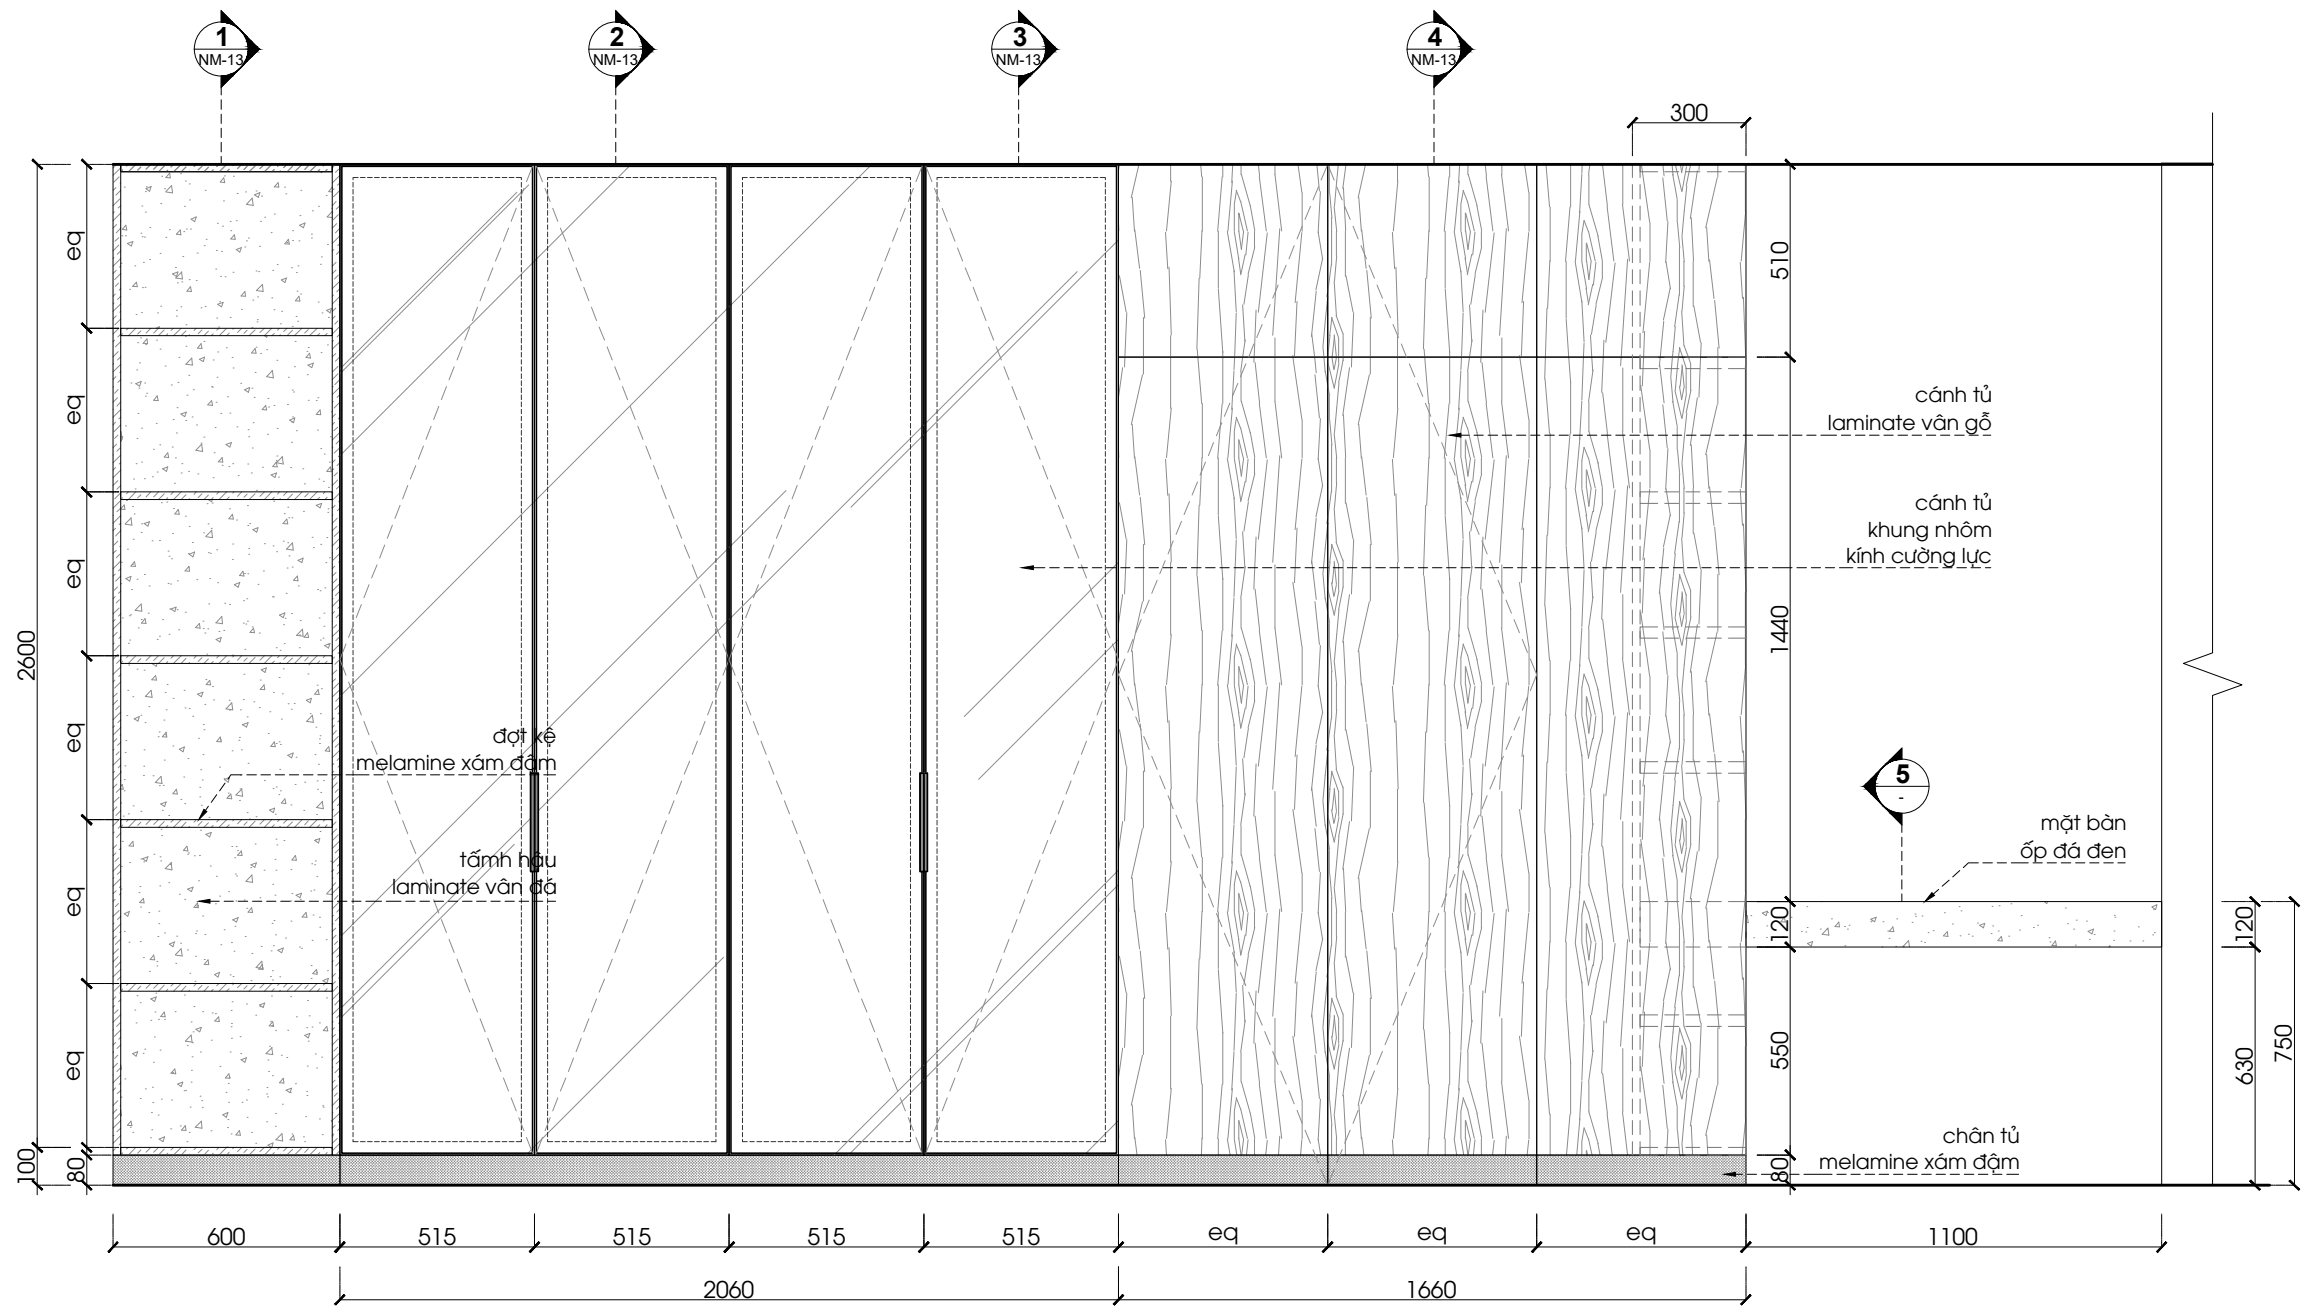


MẶT ĐỨNG PM-08,09,10
1:20 @A3

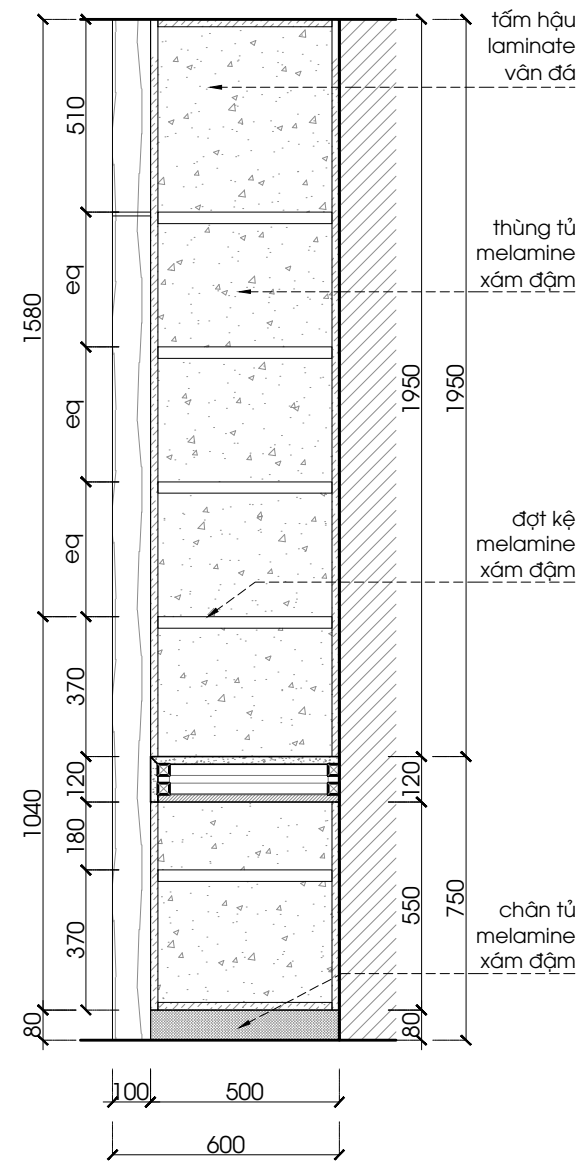


MẶT CẮT 5
1:20 @A3

PHÁT HÀNH		HIỆU CHỈNH		GHI CHÚ - MỌI KÍCH THƯỚC CẦN ĐƯỢC KIỂM TRA THEO THỰC TẾ CÔNG TRƯỜNG	ARCHITECTURAL DESIGN — THIẾT KẾ KIẾN TRÚC CÔNG TY TNHH KIẾN TRÚC VIỆT VACO DESIGN LẦU 1, 38b PHAN VĂN ĐẠT - P. BẾN NGHÉ - Q.1 - TP. HCM TEL: +84-9-36223364 EMAIL: info@vacodesign.com	DESIGNER - CHỦ TRÌ THIẾT KẾ ThS.KTS. ĐỖ QUỐC HIỆP	PROJECT TITLE - TÊN DỰ ÁN CĂN HỘ 08.03- 08.04-08.05-08.06	DATE - NGÀY 03 - 2025	
								SCALE - TỈ LỆ 1:20	
								DRAWING NO. - SỐ HIỆU BẢN VẼ NM-11	KÝ HIỆU BẢNG VẼ N
					ThS.KTS. ĐỖ QUỐC HIỆP	KTS. TRẦN TRUNG KIẾN	DRAWING TITLE - TÊN BẢN VẼ CHI TIẾT PM-08		

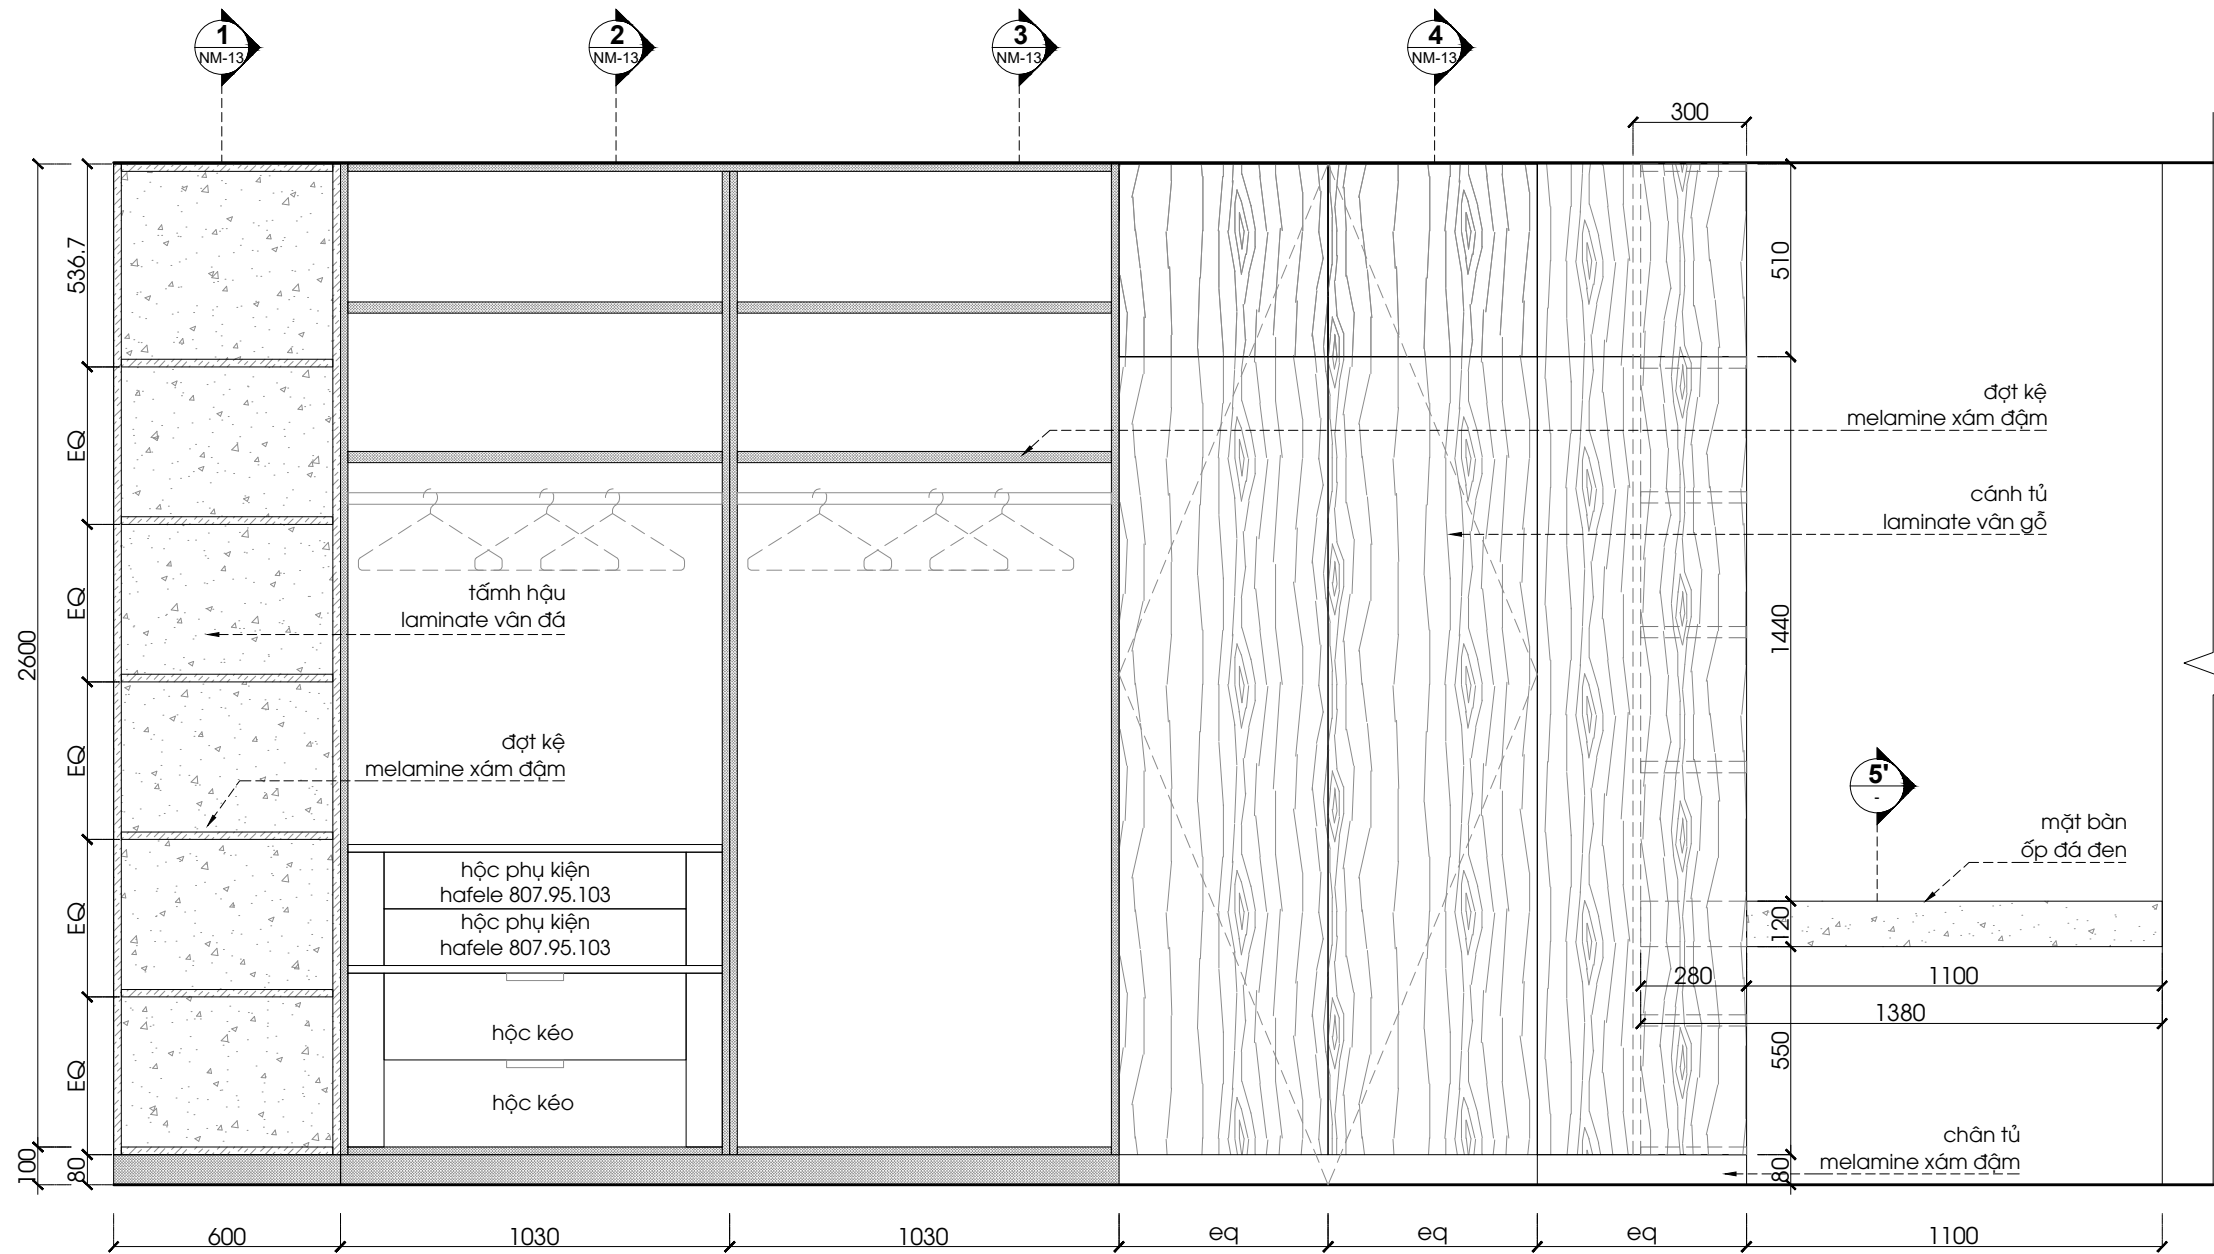


MẶT ĐỪNG PM-08,09,10
1:20 @A3

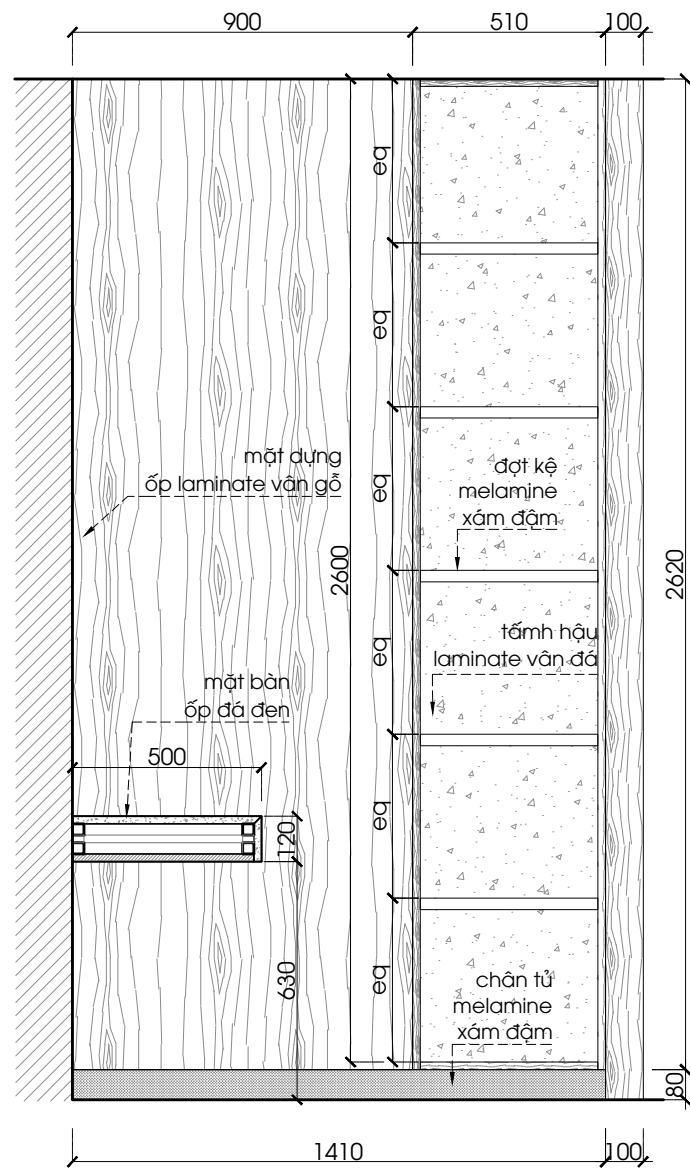


MẶT CẮT 5'
1:20 @A3


PHÁT HÀNH		HIỆU CHÍNH		GHI CHÚ	ARCHITECTURAL DESIGN — THIẾT KẾ KIẾN TRÚC  CÔNG TY TNHH KIẾN TRÚC VIỆT VACO DESIGN LẦU 1, 38b PHAN VĂN ĐẠT - P. BẾN NGHÉ - Q.1 - TP. HCM TEL: +84-9-36223364 EMAIL: info@vacodesign.com	DESIGNER - CHỦ TRÌ THIẾT KẾ	PROJECT TITLE - TÊN DỰ ÁN	DATE - NGÀY		
								03 - 2025		
								SCALE - TỈ LỆ		
								1:20		
								DRAWING TITLE - TÊN BẢN VẼ	DRAWING NO. - SỐ HIỆU BẢN VẼ	KÝ HIỆU BẢNG VẼ
				ThS.KTS. ĐỖ QUỐC HIỆP	KTS. TRẦN TRUNG KIẾN					

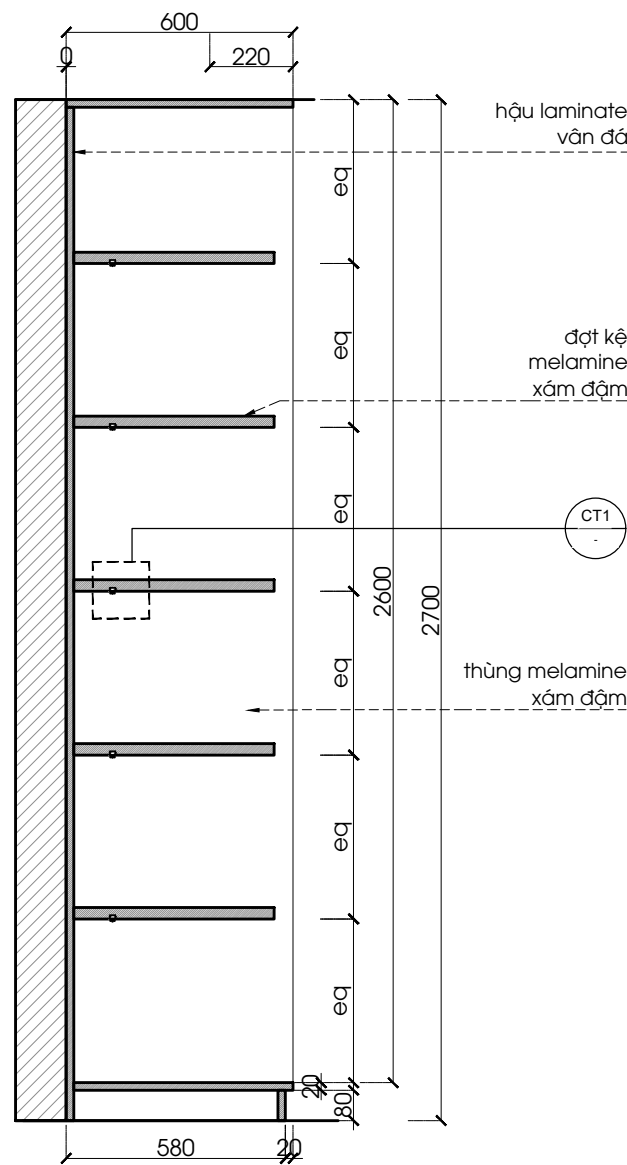


MẶT CẮT 1
1:20 @A3

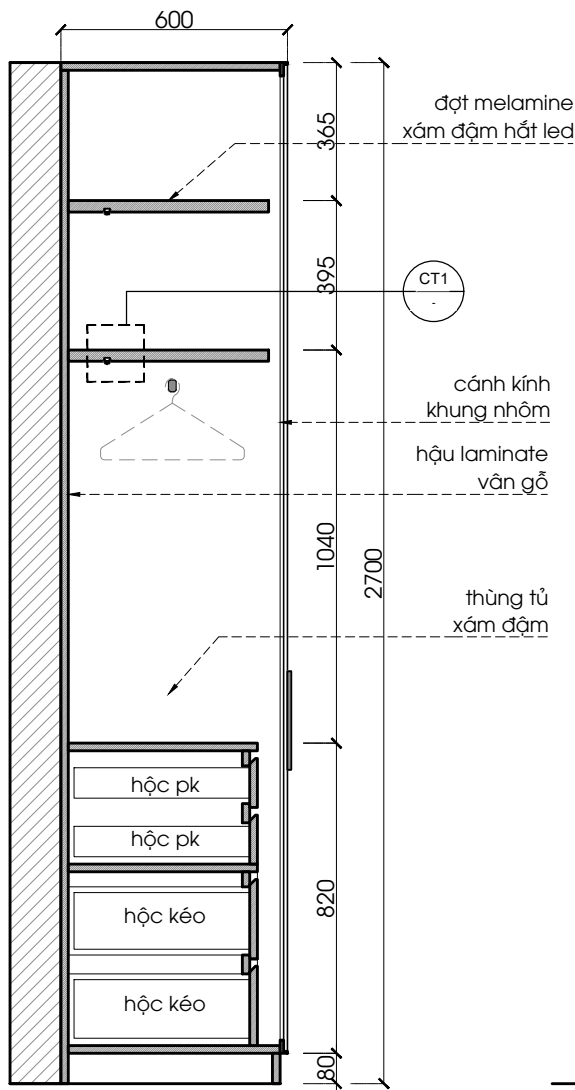


MẶT CẮT 2
1:20 @A3

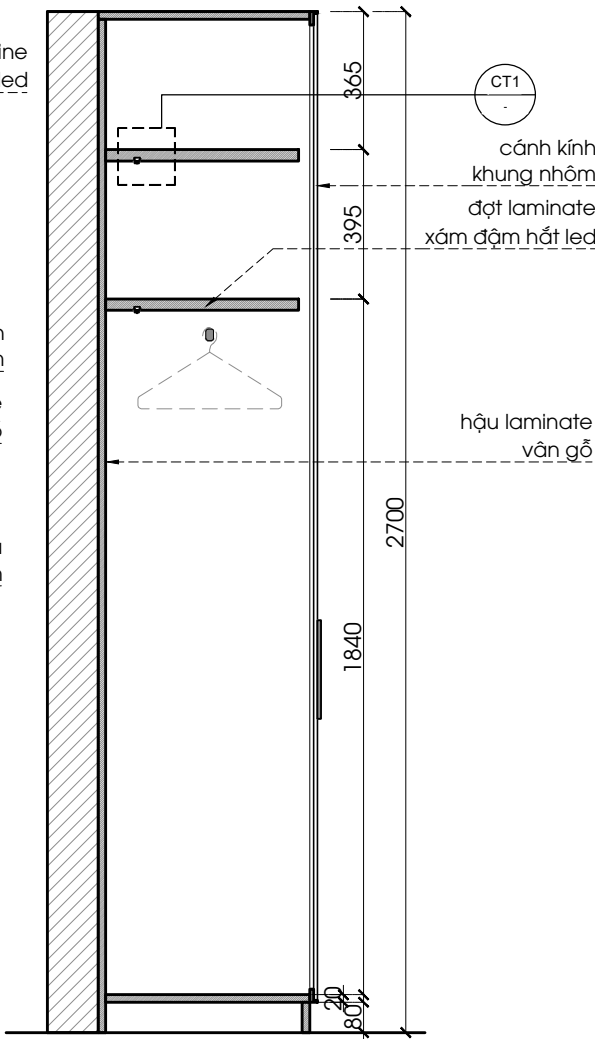

MẶT CẮT 3
1:20 @A3

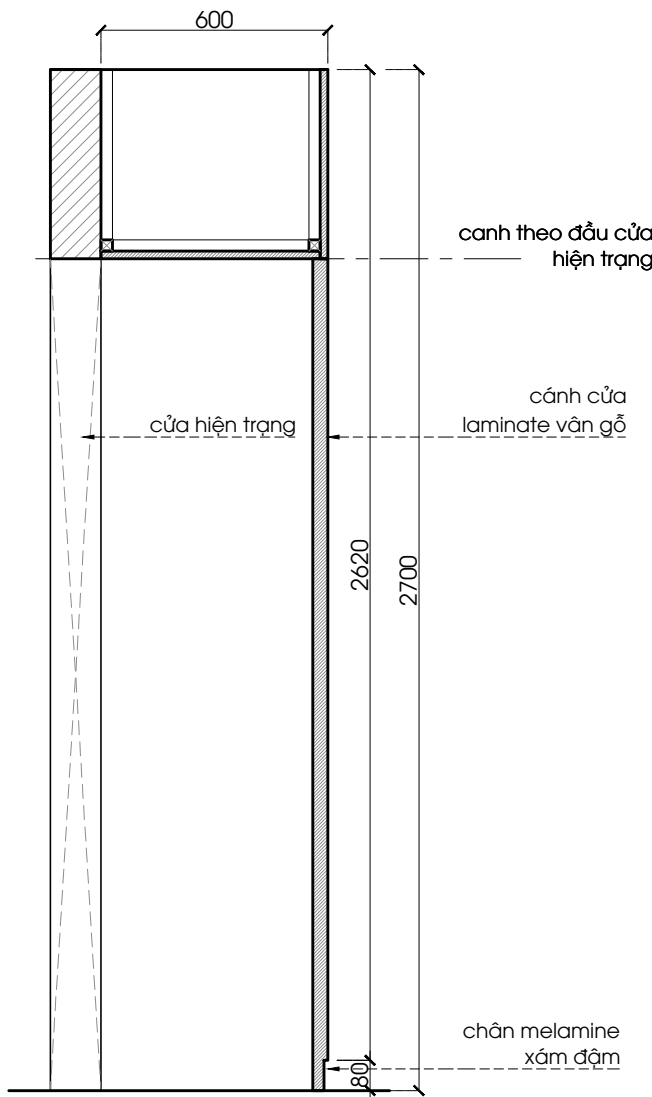


MẶT CẮT 4
1:20 @A3

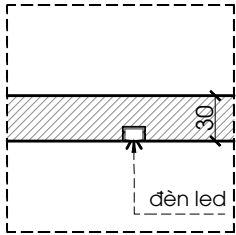


CHI TIẾT 1

PHÁT HÀNH		HIỆU CHÍNH		GHI CHÚ	ARCHITECTURAL DESIGN — THIẾT KẾ KIẾN TRÚC		DESIGNER - CHỦ TRÌ THIẾT KẾ		PROJECT TITLE - TÊN DỰ ÁN		DATE - NGÀY	
					- MỌI KÍCH THƯỚC CẦN ĐƯỢC KIỂM TRA THEO THỰC TẾ CÔNG TRƯỜNG	CÔNG TY TNHH KIẾN TRÚC VIỆT VACO DESIGN LẦU 1, 3bis PHAN VĂN ĐẠT - P. BẾN NGHÉ - Q.1 - TP. HCM TEL: +84-9-36223384 EMAIL: info@vacodesign.com	ThS.KTS. ĐỖ QUỐC HIỆP	CĂN HỘ 08.03- 08.04-08.05-08.06	03 - 2025	SCALE - TỈ LỆ 1:20		
				DIRECTOR - GIÁM ĐỐC	DRAWN BY - NGƯỜI VẼ		DRAWING TITLE - TÊN BẢN VẼ		DRAWING NO. - SỐ HIỆU BẢN VẼ	KÝ HIỆU BẢNG VẼ		
				ThS.KTS. ĐỖ QUỐC HIỆP	KTS. TRẦN TRUNG KIẾN		CHI TIẾT PM-08,09,10		NM-13	N		

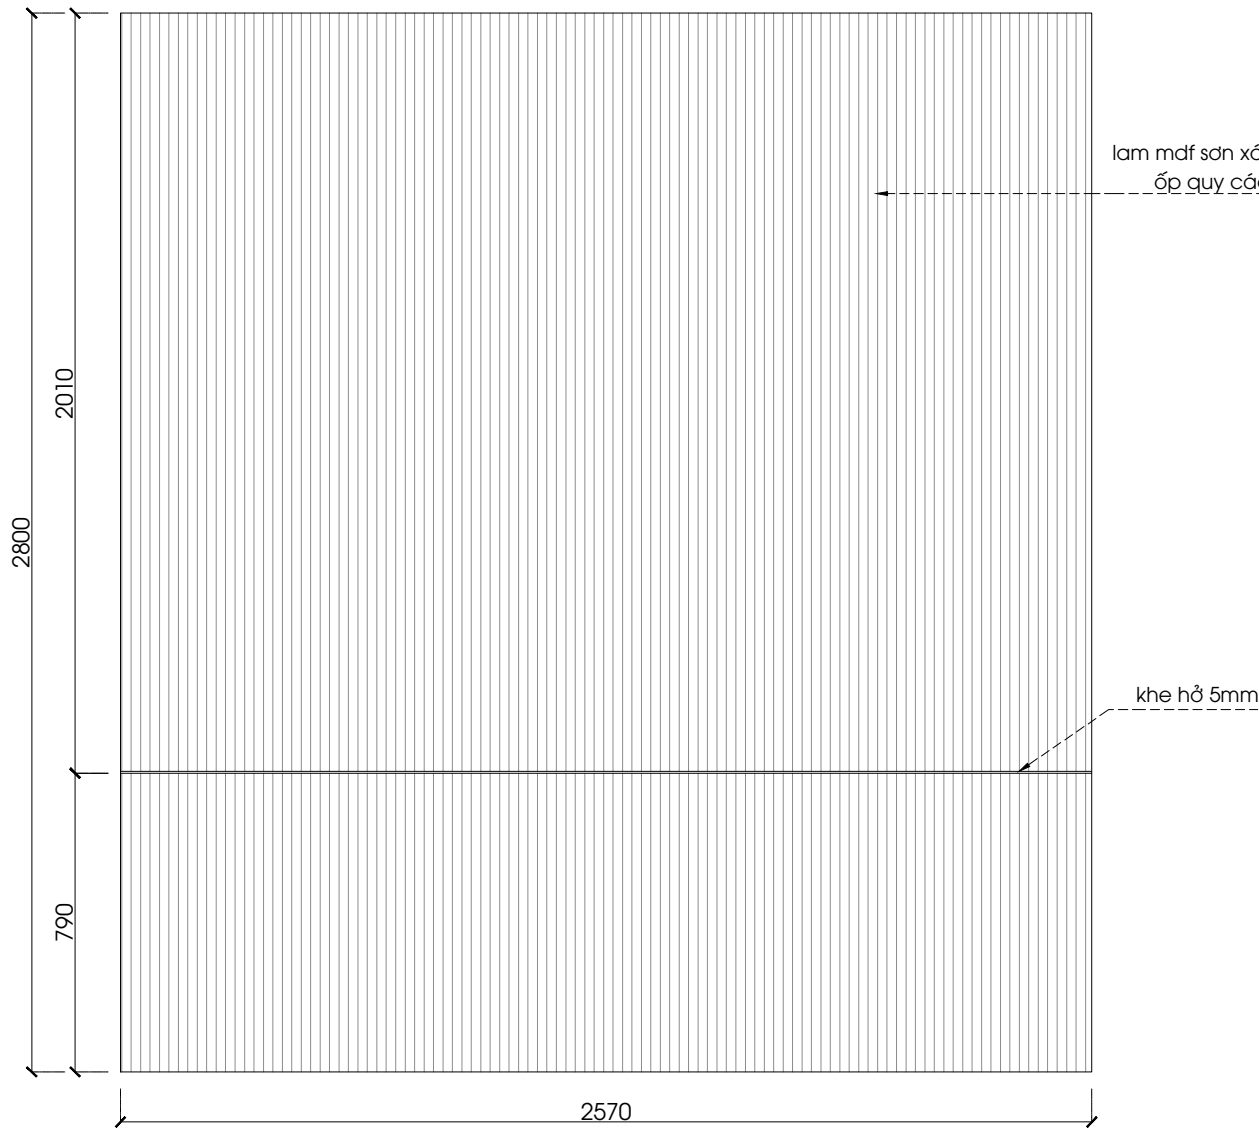


MẶT ĐỨNG 1 PM-02
1:20 @A3

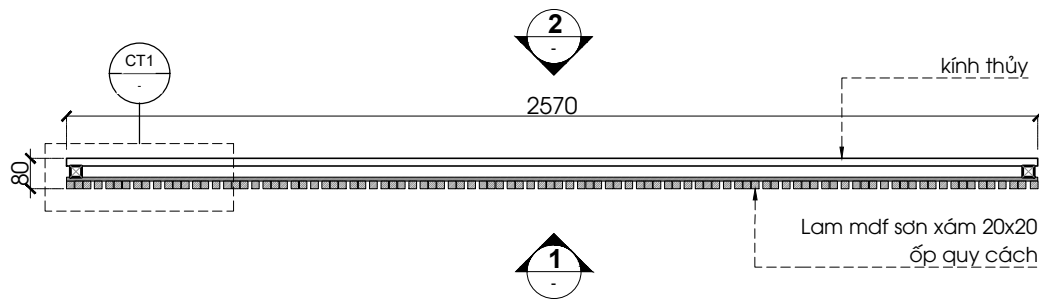

MẶT BẰNG PM-02
1:20 @A3




MẶT ĐỨNG 2 PM-02
1:20 @A3

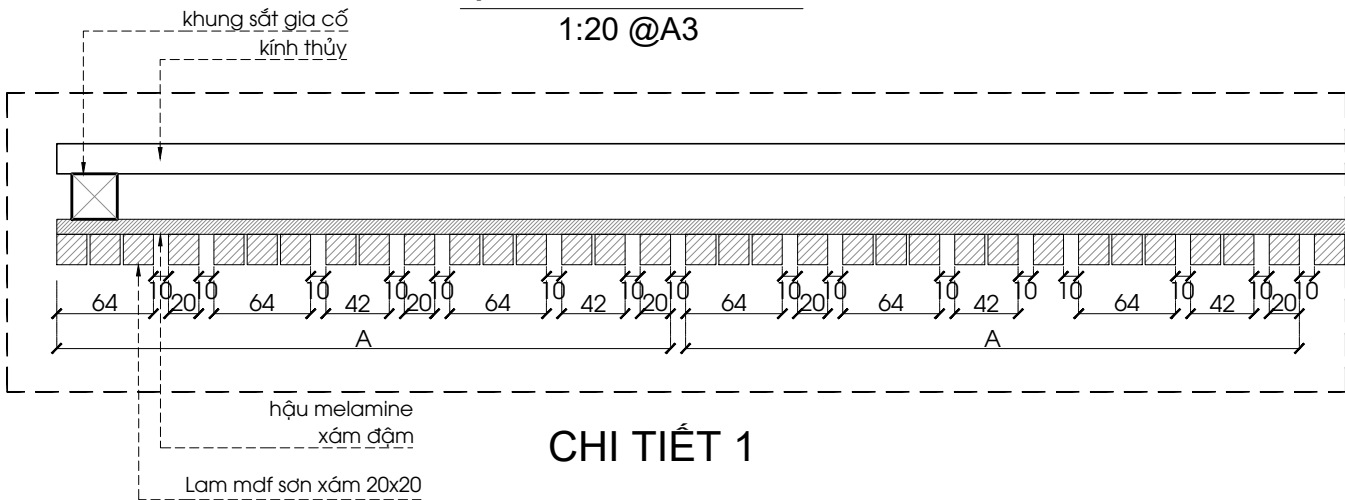


CHI TIẾT 1

PHÁT HÀNH		HIỆU CHỈNH		GHI CHÚ	ARCHITECTURAL DESIGN — THIẾT KẾ KIẾN TRÚC		DESIGNER - CHỦ TRÌ THIẾT KẾ		PROJECT TITLE - TÊN DỰ ÁN		DATE - NGÀY	
					CÔNG TY TNHH KIẾN TRÚC VIỆT VACO DESIGN LẦU 1, 3bis PHAN VĂN ĐẠT - P. BẾN NGHÉ - Q.1 - TP. HCM TEL: +84-9-36223364 EMAIL: info@vacodesign.com		ThS.KTS. ĐỖ QUỐC HIỆP		CĂN HỘ 08.03- 08.04-08.05-08.06		03 - 2025	
											SCALE - TỈ LỆ	
											1:20	
											DRAWING NO. - SỐ HIỆU BẢN VẼ	
											NM-14	
											KỶ HIỆU BẢNG VẼ	
				MỌI KÍCH THƯỚC CẦN ĐƯỢC KIỂM TRA THEO THỰC TẾ CÔNG TRƯỜNG		ThS.KTS. ĐỖ QUỐC HIỆP	KTS. TRẦN TRUNG KIẾN		CHI TIẾT PM-02		N	

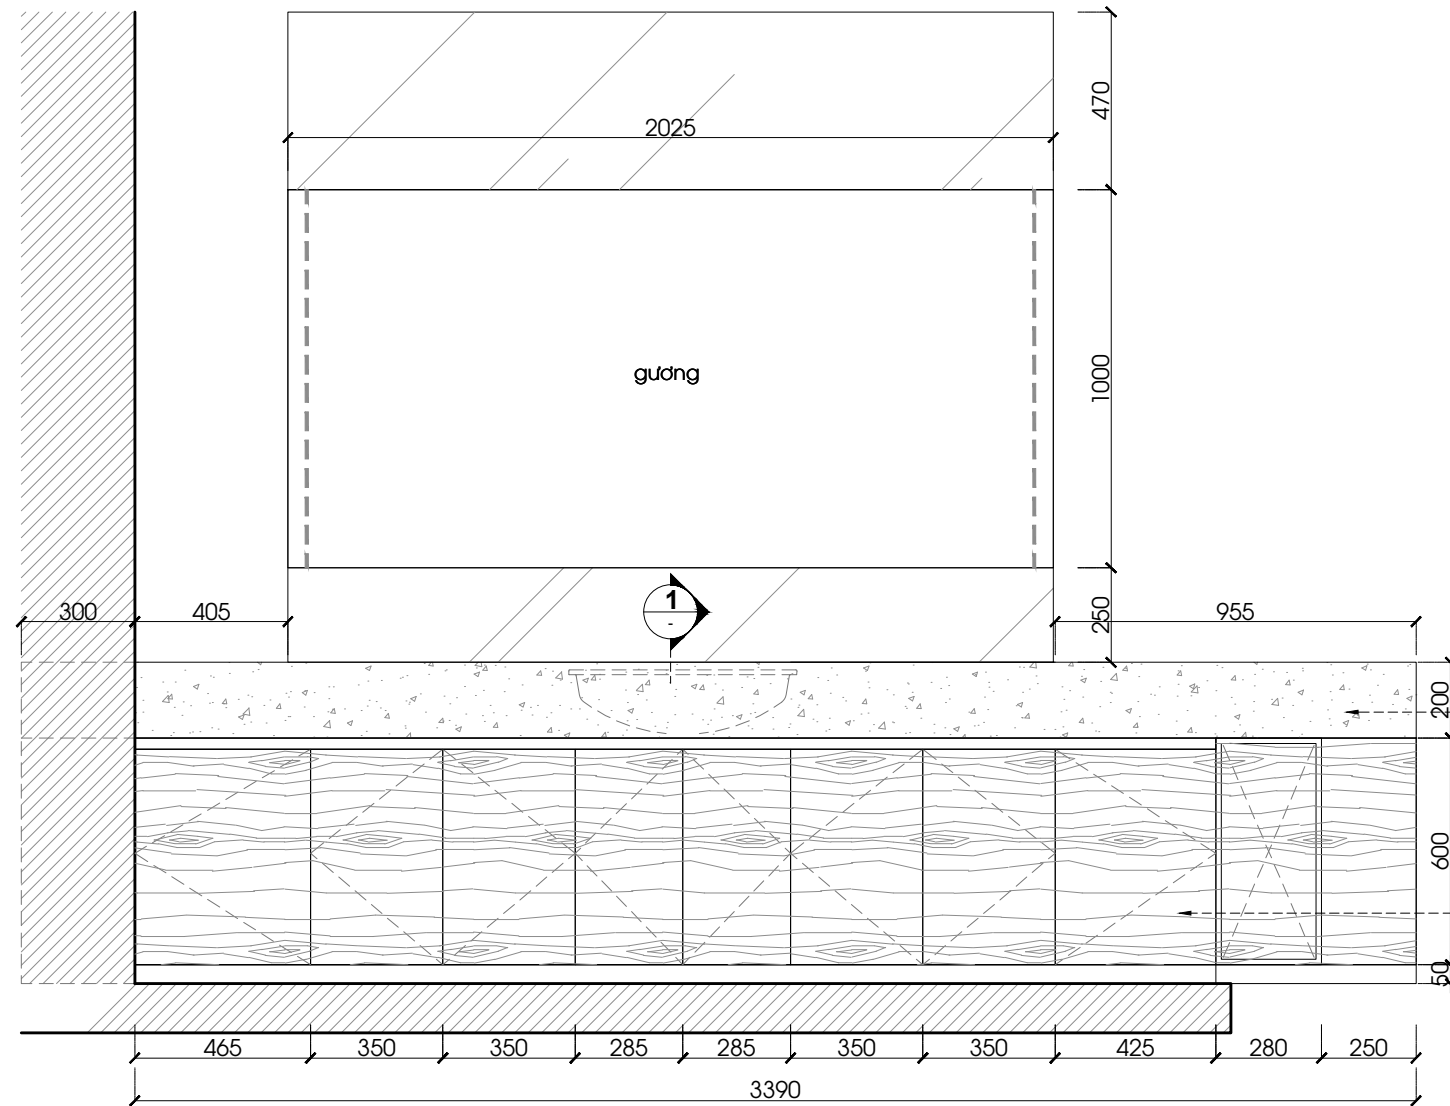


MẶT ĐỪNG 1 PM-12

1:20 @A3

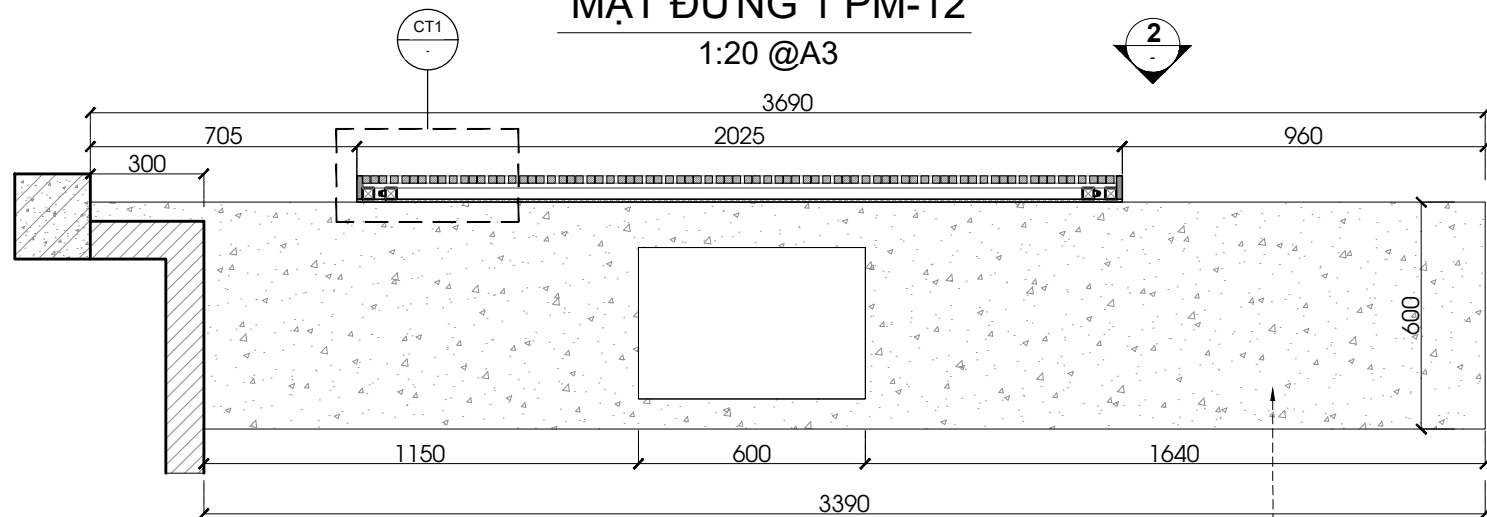


MẶT BẰNG PM-12

1:20 @A3

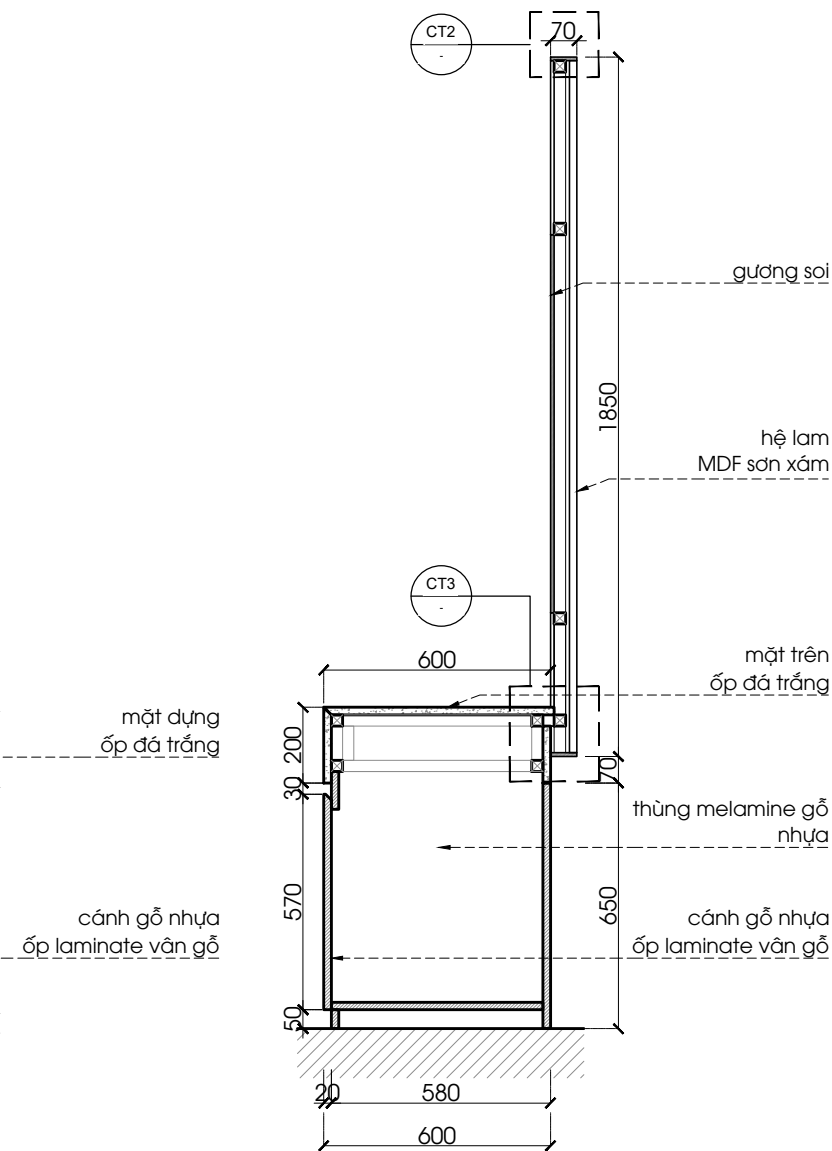


MẶT CẮT 1


1:20 @A3

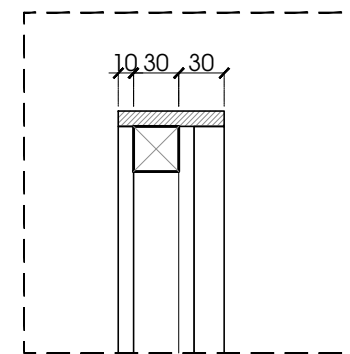

CHI TIẾT 2

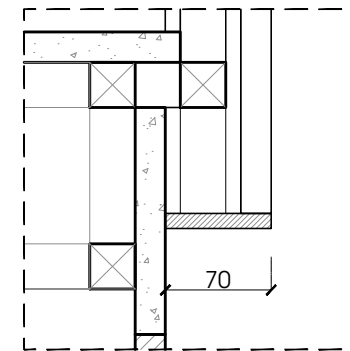


CHI TIẾT 3

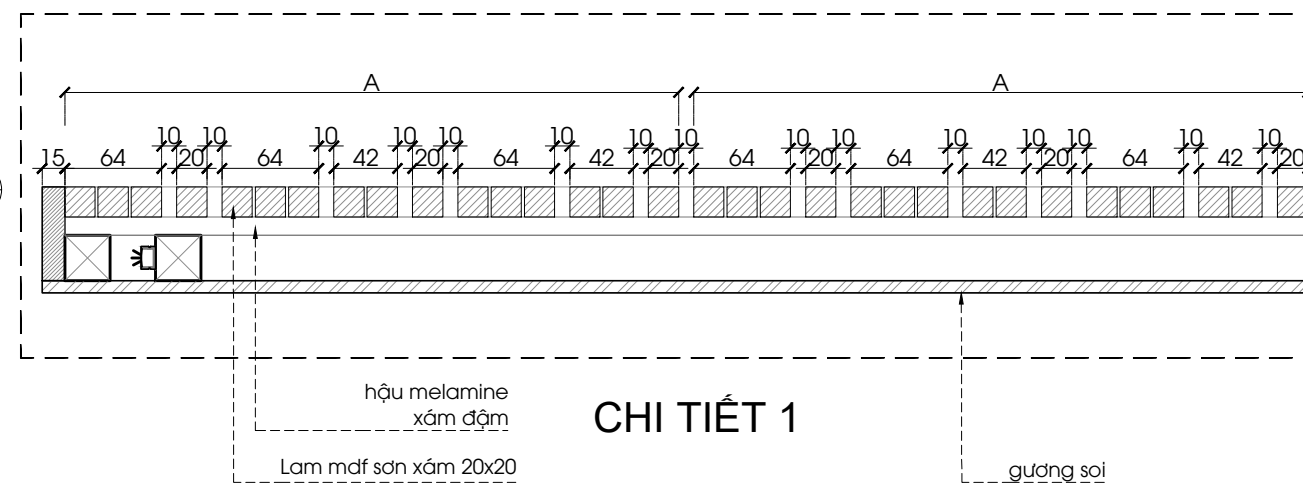


CHI TIẾT 1


PHÁT HÀNH		HIỆU CHỈNH		GHI CHÚ		ARCHITECTURAL DESIGN — THIẾT KẾ KIẾN TRÚC		DESIGNER - CHỦ TRÌ THIẾT KẾ		PROJECT TITLE - TÊN DỰ ÁN		DATE - NGÀY	
				- MỌI KÍCH THƯỚC CẦN ĐƯỢC KIỂM TRA THEO THỰC TẾ CÔNG TRƯỜNG		CÔNG TY TNHH KIẾN TRÚC VIỆT		ThS.KTS. ĐỖ QUỐC HIỆP		CĂN HỘ 08.03- 08.04-08.05-08.06		03 - 2025	
						VACO DESIGN						SCALE - TỈ LỆ	
						LẦU 1, 3bis PHAN VĂN ĐẠT - P. BẾN NGHÉ - Q.1 - TP. HCM		DRAWN BY - NGƯỜI VẼ		DRAWING TITLE - TÊN BẢN VẼ		DRAWING NO. - SỐ HIỆU BẢN VẼ	
						TEL: +84-9-36233384		KTS. TRẦN TRUNG KIẾN		CHI TIẾT PM-12		NM-15	
						EMAIL: info@vacodesign.com						KÝ HIỆU BẢN VẼ	
												N	

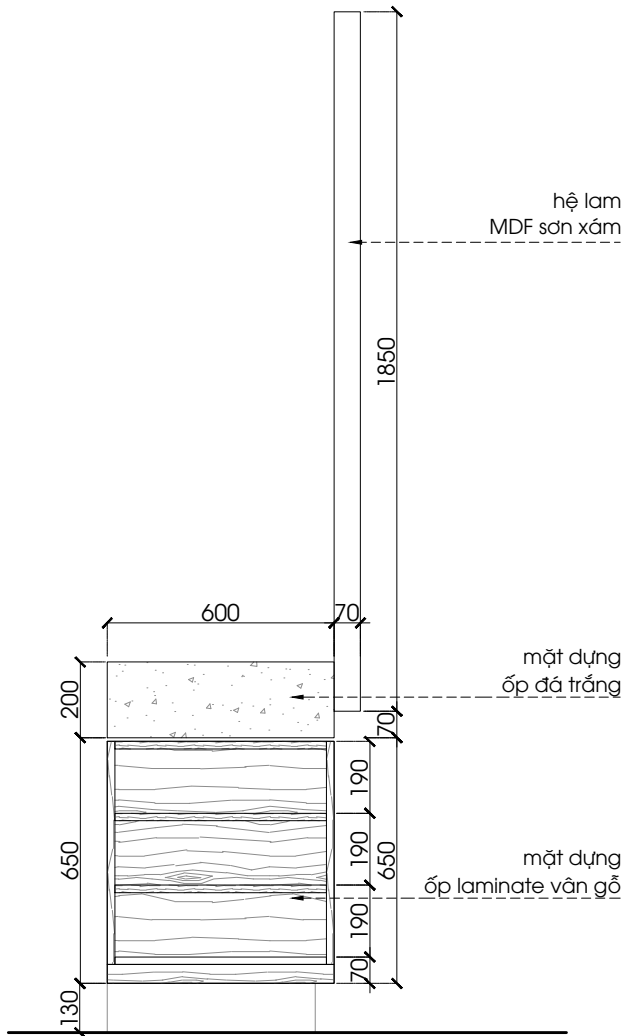

MẶT ĐỨNG 2 PM-12
1:20 @A3

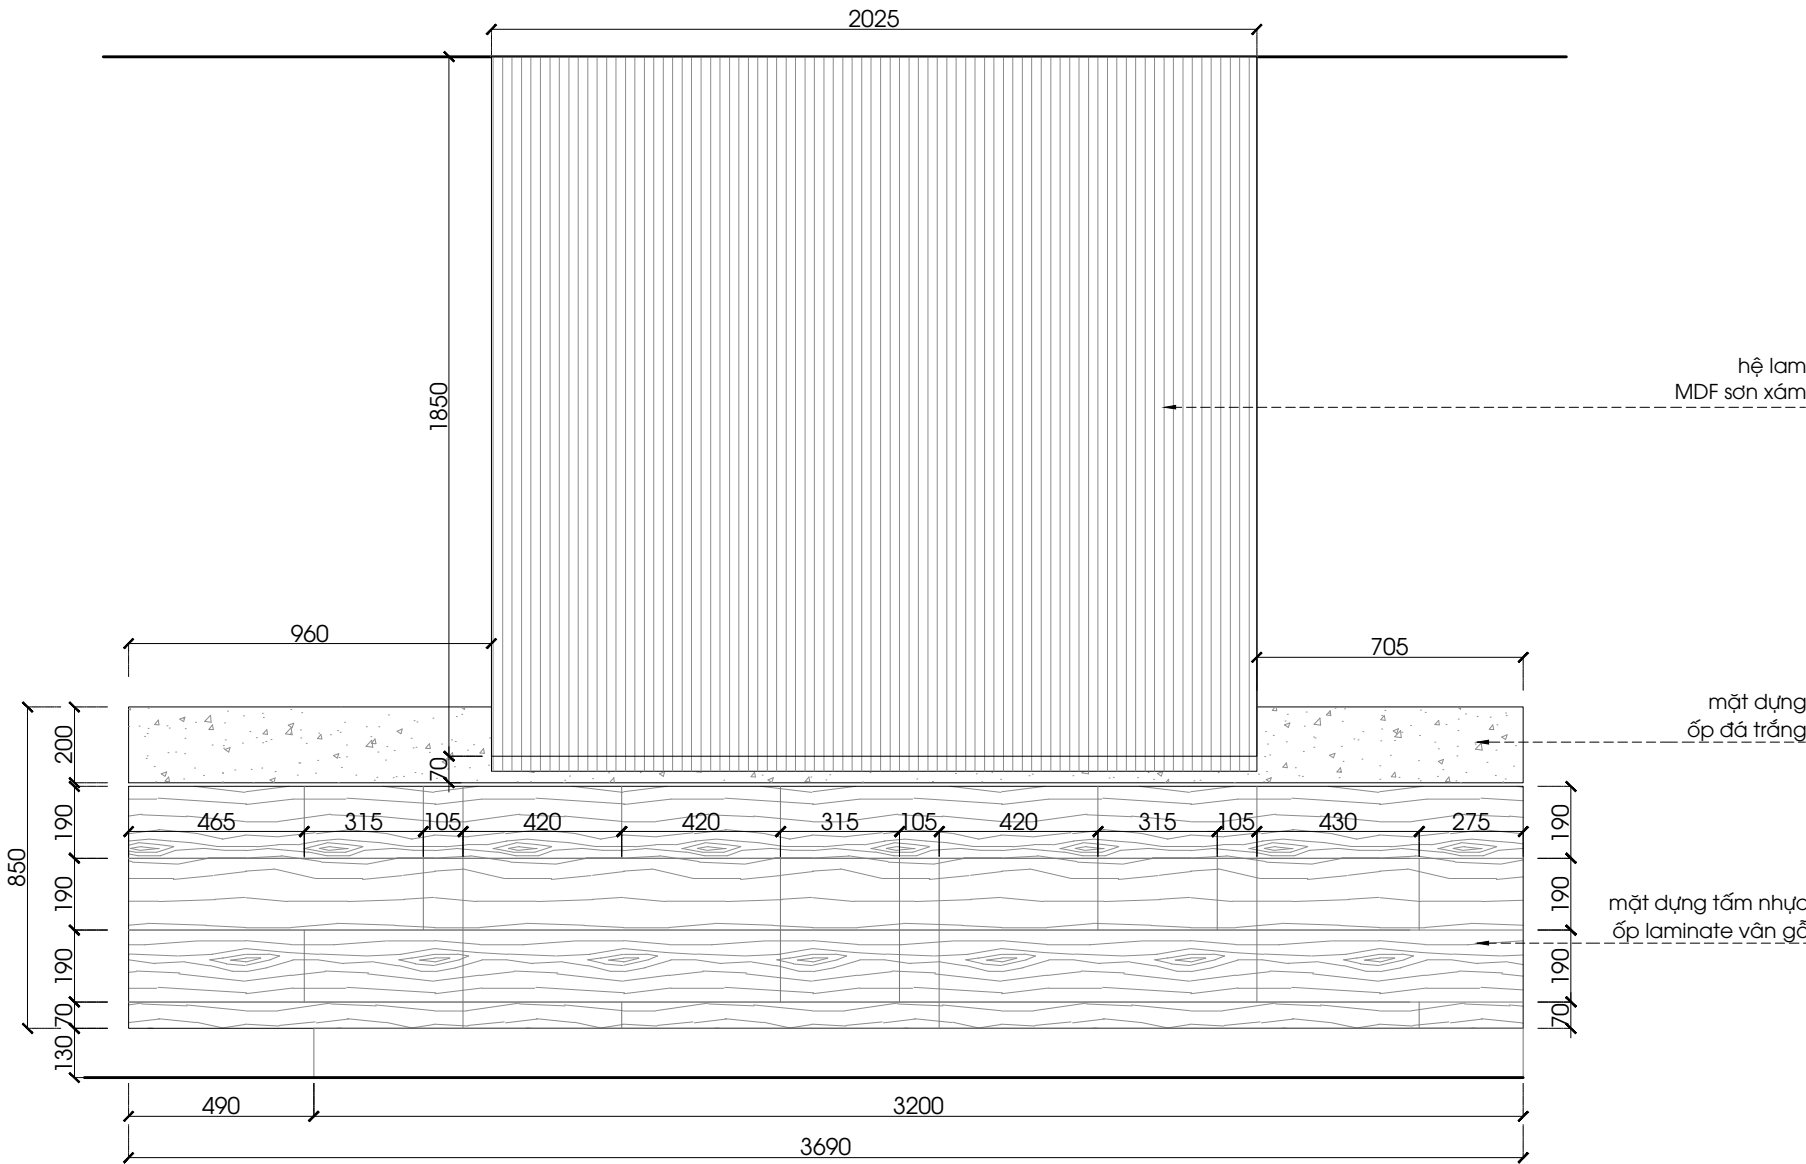


MẶT ĐỨNG 3 PM-12
1:20 @A3

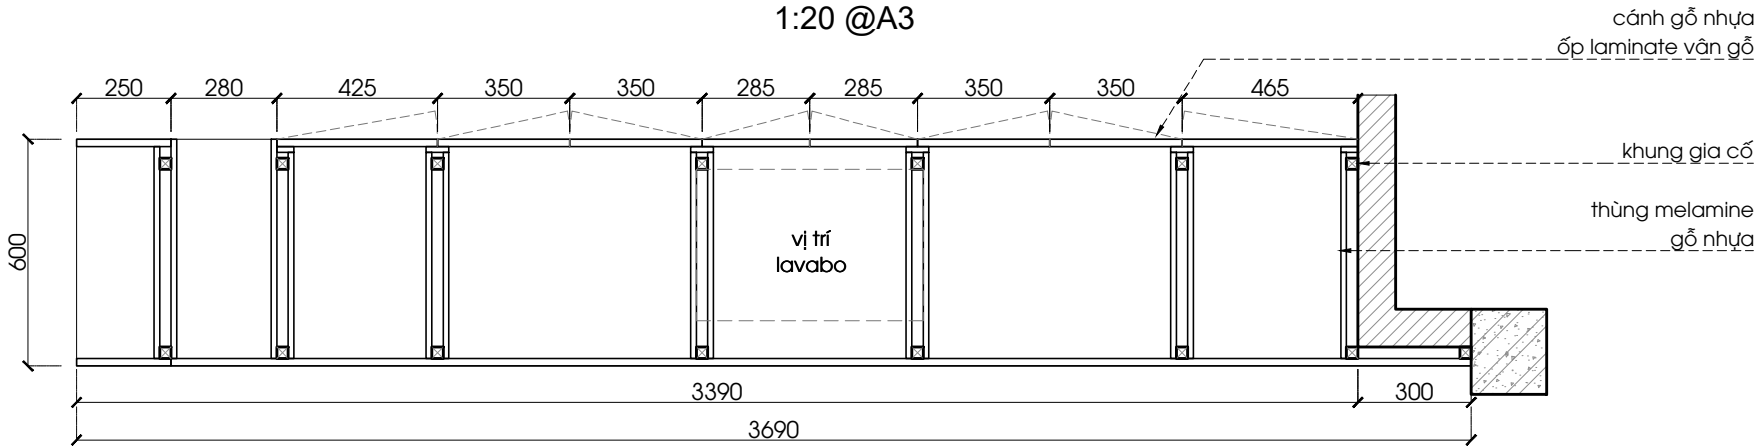



MẶT BẰNG THÙNG TỦ PM-12
1:20 @A3

PHÁT HÀNH		HIỆU CHÍNH		GHI CHÚ - MỌI KÍCH THƯỚC CẦN ĐƯỢC KIỂM TRA THEO THỰC TẾ CÔNG TRƯỜNG	ARCHITECTURAL DESIGN — THIẾT KẾ KIẾN TRÚC CÔNG TY TNHH KIẾN TRÚC VIỆT VACO DESIGN LẦU 1, 3bis PHAN VĂN ĐẠT - P. BẾN NGHÉ - Q.1 - TP. HCM TEL: +84-9-36223364 EMAIL: info@vacodesign.com DESIGN DIRECTOR - GIÁM ĐỐC ThS.KTS. ĐỖ QUỐC HIỆP	DESIGNER - CHỦ TRÌ THIẾT KẾ ThS.KTS. ĐỖ QUỐC HIỆP DRAWN BY - NGƯỜI VẼ KTS. TRẦN TRUNG KIẾN	PROJECT TITLE - TÊN DỰ ÁN		DATE - NGÀY	
							03 - 2025			
							SCALE - TỈ LỆ			
							1:20			
							DRAWING TITLE - TÊN BẢN VẼ			
							CHI TIẾT PM-12			
							DRAWING NO. - SỐ HIỆU BẢN VẼ	KÝ HIỆU BẢNG VẼ		
							NM-16	N		

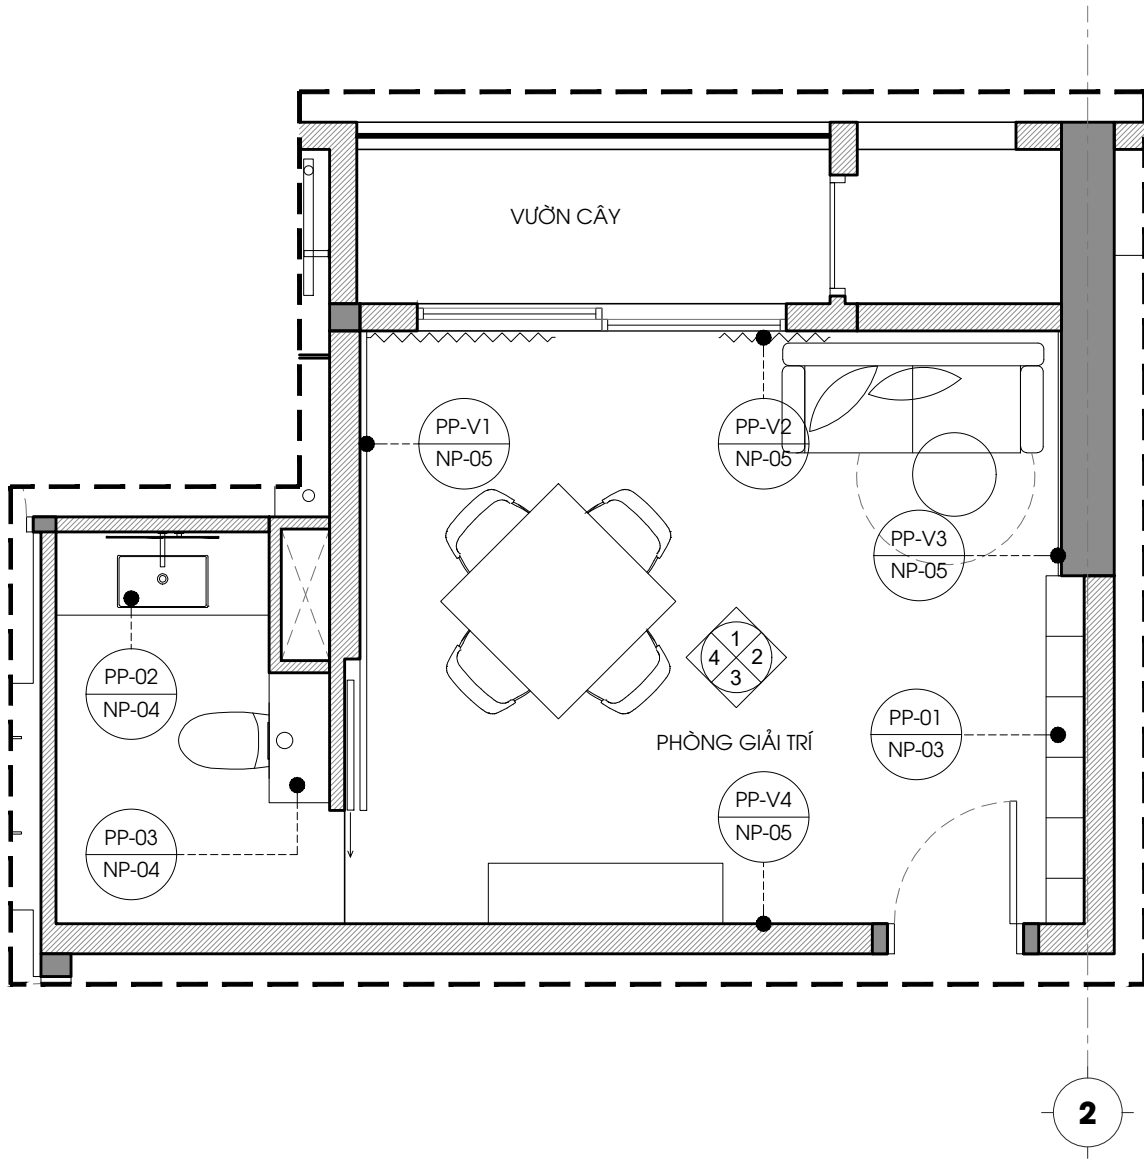


- PP1-V1** VÁCH ỐP
- LAMINATE VÂN GỖ
- PP1-V2** VÁCH ỐP
- LAMINATE VÂN GỖ
- PP1-V3** VÁCH ỐP
- LAMINATE VÂN GỖ
- PP1-V4** VÁCH ỐP
- LAMINATE VÂN GỖ
- PP-01** TỦ TRANG TRÍ
- KHUNG SẮT
- HẬU LAMINATE GIẢ ĐÁ
- ĐỢT KỆ GỖ VENEER WALNUT
- PP-02** TỦ LAVABO
- THÙNG MELAMINE GỖ NHỰA
- CÁCH GỖ NHỰA LAMINATE VÂN VẢI
- PP-03** TỦ TRANG TRÍ WC
- THÙNG GỖ NHỰA
- CÁCH NHỰA BỌC LAMINATE MÀU XẮM ĐẬM

 
PHÁT HÀNH		HIỆU CHỈNH		GHI CHÚ - MỌI KÍCH THƯỚC CẦN ĐƯỢC KIỂM TRA THEO THỰC TẾ CÔNG TRƯỜNG	ARCHITECTURAL DESIGN — THIẾT KẾ KIẾN TRÚC  CÔNG TY TNHH KIẾN TRÚC VIỆT VACO DESIGN LẦU 1, 38/6 PHAN VĂN ĐẠT - P. BẾN NGHÉ - Q.1 - TP. HCM TEL: +84-9-36223364 EMAIL: info@vacodesign.com		DESIGNER - CHỦ TRÌ THIẾT KẾ		PROJECT TITLE - TÊN DỰ ÁN		DATE - NGÀY 03 - 2025	
					ThS.KTS. ĐỖ QUỐC HIỆP <td colspan="2">CĂN HỘ 08.03- 08.04-08.05-08.06<td colspan="2">SCALE - TỈ LỆ 1:50</td></td>		CĂN HỘ 08.03- 08.04-08.05-08.06 <td colspan="2">SCALE - TỈ LỆ 1:50</td>		SCALE - TỈ LỆ 1:50			
					DIRECTOR - GIÁM ĐỐC <td colspan="2">DRAWN BY - NGƯỜI VẼ<td colspan="2">DRAWING TITLE - TÊN BẢN VẼ<td colspan="1">DRAWING NO. - SỐ HIỆU BẢN VẼ</td><td colspan="1">KÝ HIỆU BẢNG VẼ</td></td></td>		DRAWN BY - NGƯỜI VẼ <td colspan="2">DRAWING TITLE - TÊN BẢN VẼ<td colspan="1">DRAWING NO. - SỐ HIỆU BẢN VẼ</td><td colspan="1">KÝ HIỆU BẢNG VẼ</td></td>		DRAWING TITLE - TÊN BẢN VẼ <td colspan="1">DRAWING NO. - SỐ HIỆU BẢN VẼ</td> <td colspan="1">KÝ HIỆU BẢNG VẼ</td>		DRAWING NO. - SỐ HIỆU BẢN VẼ	KÝ HIỆU BẢNG VẼ
					ThS.KTS. ĐỖ QUỐC HIỆP <td colspan="2">KTS. TRẦN TRUNG KIÊN<td colspan="2">MẶT BẰNG BỐ TRÍ NỘI THẤT PHÒNG POCKER<td colspan="1">NP-01</td><td colspan="1">N</td></td></td>		KTS. TRẦN TRUNG KIÊN <td colspan="2">MẶT BẰNG BỐ TRÍ NỘI THẤT PHÒNG POCKER<td colspan="1">NP-01</td><td colspan="1">N</td></td>		MẶT BẰNG BỐ TRÍ NỘI THẤT PHÒNG POCKER <td colspan="1">NP-01</td> <td colspan="1">N</td>		NP-01	N

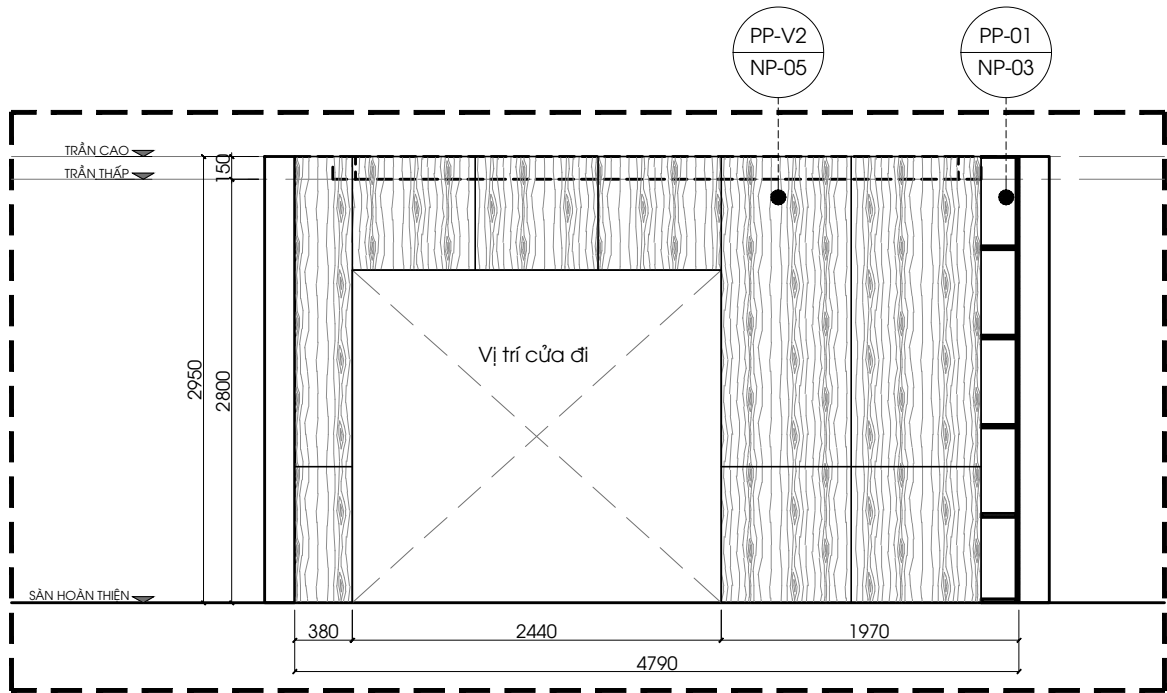


PN1 MẶT ĐỨNG 1
- 1:50 @ A3

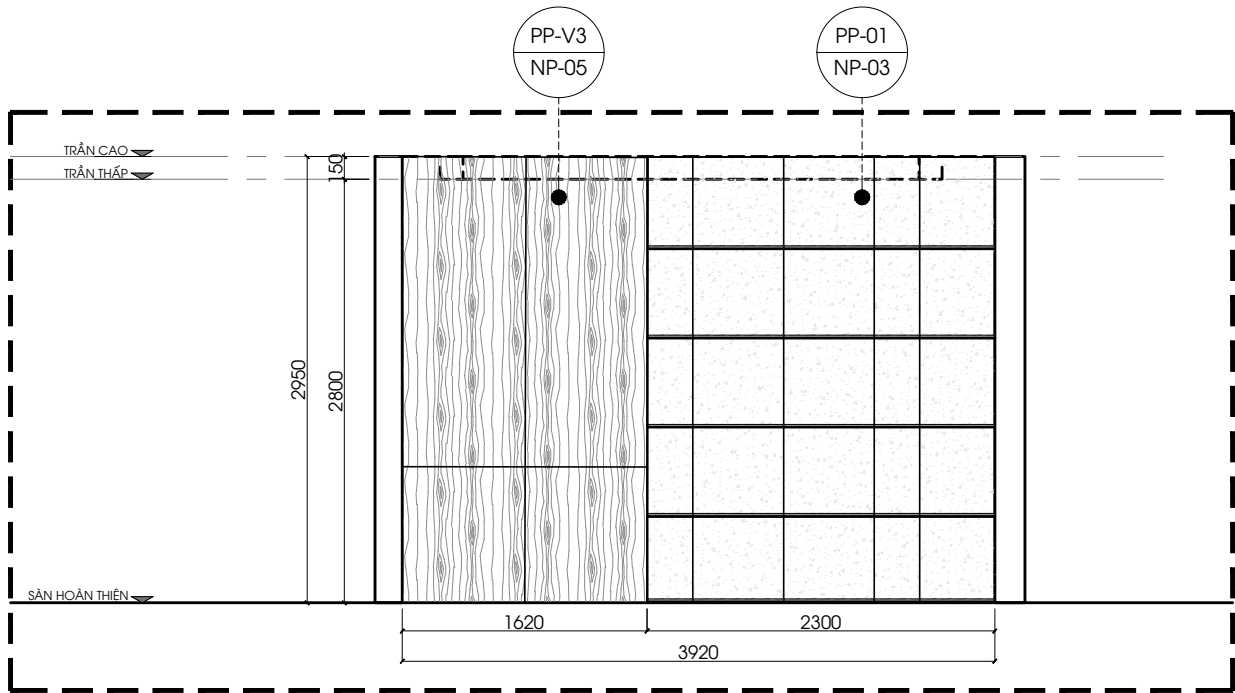

PN1 MẶT ĐỨNG 2
- 1:50 @ A3

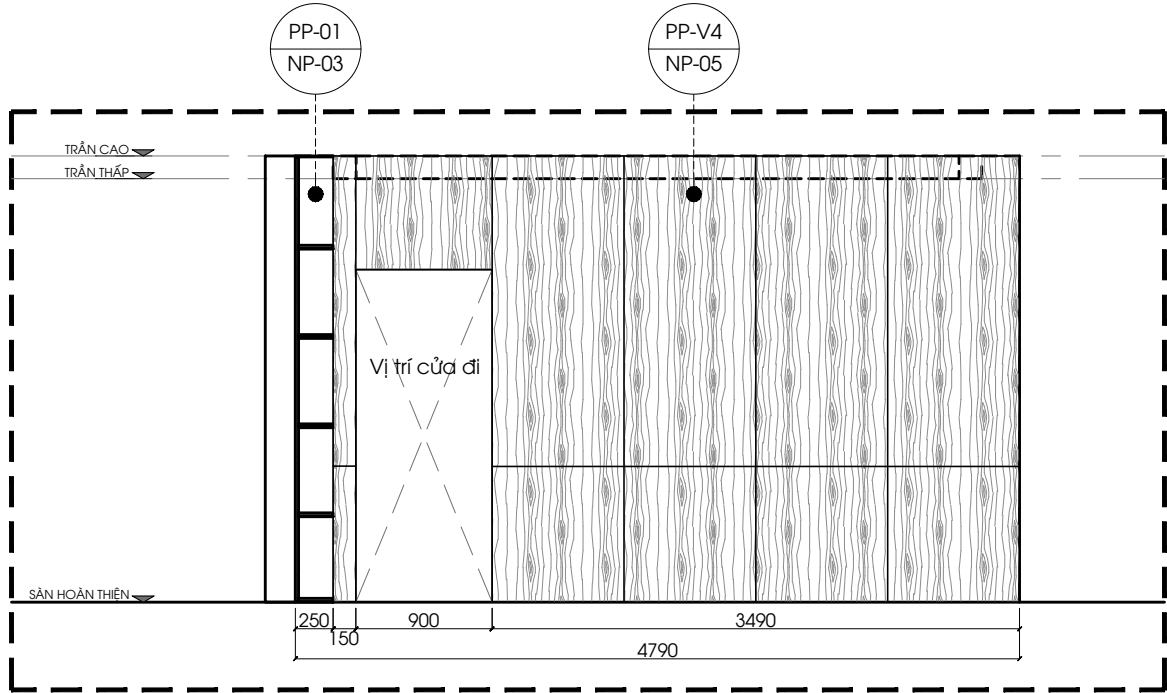


PN1 MẶT ĐỨNG 3
- 1:50 @ A3

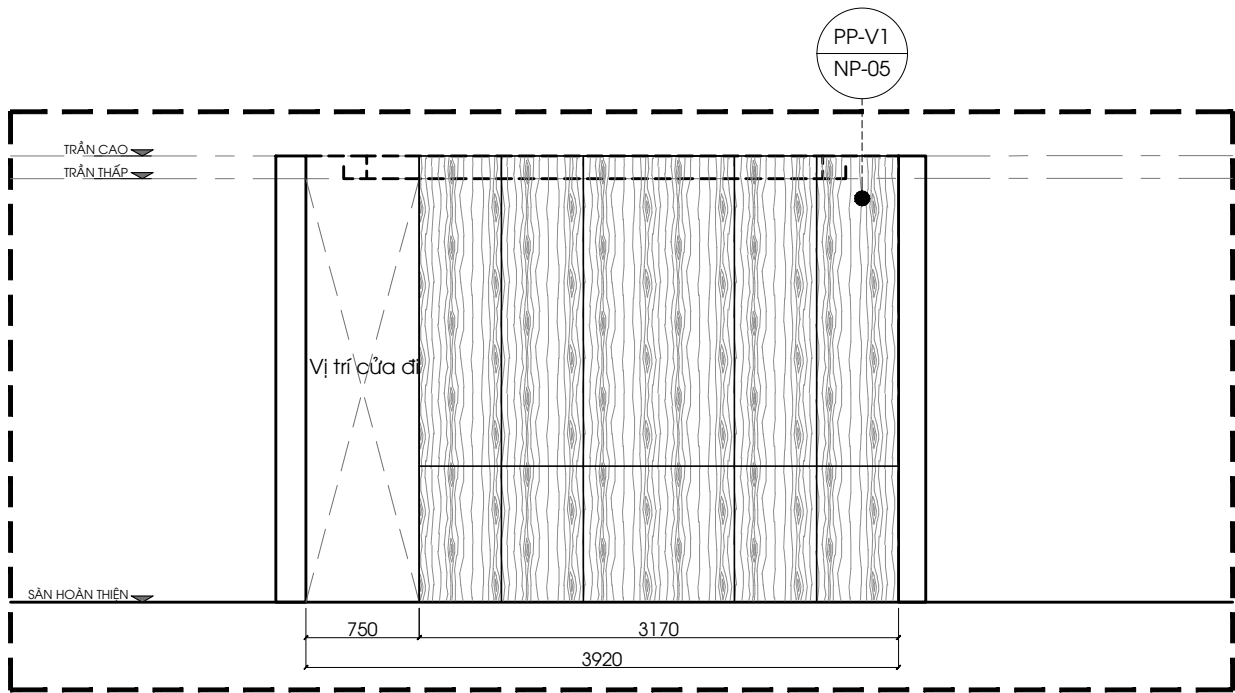

PN1 MẶT ĐỨNG 4
- 1:50 @ A3

PHÁT HÀNH		HIỆU CHÍNH		GHI CHÚ	ARCHITECTURAL DESIGN — THIẾT KẾ KIẾN TRÚC		DESIGNER - CHỦ TRÌ THIẾT KẾ	PROJECT TITLE - TÊN DỰ ÁN	DATE - NGÀY				
					- MỌI KÍCH THƯỚC CẦN ĐƯỢC KIỂM TRA THEO THỰC TẾ CÔNG TRƯỜNG	CÔNG TY TNHH KIẾN TRÚC VIỆT VACO DESIGN LẦU 1, 38b PHAN VĂN ĐẠT - P. BẾN NGHÉ - Q.1 - TP. HCM TEL: +84-9-36223384 EMAIL: info@vacodesign.com	ThS.KTS. ĐỖ QUỐC HIỆP	CĂN HỘ 08.03- 08.04-08.05-08.06	03 - 2025				
									SCALE - TỈ LỆ				
									1:50				
									DIRECTOR - GIÁM ĐỐC	DRAWN BY - NGƯỜI VẼ	DRAWING TITLE - TÊN BẢN VẼ	DRAWING NO. - SỐ HIỆU BẢN VẼ	KÝ HIỆU BẢNG VẼ
									ThS.KTS. ĐỖ QUỐC HIỆP	KTS. TRẦN TRUNG KIÊN	MẶT ĐỨNG NỘI THẤT PHÒNG POCKER	NP-02	N

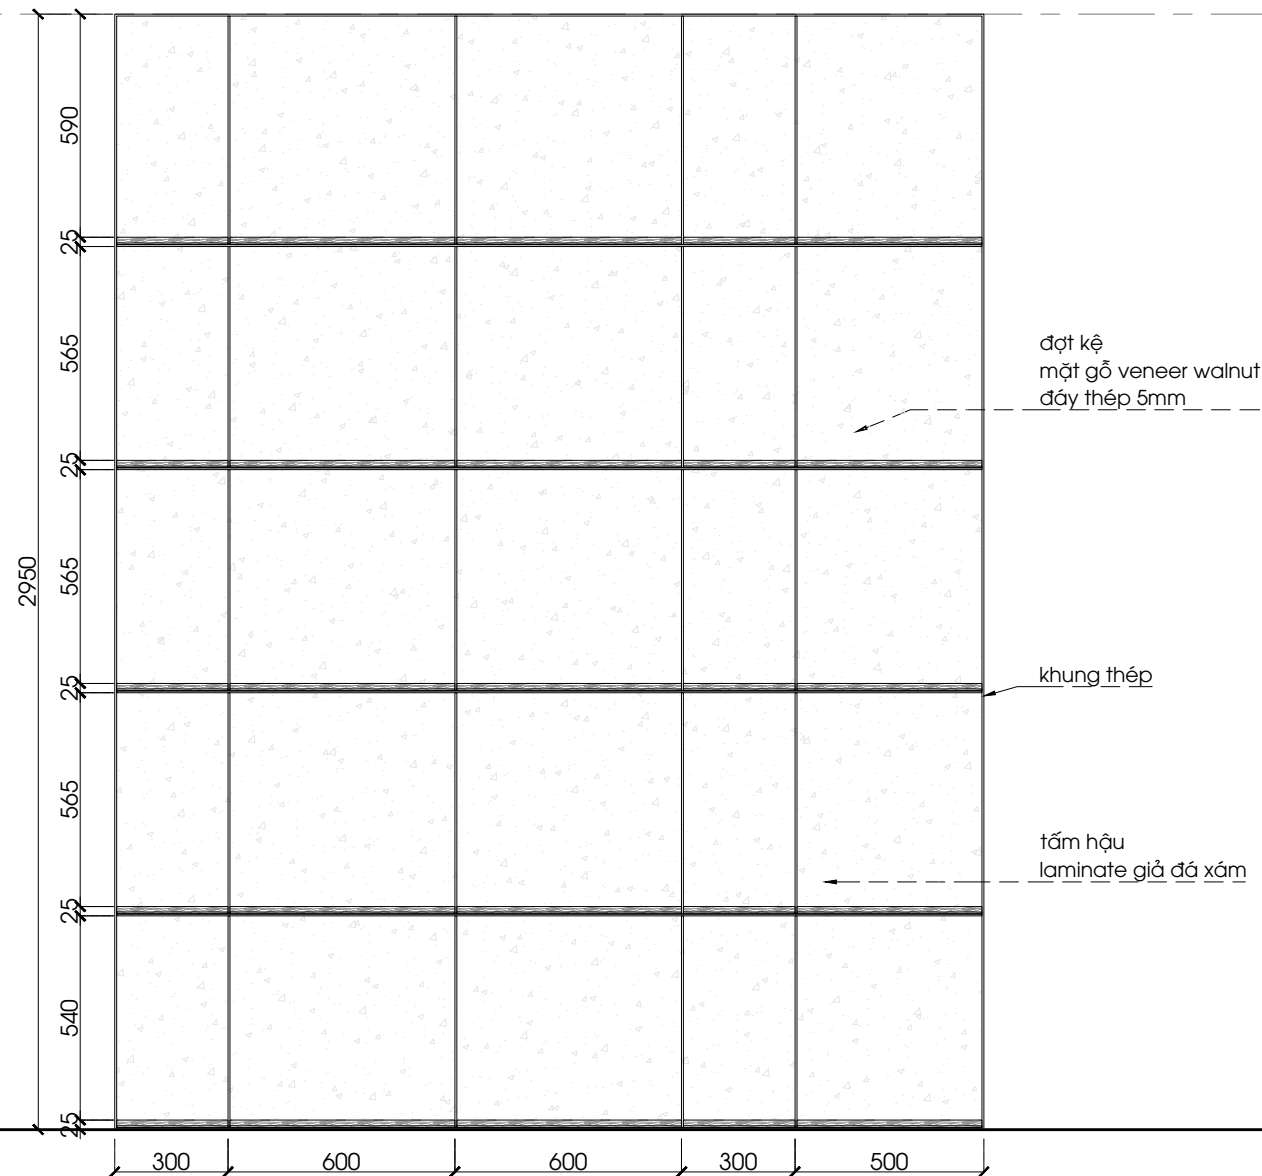


khung thép

tấm hậu
lamine giả đá xám

PP-01 - MẶT ĐỨNG

1:20 @ A3

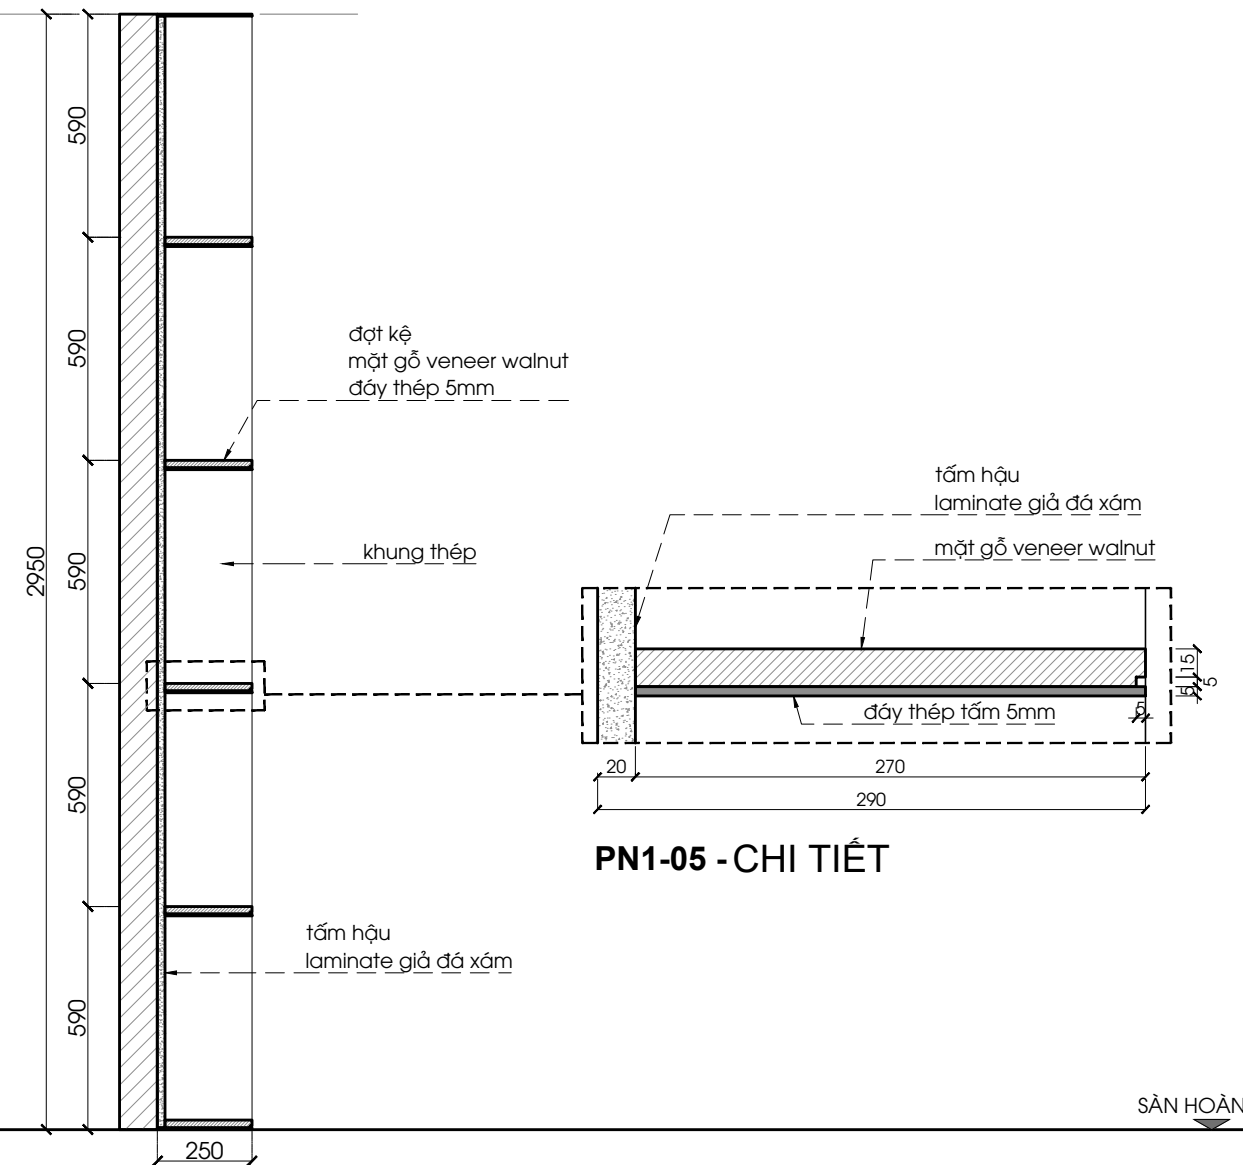

khung thép

tấm hậu
lamine giả đá xám

PN1-05 - CHI TIẾT

ĐÀN HOÀN THIỆN

PP-01 - MẶT CẮT

1:20 @ A3

PHÁT HÀNH		HIỆU CHỈNH		GHI CHÚ - MỌI KÍCH THƯỚC CẦN ĐƯỢC KIỂM TRA THEO THỰC TẾ CÔNG TRƯỜNG	ARCHITECTURAL DESIGN — THIẾT KẾ KIẾN TRÚC CÔNG TY TNHH KIẾN TRÚC VIỆT VACO DESIGN LẦU 1, 30is PHAN VĂN ĐẠT - P. BẾN NGHÉ - Q.1 - TP. HCM TEL: +84-8-38223364 EMAIL: info@vacodesign.com		DESIGNER - CHỦ TRÌ THIẾT KẾ		PROJECT TITLE - TÊN DỰ ÁN		DATE - NGÀY		
					DIRECTOR - GIÁM ĐỐC		DRAWN BY - NGƯỜI VẼ		DRAWING TITLE - TÊN BẢN VẼ		DRAWING NO. - SỐ HIỆU BẢN VẼ	KÝ HIỆU BẢNG VẼ	
					ThS.KTS. ĐỖ QUỐC HIỆP		KTS. TRẦN TRUNG KIẾN		ThS.KTS. ĐỖ QUỐC HIỆP		CĂN HỘ 08.03- 08.04-08.05-08.06		SCALE - TỈ LỆ 1:20





PP-02 - MẶT ĐÚNG

PP-03 - MẶT CẮT


PP-03 - MẶT ĐỨNG

PP-03 - MẶT HÔNG


PHÁT HÀNH		HIỆU CHỈNH		GHI CHÚ	ARCHITECTURAL DESIGN — THIẾT KẾ KIẾN TRÚC CÔNG TY TNHH KIẾN TRÚC VIỆT VACO DESIGN LẦU 1, 3b/1a PHAN VĂN DAT - P. BẾN NGHÉ - Q.1 - TP. HCM TEL: +84-8-38223384 EMAIL: info@vaco-design.com	DESIGNER - CHỦ TRÌ THIẾT KẾ ThS.KTS. ĐỖ QUỐC HIỆP	PROJECT TITLE - TÊN DỰ ÁN CĂN HỘ 08.03- 08.04-08.05-08.06	DATE - NGÀY 03 - 2025	
								SCALE - TỈ LỆ 1:20	
								DRAWING NO. - SỐ HIỆU BẢN VẼ NP-04	KÝ HIỆU BẢNG VẼ N
				DIRECTOR - GIÁM ĐỐC ThS.KTS. ĐỖ QUỐC HIỆP	DRAWN BY - NGƯỜI VẼ KTS. TRẦN TRUNG KIÊN	DRAWING TITLE - TÊN BẢN VẼ CHI TIẾT NỘI THẤT TỦ LAVABO PP-02 TỦ TRANG TRÍ WC PP-03			

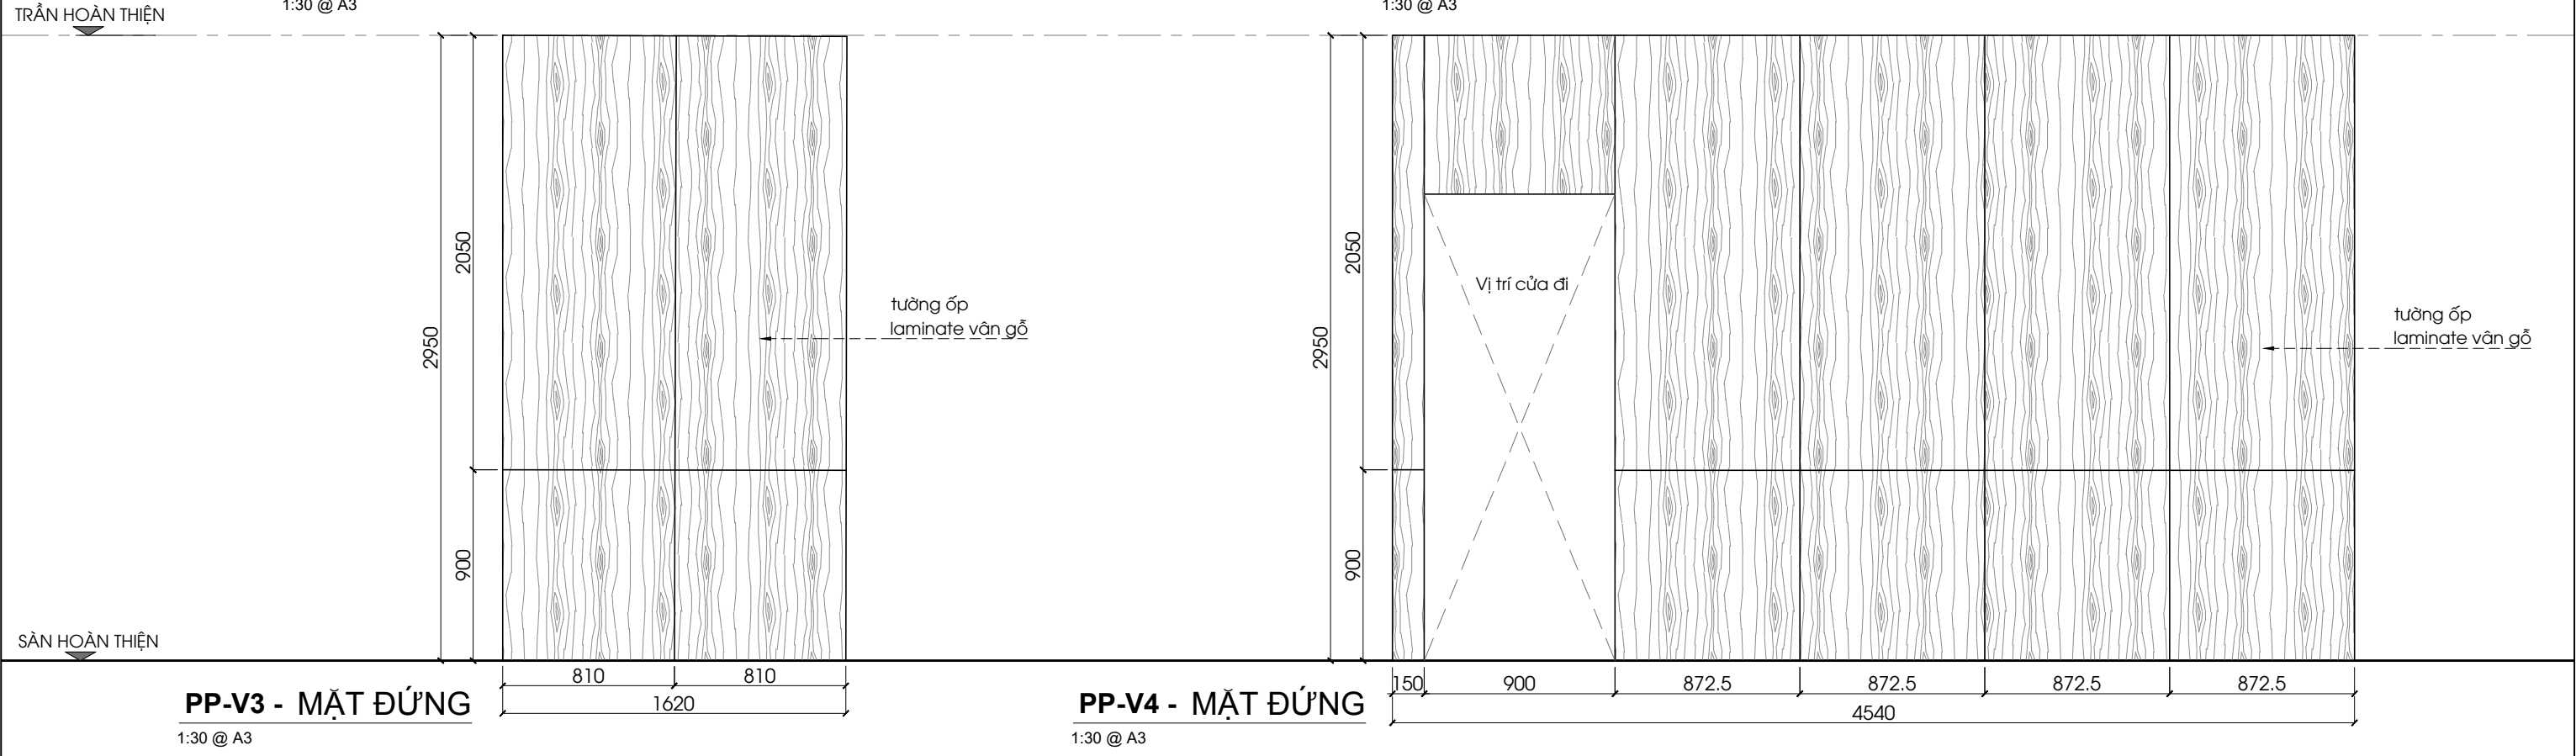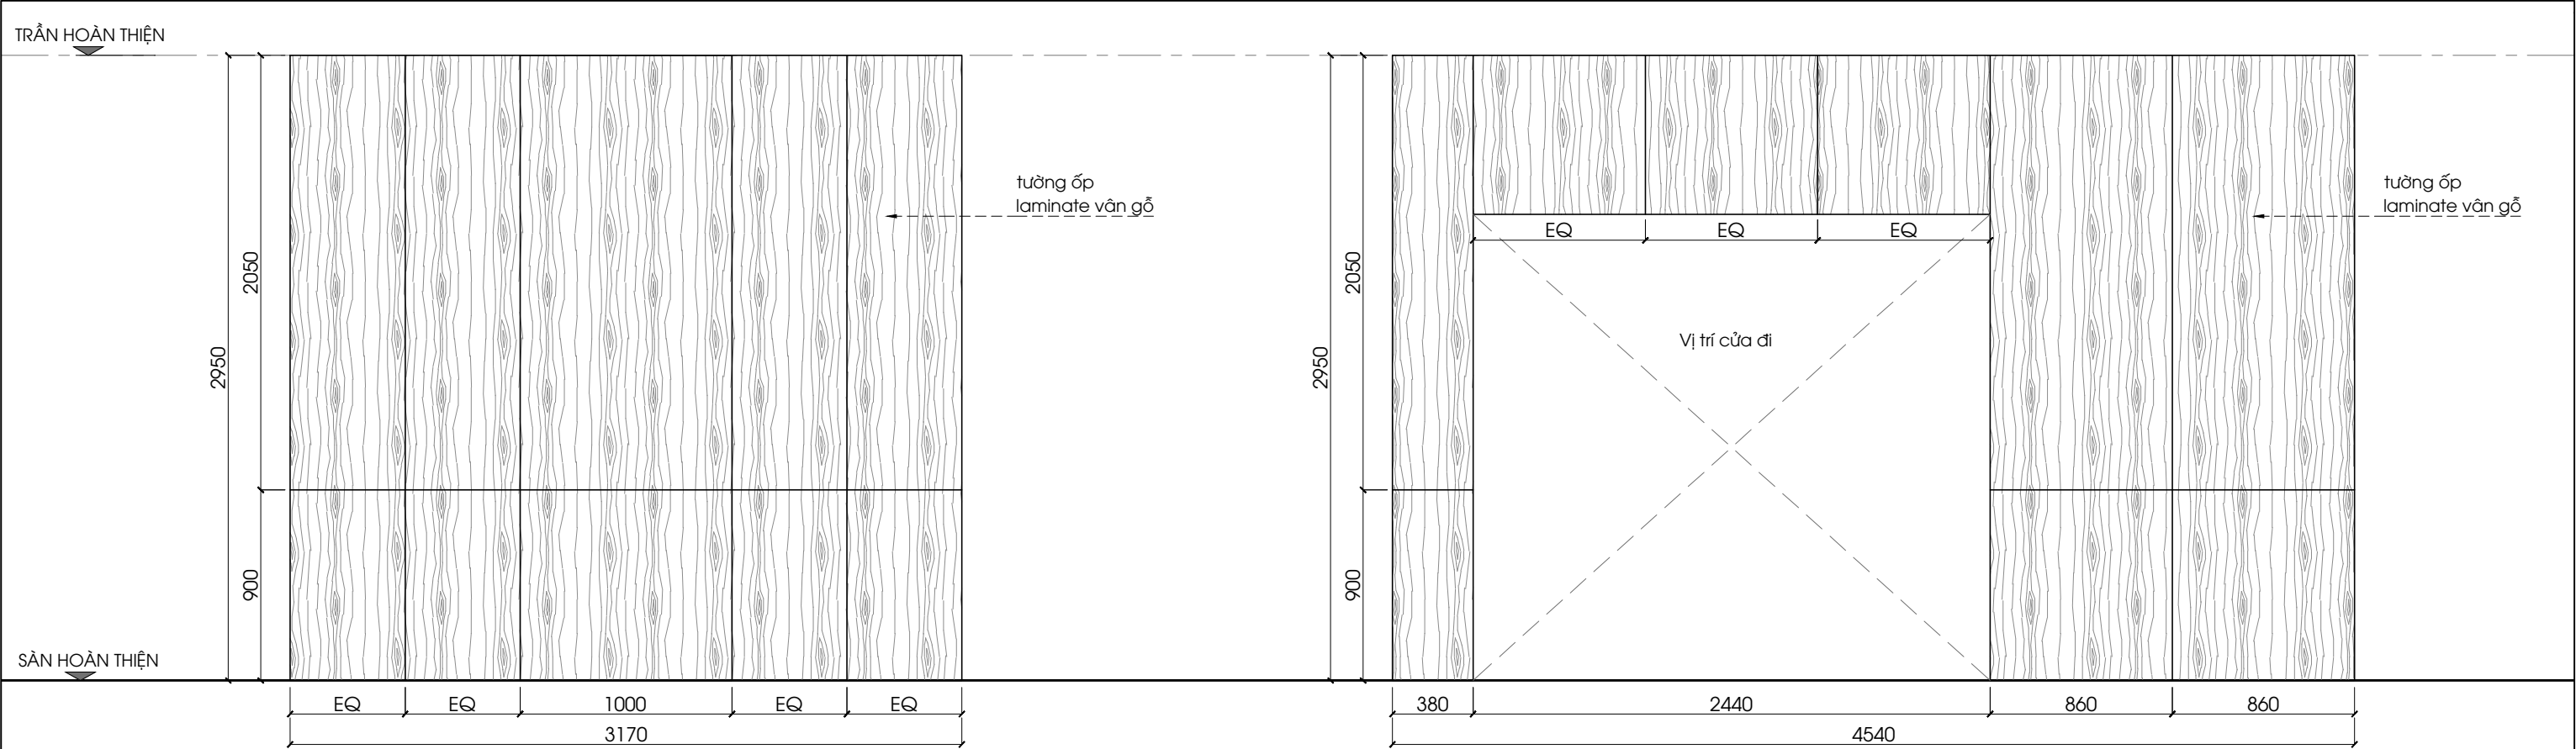

PHÁT HÀNH		HIỆU CHÍNH		GHI CHÚ	ARCHITECTURAL DESIGN — THIẾT KẾ KIẾN TRÚC		DESIGNER - CHỦ TRÌ THIẾT KẾ		PROJECT TITLE - TÊN DỰ ÁN		DATE - NGÀY	
					CÔNG TY TNHH KIẾN TRÚC VIỆT VACO DESIGN LẦU 1, 38b PHAN VĂN ĐẠT - P. BẾN NGHÉ - Q.1 - TP. HCM TEL: +84-9-36223364 EMAIL: info@vacodesign.com	ThS.KTS. ĐỖ QUỐC HIỆP	CĂN HỘ 08.03- 08.04-08.05-08.06	03 - 2025				
								SCALE - TỈ LỆ				
								1:30				
								DRAWING TITLE - TÊN BẢN VẼ				
				- MỌI KÍCH THƯỚC CẦN ĐƯỢC KIỂM TRA THEO THỰC TẾ CÔNG TRƯỜNG	ThS.KTS. ĐỖ QUỐC HIỆP		KTS. TRẦN TRUNG KIẾN		CHI TIẾT NỘI THẤT		DRAWING NO. - SỐ HIỆU BẢN VẼ	
									CHI TIẾT VÁCH ỐP PP-V1, PP-V2, PP-V3, PP-V4			
											NP-05	
											KÝ HIỆU BẢNG VẼ	
											N	

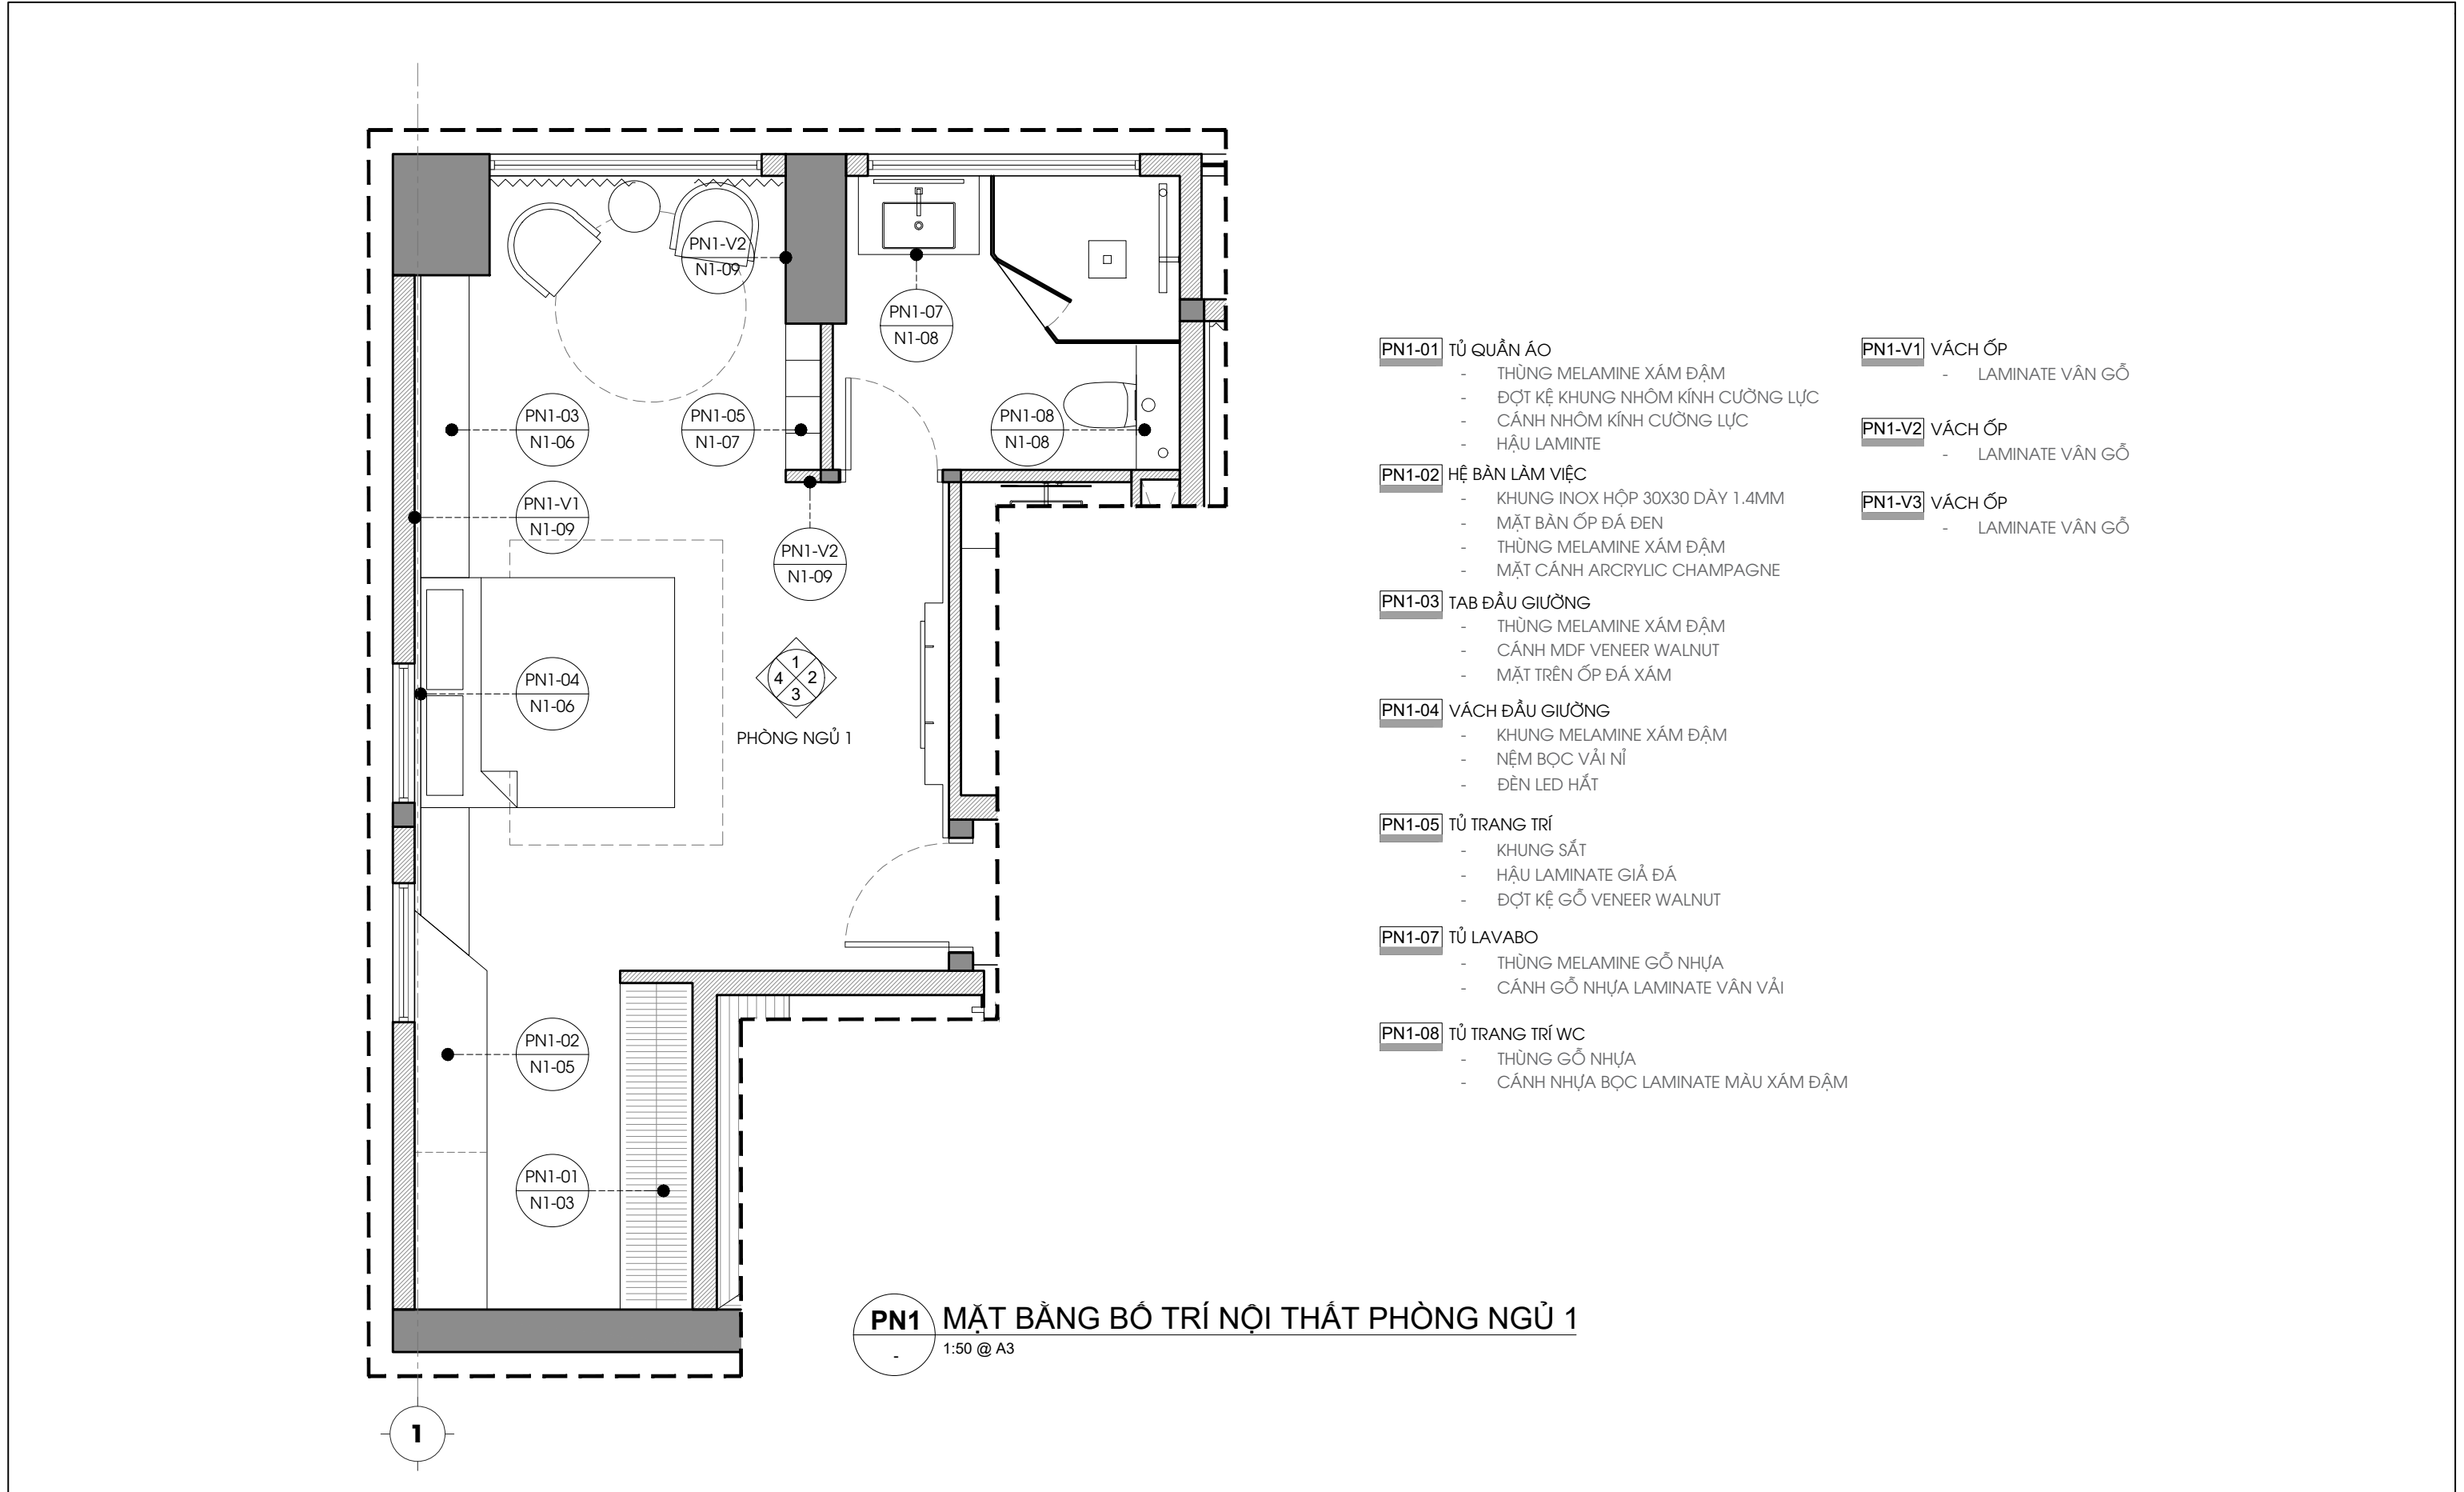


PHÁT HÀNH		HIỆU CHÍNH		GHI CHÚ	ARCHITECTURAL DESIGN — THIẾT KẾ KIẾN TRÚC		DESIGNER - CHỦ TRÌ THIẾT KẾ		PROJECT TITLE - TÊN DỰ ÁN		DATE - NGÀY	
					CÔNG TY TNHH KIẾN TRÚC VIỆT VACO DESIGN LẦU 1, 3bis PHAN VĂN ĐẠT - P. BẾN NGHÉ - Q.1 - TP. HCM TEL: +84-9-36223364 EMAIL: info@vacodesign.com			CĂN HỘ 08.03- 08.04-08.05-08.06	03 - 2025			

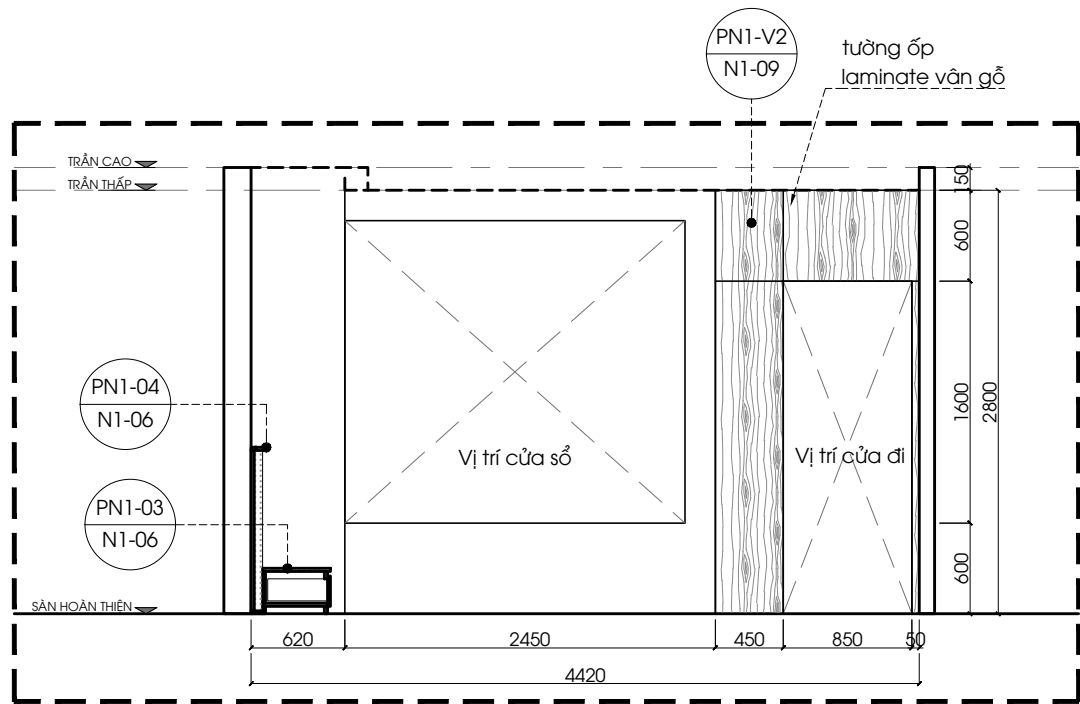


PN1 MẶT ĐỨNG 1

1:50 @ A3

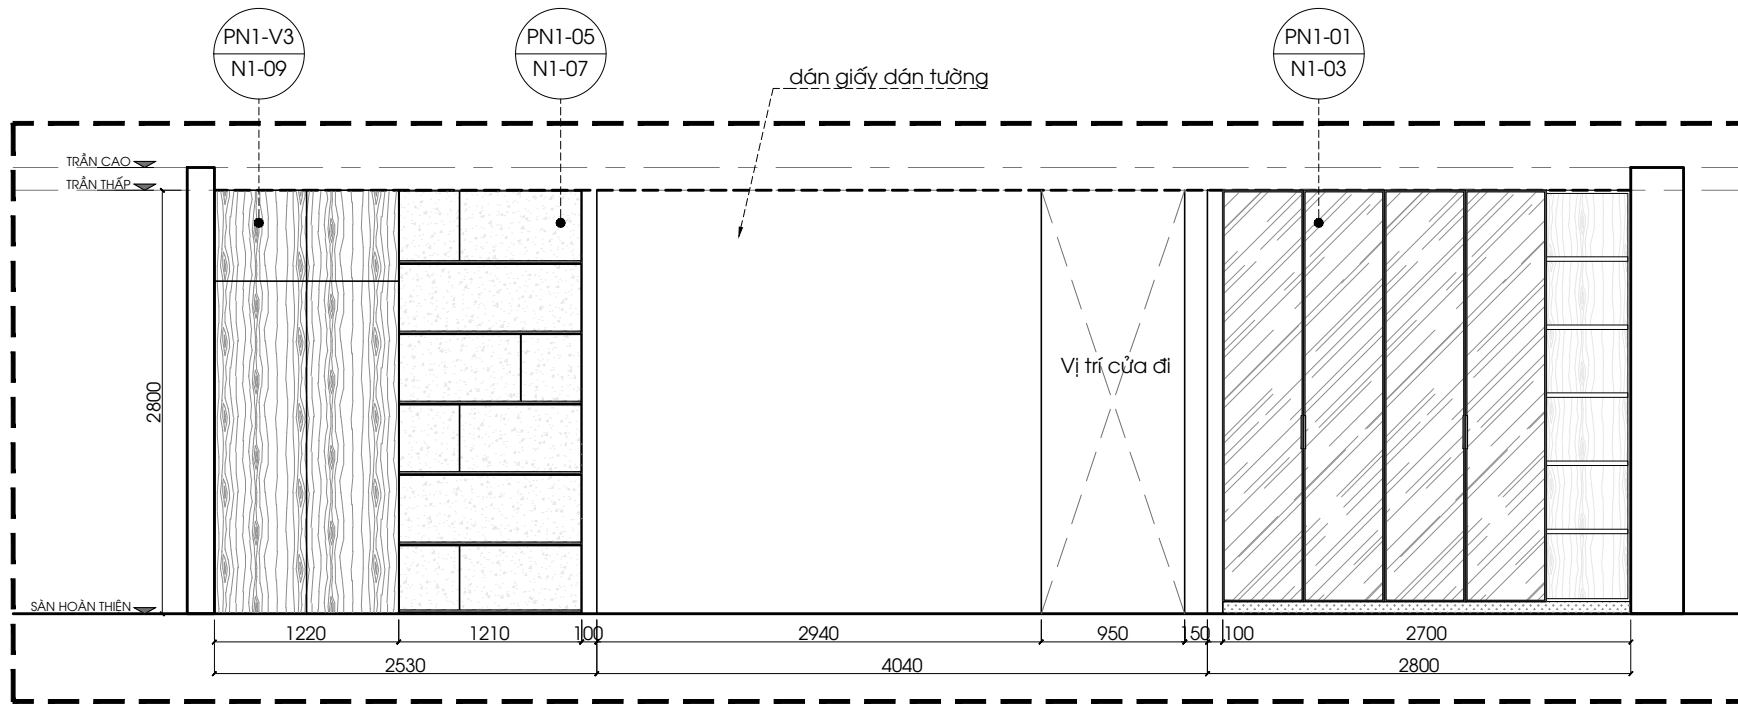


PN1 MẶT ĐỨNG 2

1:50 @ A3

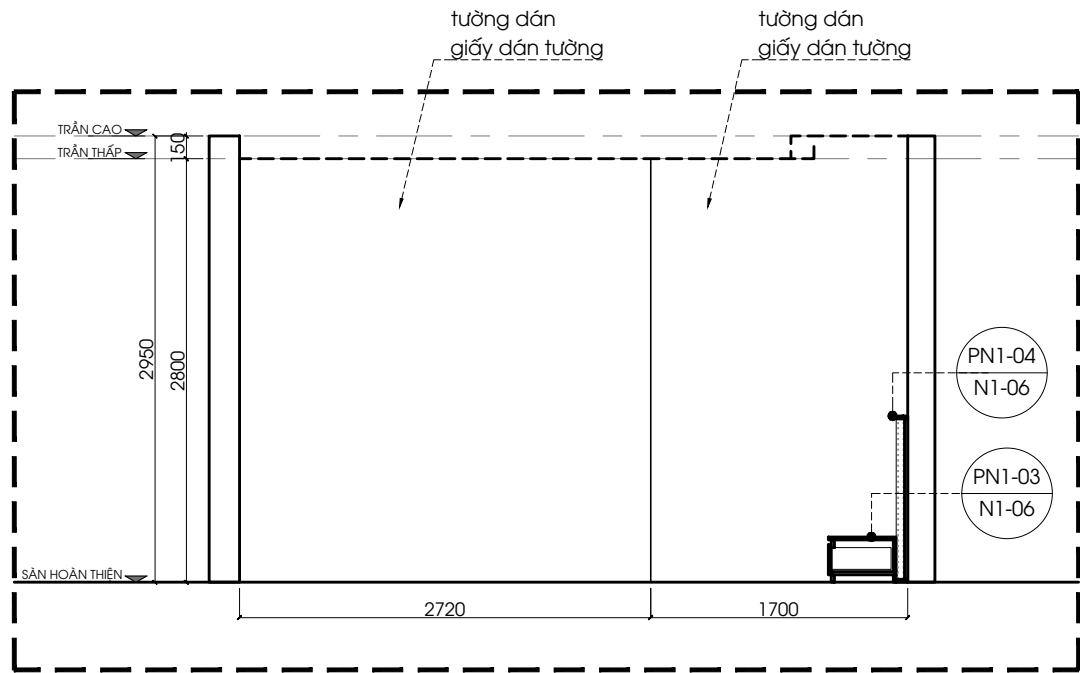

PN1 MẶT ĐỨNG 3


1:50 @ A3

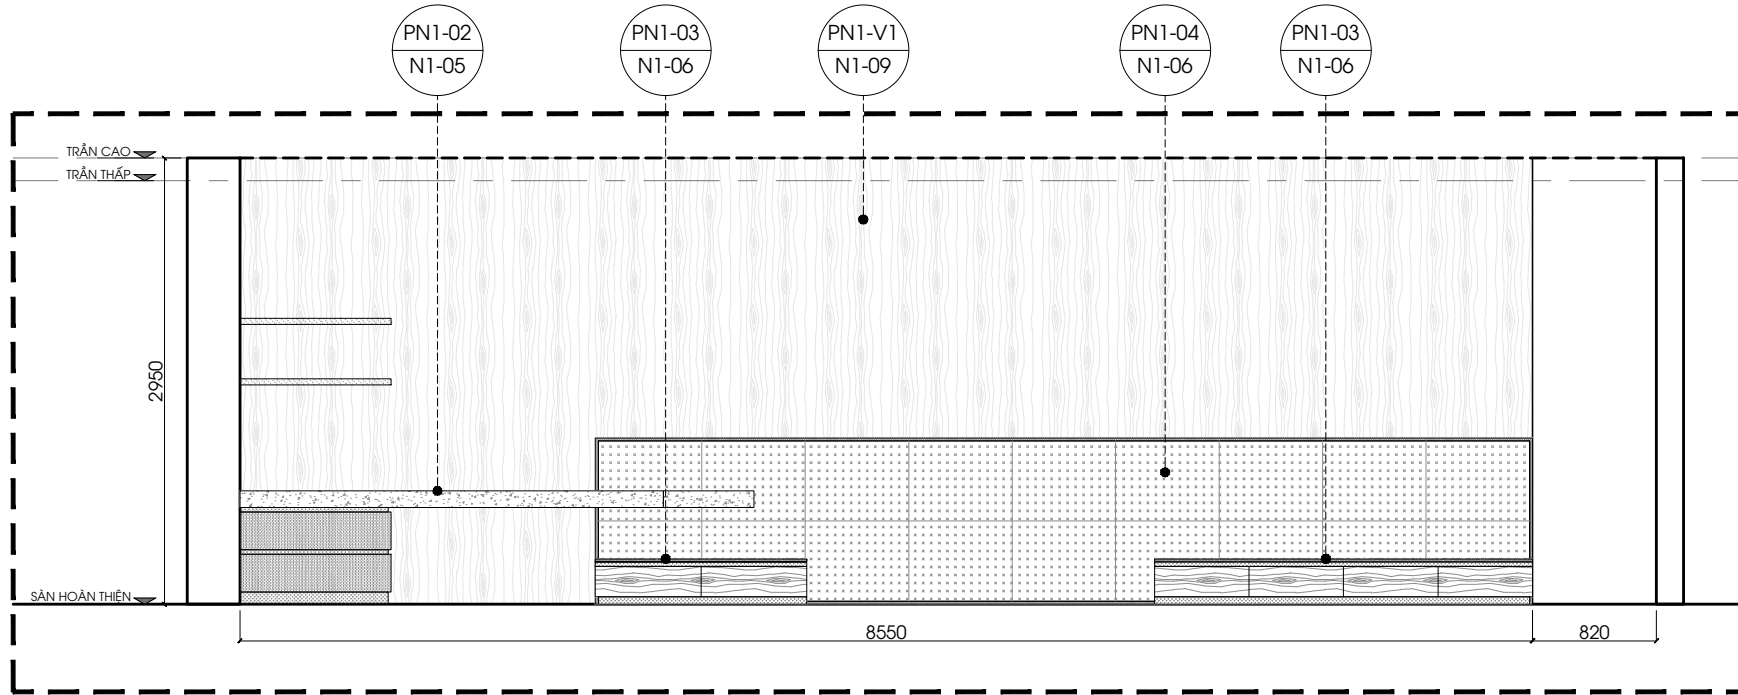

PN1 MẶT ĐỨNG 4

1:50 @ A3

PHÁT HÀNH		HIỆU CHÍNH		GHI CHÚ	ARCHITECTURAL DESIGN — THIẾT KẾ KIẾN TRÚC		DESIGNER - CHỦ TRÌ THIẾT KẾ		PROJECT TITLE - TÊN DỰ ÁN		DATE - NGÀY		
					- MỌI KÍCH THƯỚC CẦN ĐƯỢC KIỂM TRA THEO THỰC TẾ CÔNG TRƯỜNG	CÔNG TY TNHH KIẾN TRÚC VIỆT VACO DESIGN LẦU 1, 3bis PHAN VĂN ĐẠT - P. BẾN NGHÉ - Q.1 - TP. HCM TEL: +84-9-38223384 EMAIL: info@vacodesign.com	ThS.KTS. ĐỖ QUỐC HIỆP	CĂN HỘ 08.03- 08.04-08.05-08.06	ThS.KTS. ĐỖ QUỐC HIỆP	CĂN HỘ 08.03- 08.04-08.05-08.06	03 - 2025		
												SCALE - TỈ LỆ	1:50
				DIRECTOR - GIÁM ĐỐC	DRAWN BY - NGƯỜI VẼ	DRAWING TITLE - TÊN BẢN VẼ	DRAWING NO. - SỐ HIỆU BẢN VẼ	KÝ HIỆU BẢNG VẼ					
				ThS.KTS. ĐỖ QUỐC HIỆP	KTS. TRẦN TRUNG KIẾN	MẶT ĐỨNG NỘI THẤT PHÒNG NGỦ 1	N1-02	N					

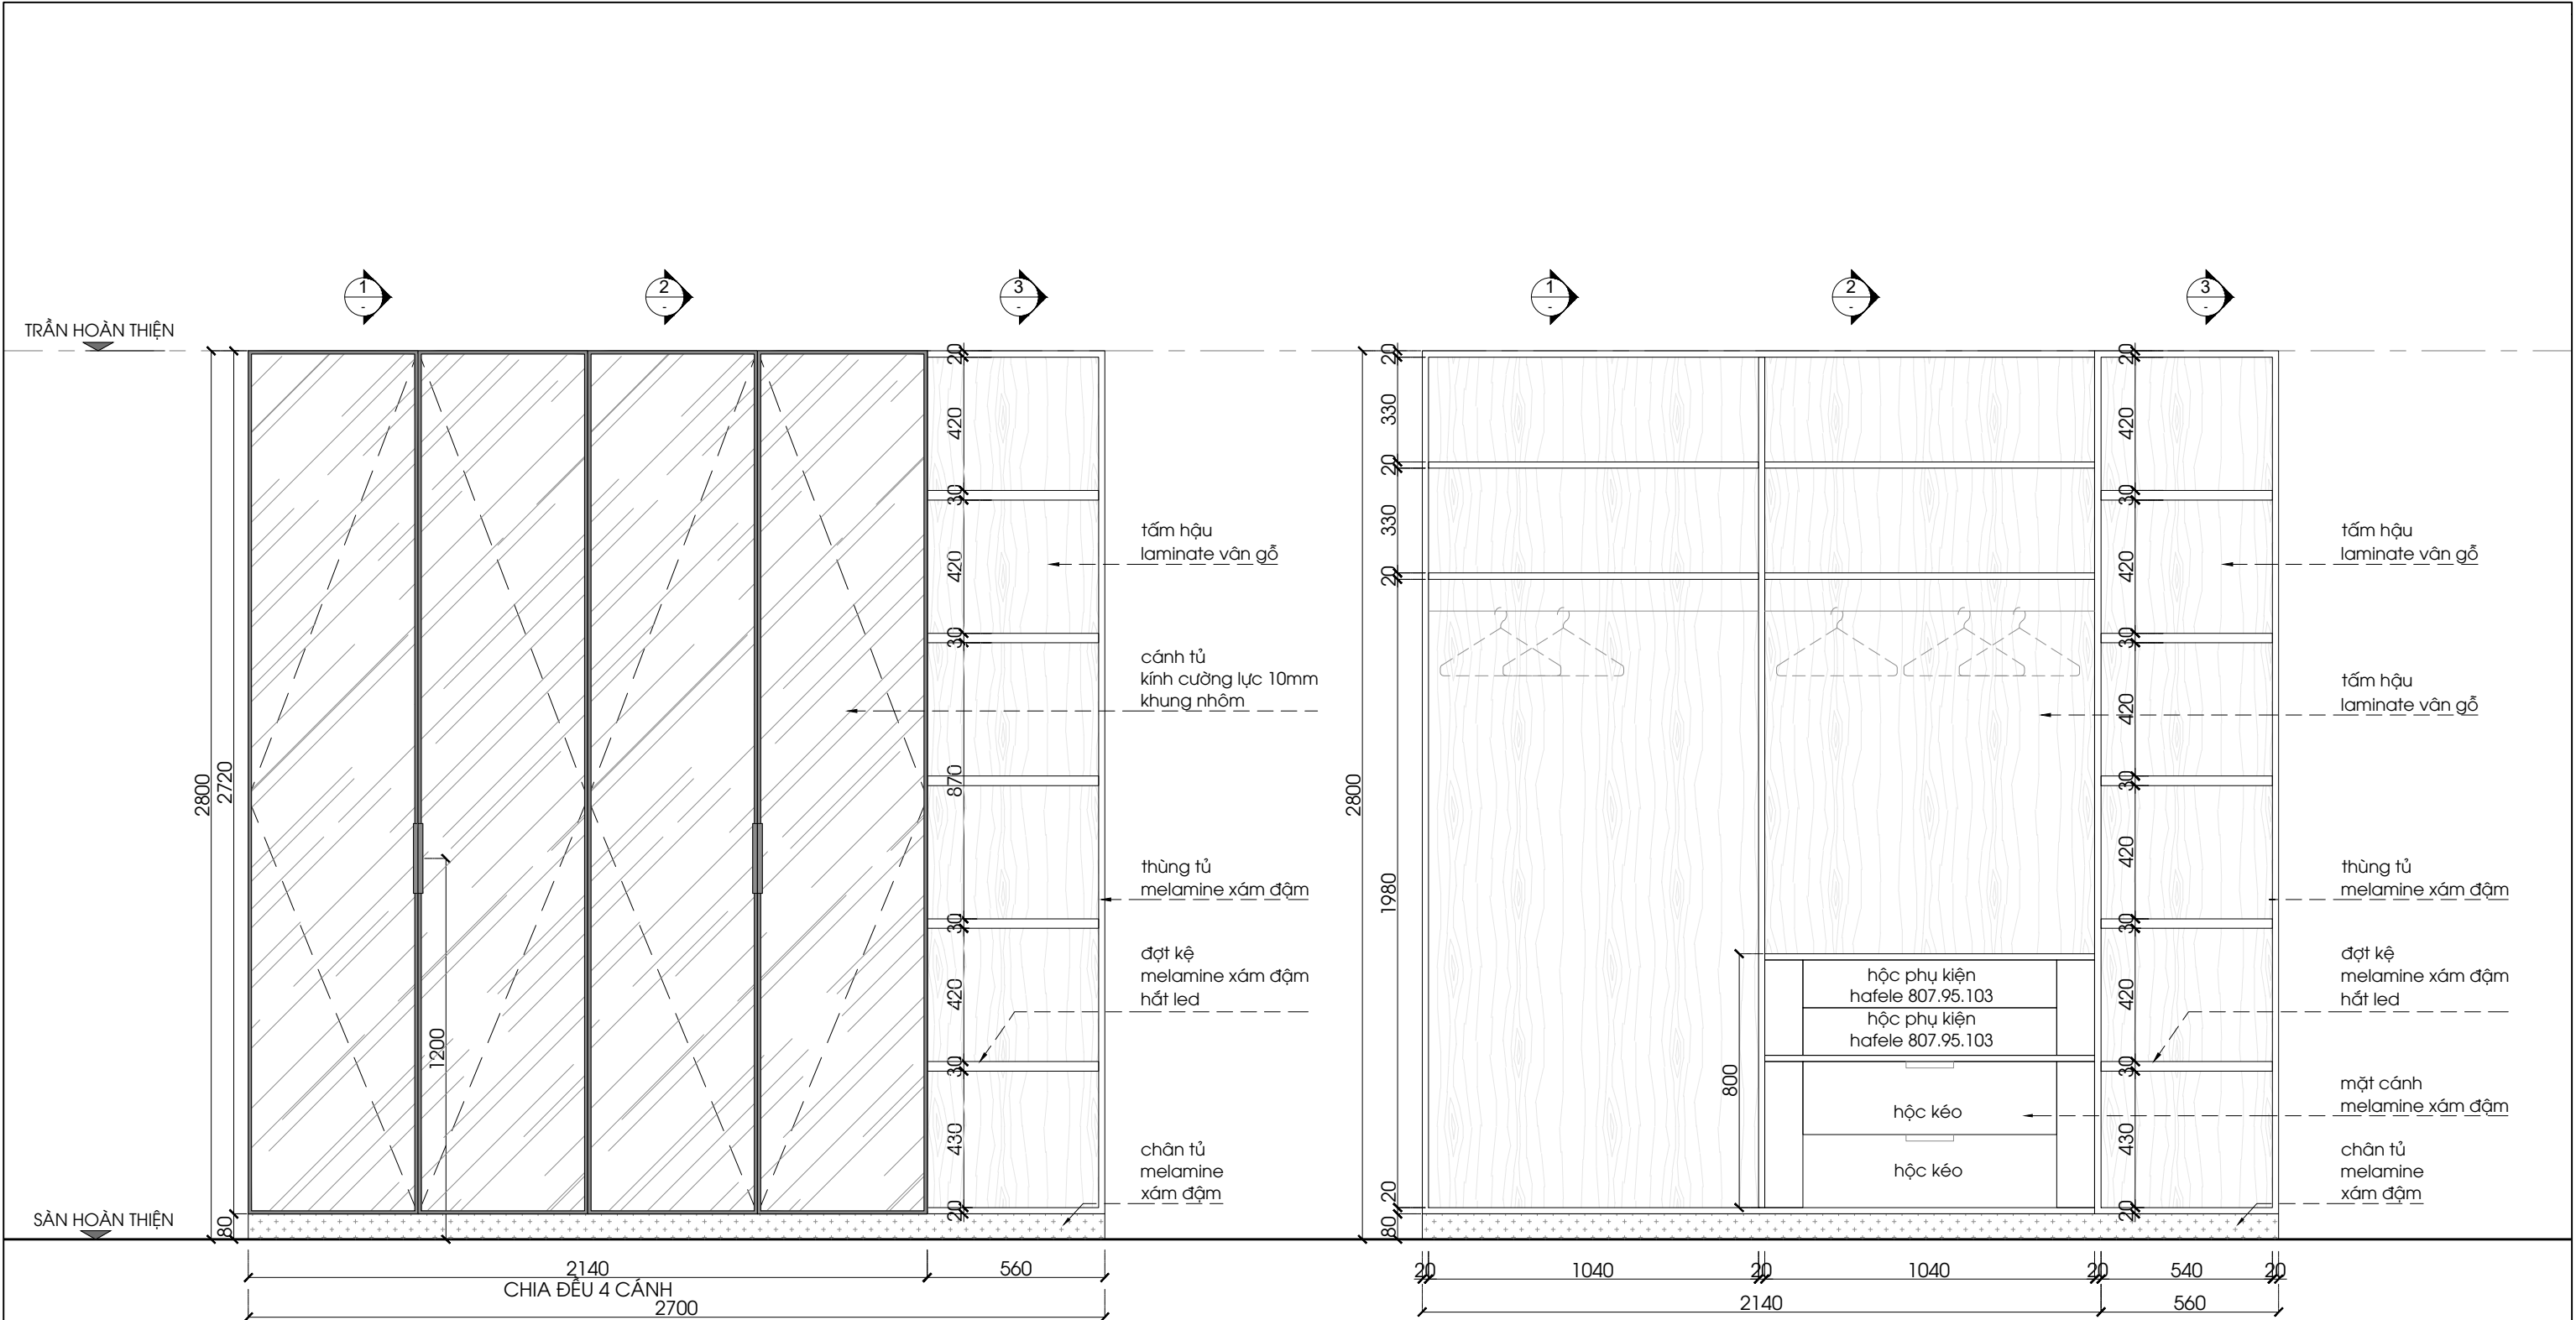

PN1- 01- MẶT ĐỪNG

1:20 @ A3


PN1- 01- MẶT ĐỪNG - KHÔNG CÁNH

1:20 @ A3


PHÁT HÀNH		HIỆU CHÍNH		GHI CHÚ	ARCHITECTURAL DESIGN — THIẾT KẾ KIẾN TRÚC		DESIGNER - CHỦ TRÌ THIẾT KẾ		PROJECT TITLE - TÊN DỰ ÁN		DATE - NGÀY	
					- MỌI KÍCH THƯỚC CẦN ĐƯỢC KIỂM TRA THEO THỰC TẾ CÔNG TRƯỜNG	CÔNG TY TNHH KIẾN TRÚC VIỆT VACO DESIGN LẦU 1, 3bis PHAN VĂN ĐẠT - P. BẾN NGHÉ - Q.1 - TP. HCM TEL: +84-9-36223364 EMAIL: info@vacodesign.com			CĂN HỘ 08.03- 08.04-08.05-08.06	03 - 2025		
								ThS.KTS. ĐỖ QUỐC HIỆP		SCALE - TỈ LỆ		
										1:20		
								</				

TRẦN HOÀN THIỆN


SÀN HOÀN THIỆN

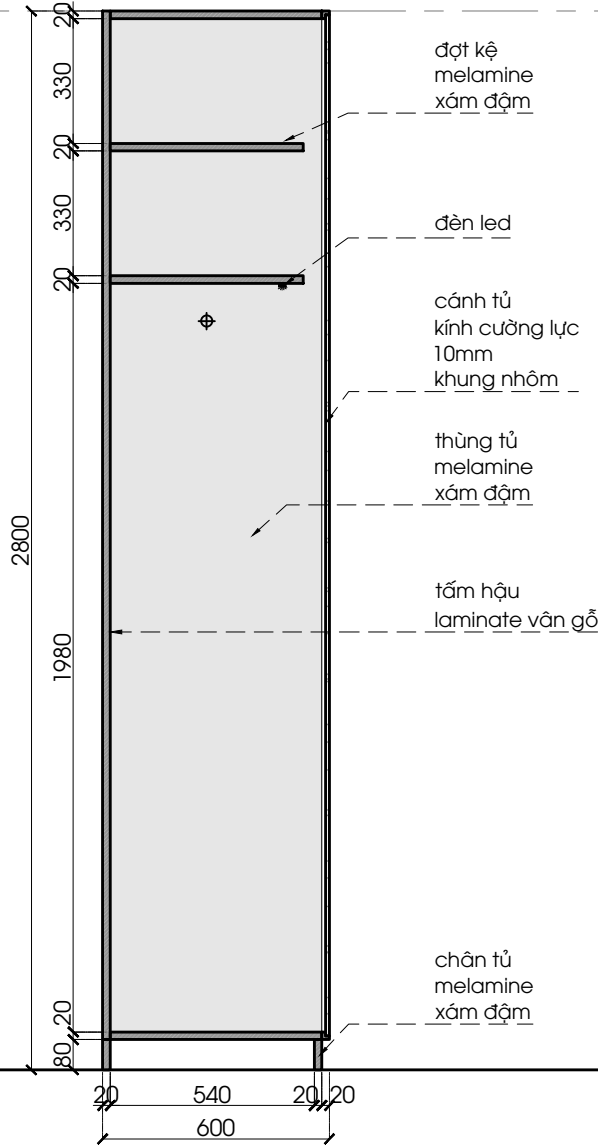


PN1-01- MẶT CẮT 1
1:20 @ A3

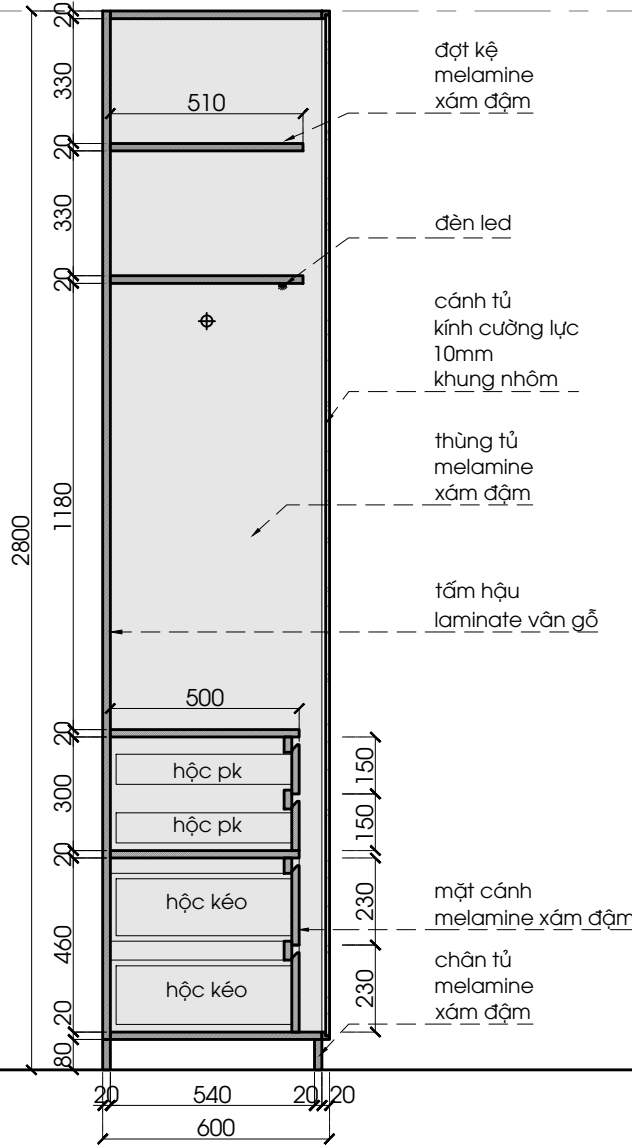

PN1-01- MẶT CẮT 2
1:20 @ A3

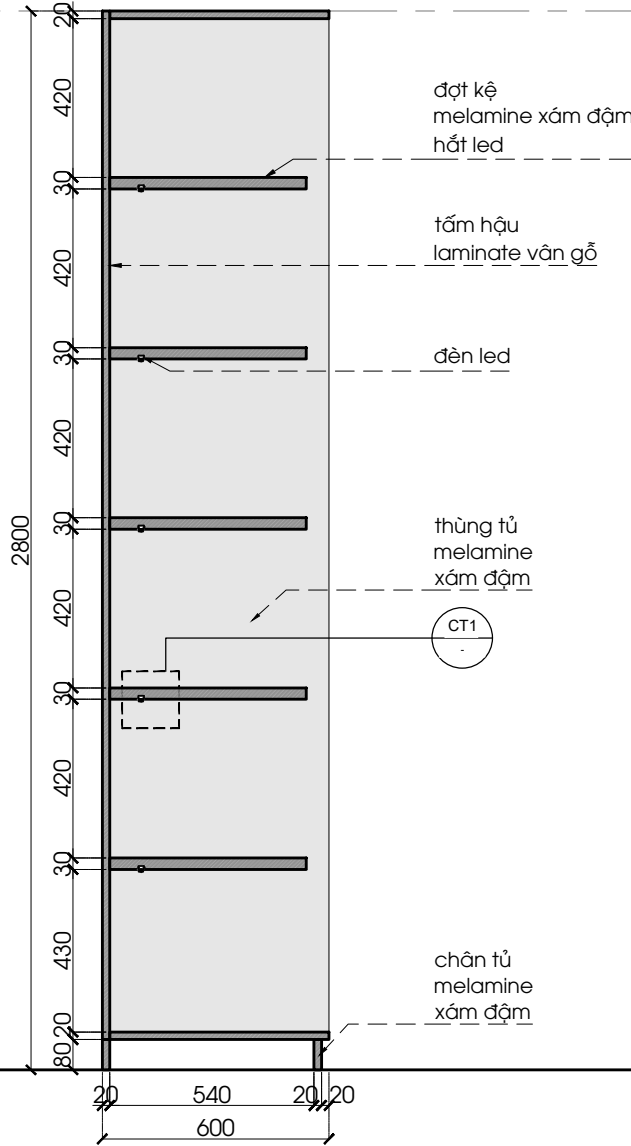


PN1-01- MẶT CẮT 3
1:20 @ A3

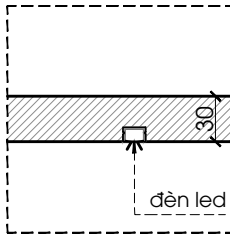


CHI TIẾT 1



PHÁT HÀNH		HIỆU CHÍNH		GHI CHÚ - MỌI KÍCH THƯỚC CẦN ĐƯỢC KIỂM TRA THEO THỰC TẾ CÔNG TRƯỜNG	ARCHITECTURAL DESIGN — THIẾT KẾ KIẾN TRÚC  CÔNG TY TNHH KIẾN TRÚC VIỆT VACO DESIGN LẦU 1, 38/6 PHAN VĂN ĐẠT - P. BẾN NGHÉ - Q.1 - TP. HCM TEL: +84-9-36223364 EMAIL: info@vacodesign.com		DESIGNER - CHỦ TRÌ THIẾT KẾ		PROJECT TITLE - TÊN DỰ ÁN		DATE - NGÀY 03 - 2025	
					DIRECTOR - GIÁM ĐỐC ThS.KTS. ĐỖ QUỐC HIỆP	DRAWN BY - NGƯỜI VẼ KTS. TRẦN TRUNG KIẾN	DRAWING TITLE - TÊN BẢN VẼ CHI TIẾT NỘI THẤT TỦ QUẦN ÁO PN1-01	DRAWING NO. - SỐ HIỆU BẢN VẼ N1-04	KÝ HIỆU BẢNG VẼ N	SCALE - TỈ LỆ 1:20		

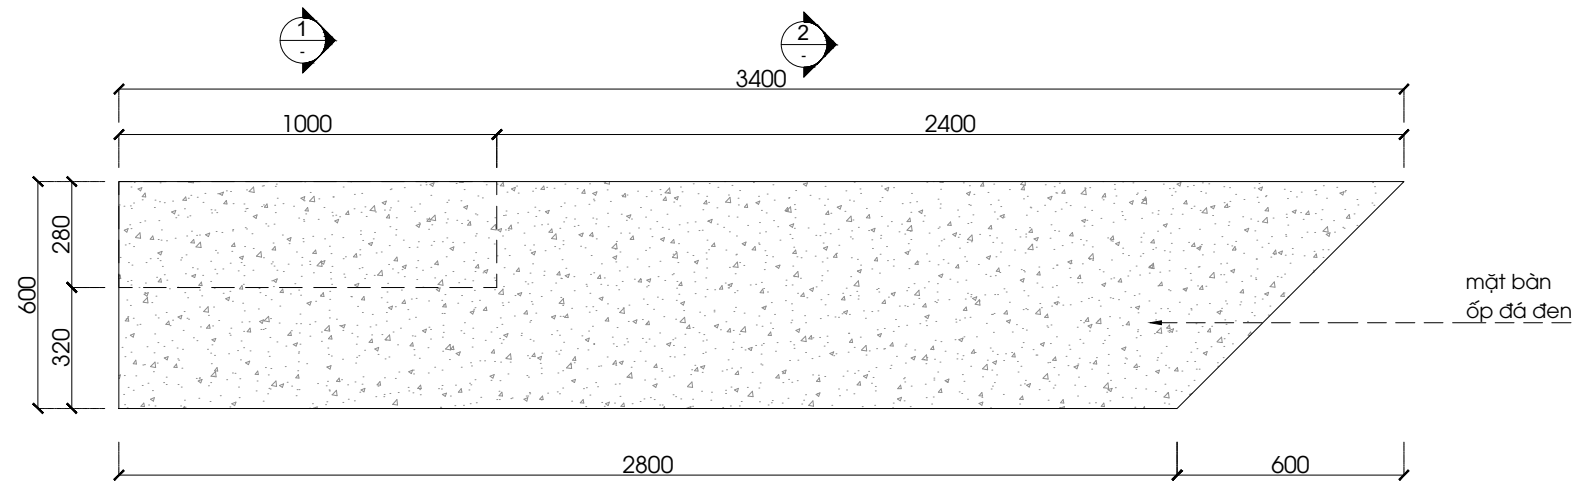

PN1- 02- MẶT BẰNG
1:20 @ A3

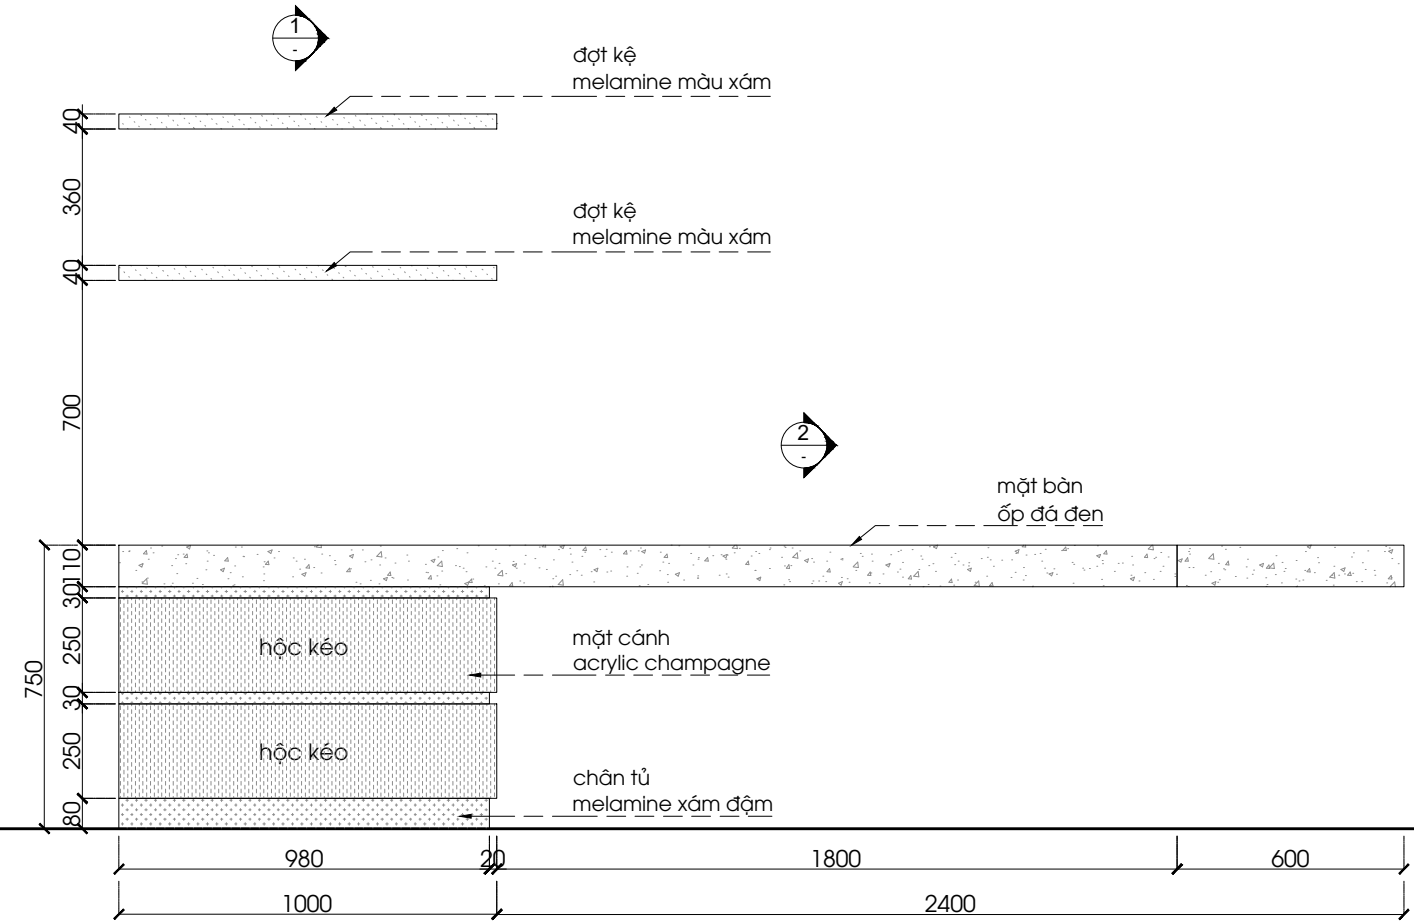


PN1- 02- MẶT ĐỨNG
1:20 @ A3

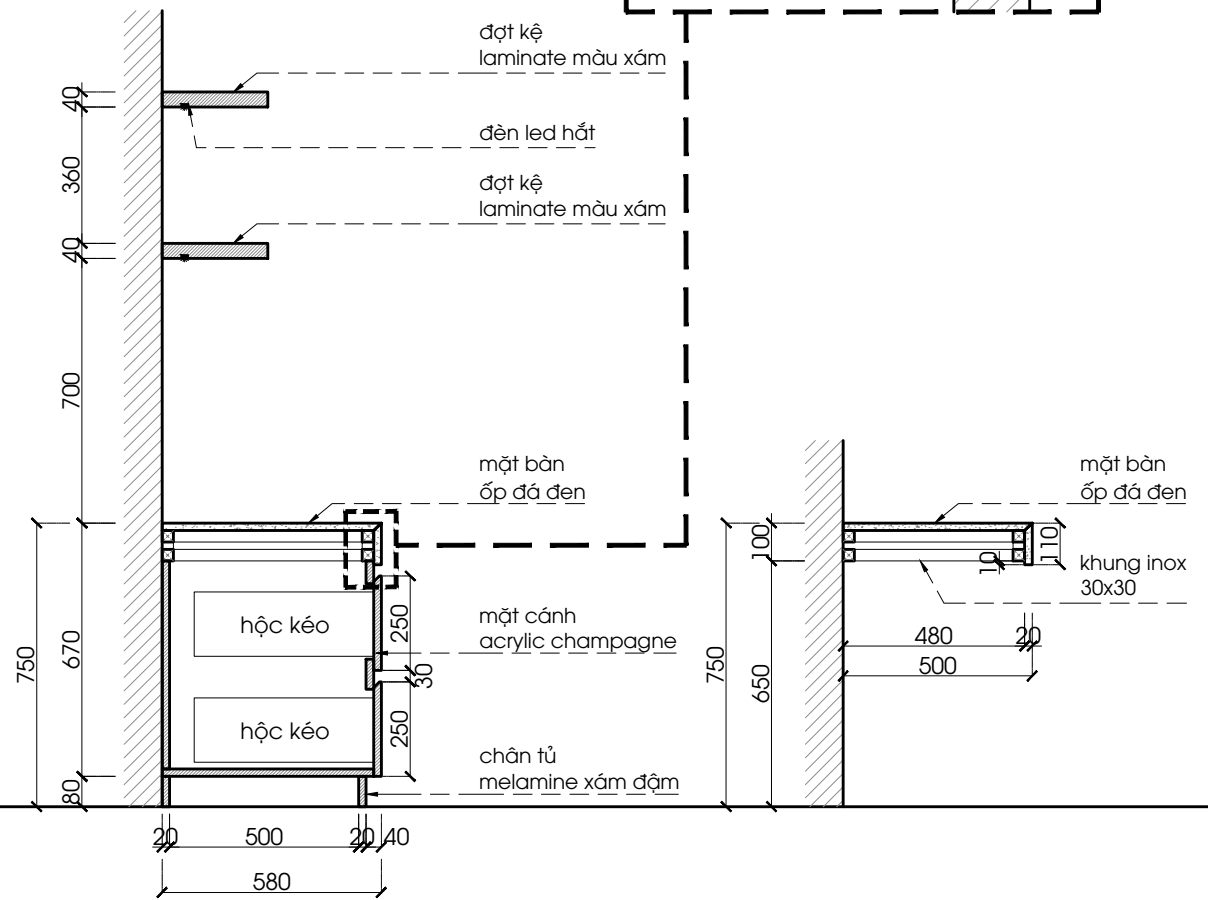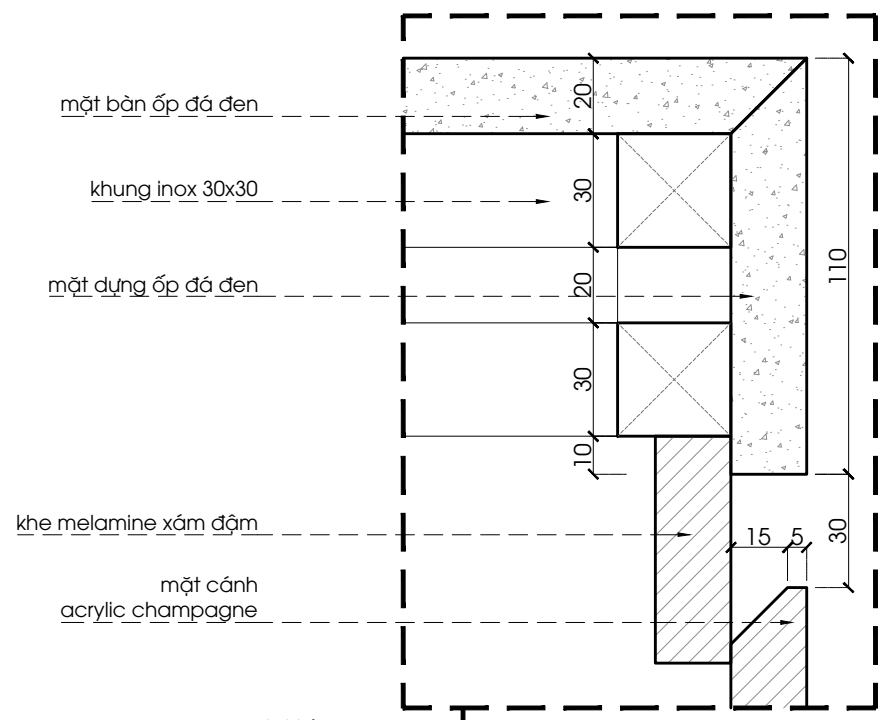

PN1- 02- MẶT CẮT 1
1:20 @ A3


PN1- 02- MẶT CẮT 2
1:20 @ A3

PHÁT HÀNH		HIỆU CHÍNH		GHI CHÚ - MỌI KÍCH THƯỚC CẦN ĐƯỢC KIỂM TRA THEO THỰC TẾ CÔNG TRƯỜNG	ARCHITECTURAL DESIGN — THIẾT KẾ KIẾN TRÚC CÔNG TY TNHH KIẾN TRÚC VIỆT VACO DESIGN LẦU 1, 38b PHAN VĂN ĐẠT · P. BẾN NGHÉ · Q.1 · TP. HCM TEL: +84-9-36223364 EMAIL: info@vacodesign.com DESIGN DIRECTOR - GIÁM ĐỐC ThS.KTS. ĐỖ QUỐC HIỆP	DESIGNER - CHỦ TRÌ THIẾT KẾ		PROJECT TITLE - TÊN DỰ ÁN		DATE - NGÀY	
						CĂN HỘ 08.03- 08.04-08.05-08.06		03 - 2025			
						ThS.KTS. ĐỖ QUỐC HIỆP		SCALE - TỈ LỆ			
								1:20			
						DRAWN BY - NGƯỜI VẼ		DRAWING TITLE - TÊN BẢN VẼ			
						KTS. TRẦN TRUNG KIÊN		DRAWING NO. - SỐ HIỆU BẢN VẼ			
						CHI TIẾT NỘI THẤT HỆ BÀN LÂM VIỆC PN1-02		N1-05			
						KÝ HIỆU BẢNG VẼ					
						N					

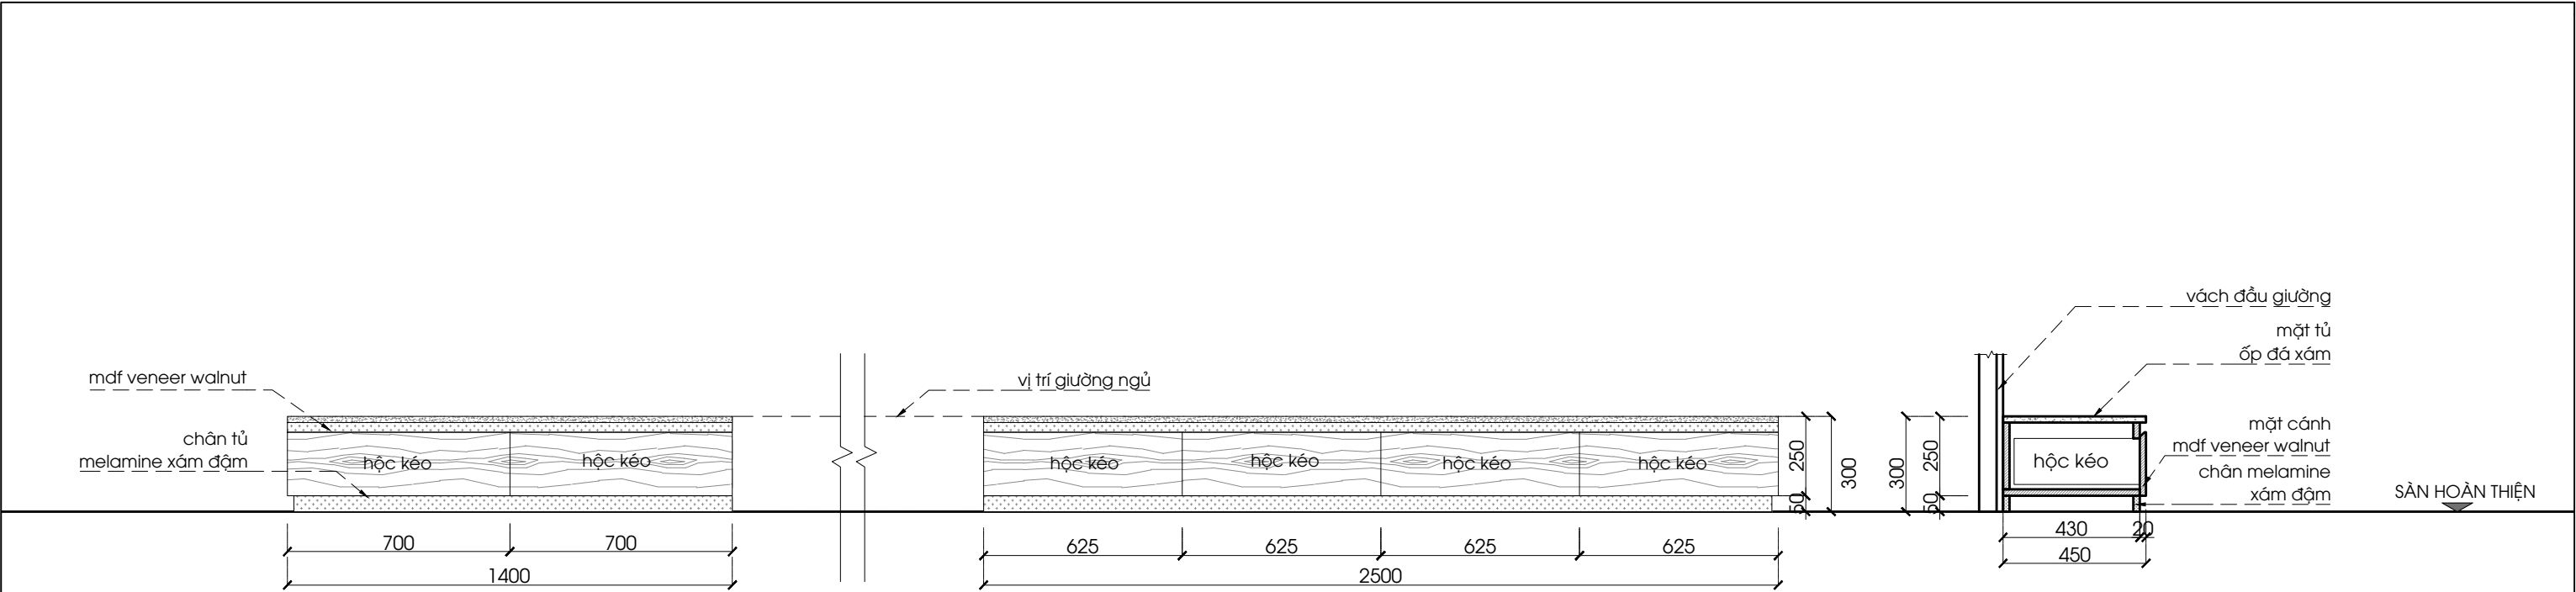

PN1-03 - MẶT ĐỨNG
1:20 @ A3


PN1-03 - MẶT CẮT
1:20 @ A3

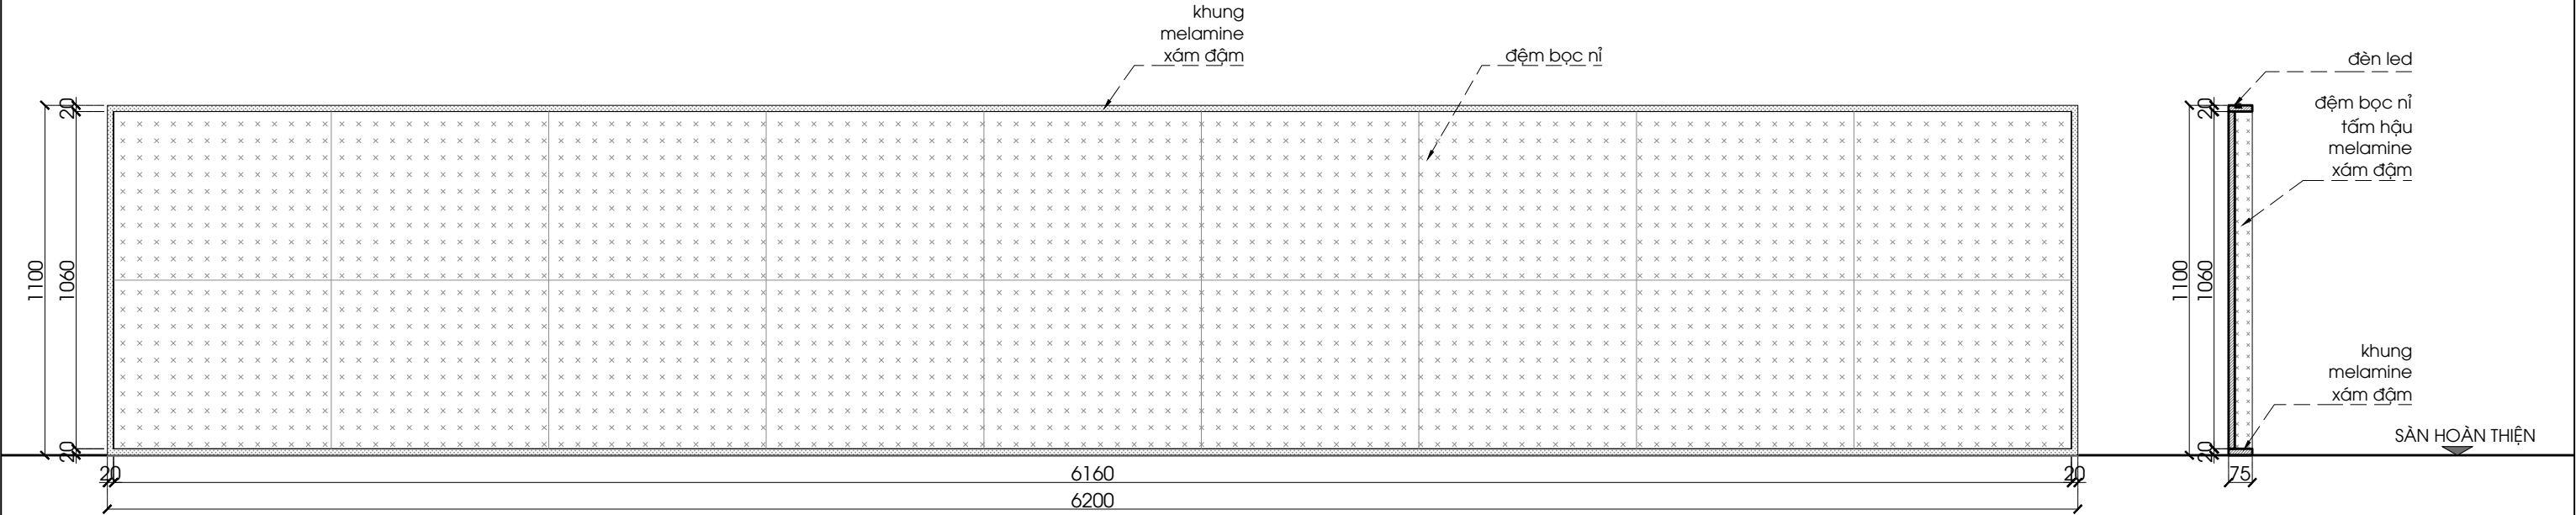

PN1-04 - MẶT ĐỨNG
1:20 @ A3


PN1-04 - MẶT CẮT
1:20 @ A3

PHÁT HÀNH		HIỆU CHÍNH		GHI CHÚ	ARCHITECTURAL DESIGN — THIẾT KẾ KIẾN TRÚC		DESIGNER - CHỦ TRÌ THIẾT KẾ		PROJECT TITLE - TÊN DỰ ÁN		DATE - NGÀY	
					- MỌI KÍCH THƯỚC CẦN ĐƯỢC KIỂM TRA THEO THỰC TẾ CÔNG TRƯỜNG	CÔNG TY TNHH KIẾN TRÚC VIỆT VACO DESIGN LẦU 1, 3bis PHAN VĂN ĐẠT - P. BẾN NGHÉ - Q.1 - TP. HCM TEL: +84-9-36233584 EMAIL: info@vacodesign.com	ThS.KTS. ĐỖ QUỐC HIỆP	CĂN HỘ 08.03- 08.04-08.05-08.06	03 - 2025	SCALE - TỈ LỆ 1:20		
				DIRECTOR - GIÁM ĐỐC	DRAWN BY - NGƯỜI VẼ	DRAWING TITLE - TÊN BẢN VẼ	DRAWING NO. - SỐ HIỆU BẢN VẼ	KÝ HIỆU BẢNG VẼ				
				ThS.KTS. ĐỖ QUỐC HIỆP	KTS. TRẦN TRUNG KIẾN	CHI TIẾT NỘI THẤT TAB ĐẦU GIƯỜNG PN1-03 VÁCH ĐẦU GIƯỜNG PN1-04	N1-06	N				

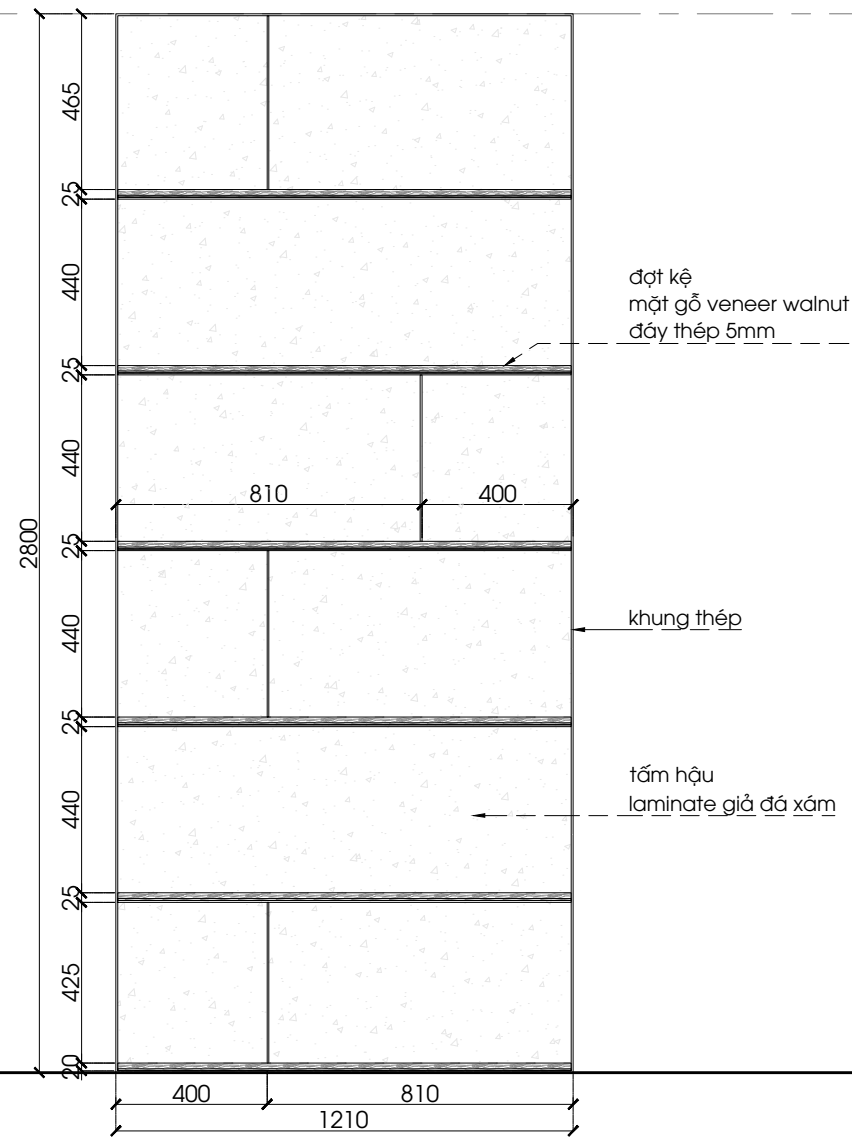

PN1-05 - MẶT ĐỨNG

1:20 @ A3

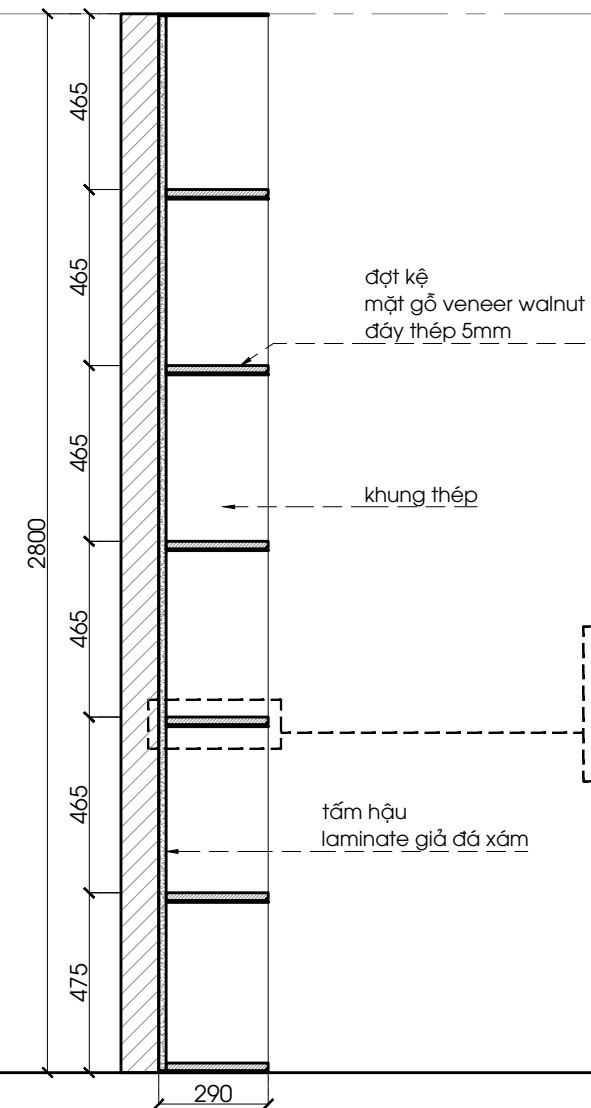



khung thép

tấm hậu
lamine giả đá xám

PN1-05 - CHI TIẾT

ÀN HOÀN THIỆN

 PHÁT HÀNH		HIỆU CHỈNH		GHI CHÚ - MỌI KÍCH THƯỚC CẦN ĐƯỢC KIỂM TRA THEO THỰC TẾ CÔNG TRƯỜNG	ARCHITECTURAL DESIGN — THIẾT KẾ KIẾN TRÚC  CÔNG TY TNHH KIẾN TRÚC VIỆT VACO DESIGN LẦU 1, 3bis PHAN VĂN ĐẠT - P. BẾN NGHÉ - Q. 1 - TP. HCM TEL: +84-8-38223384 EMAIL: info@vacodesign.com		DESIGNER - CHỦ TRÌ THIẾT KẾ ThS.KTS. ĐỖ QUỐC HIỆP		PROJECT TITLE - TÊN DỰ ÁN CĂN HỘ 08.03- 08.04-08.05-08.06		DATE - NGÀY 03 - 2025	
					DIRECTOR - GIÁM ĐỐC ThS.KTS. ĐỖ QUỐC HIỆP		DRAWN BY - NGƯỜI VẼ KTS. TRẦN TRUNG KIẾN		DRAWING TITLE - TÊN BẢN VẼ CHI TIẾT NỘI THẤT TỦ TRANG TRÍ PN1-05		SCALE - TỈ LỆ 1:20	
									DRAWING NO. - SỐ HIỆU BẢN VẼ N1-07		KÝ HIỆU BẢNG VẼ N	

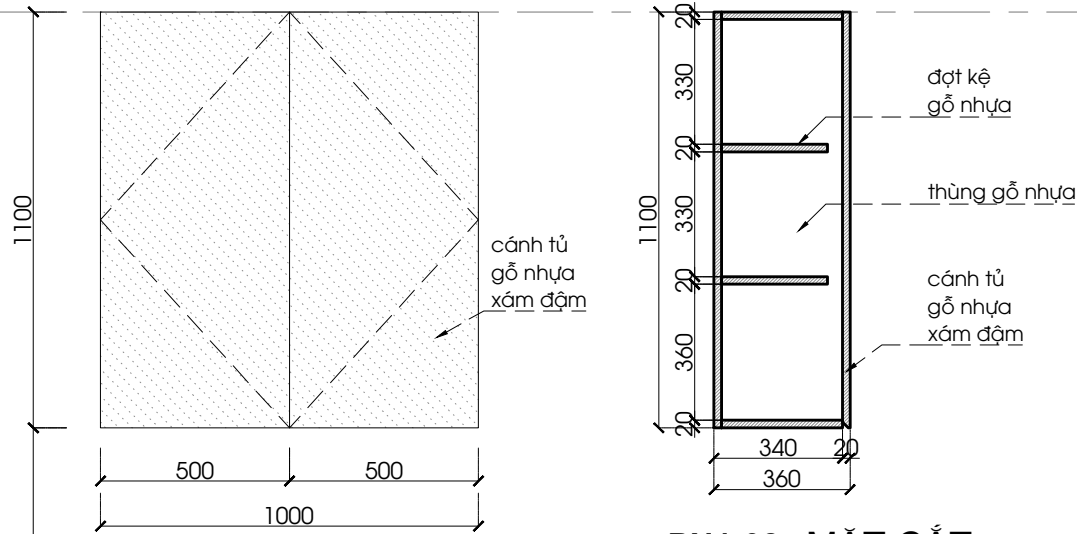


PN1-08 - MẶT CẮT
1:20 @ A3


SẴN HOÀN THIỆN

PN1-08 - MẶT ĐỪNG
1:20 @ A3


PHÁT HÀNH		HIỆU CHỈNH		GHI CHÚ - MỌI KÍCH THƯỚC CẦN ĐƯỢC KIỂM TRA THEO THỰC TẾ CÔNG TRƯỜNG	ARCHITECTURAL DESIGN — THIẾT KẾ KIẾN TRÚC CÔNG TY TNHH KIẾN TRÚC VIỆT VACO DESIGN LẦU 1, 38a PHAN VĂN ĐẠT - P. BẾN NGHÉ - Q.1 - TP. HCM TEL: +84-9-36223364 EMAIL: info@vacodesign.com DESIGN DIRECTOR - GIÁM ĐỐC ThS.KTS. ĐỖ QUỐC HIỆP		DESIGNER - CHỦ TRÌ THIẾT KẾ ThS.KTS. ĐỖ QUỐC HIỆP DRAWN BY - NGƯỜI VẼ KTS. TRẦN TRUNG KIẾN		PROJECT TITLE - TÊN DỰ ÁN CĂN HỘ 08.03- 08.04-08.05-08.06 DRAWING TITLE - TÊN BẢN VẼ CHI TIẾT NỘI THẤT TỦ LAVABO PN1-07 TỦ TRANG TRÍ WC PN1-08		DATE - NGÀY 03 - 2025 SCALE - TỈ LỆ 1:20 DRAWING NO. - SỐ HIỆU BẢN VẼ N1-08 KÝ HIỆU BẢNG VẼ N	

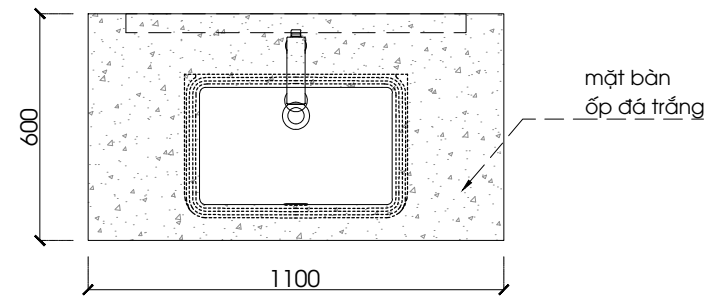


PN1-07 - MẶT BẰNG
1:20 @ A3

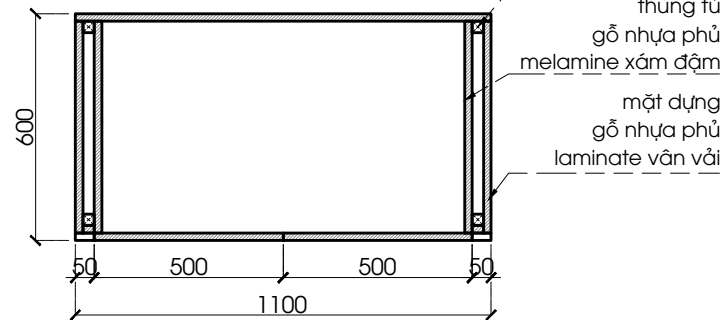

PN1-07 - MẶT CẮT NGANG
1:20 @ A3

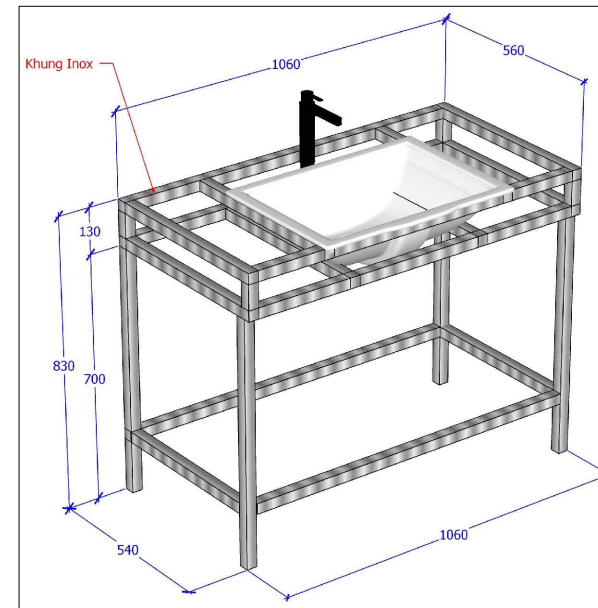


PN1-07 - PHỐI CẢNH KHUNG INOX

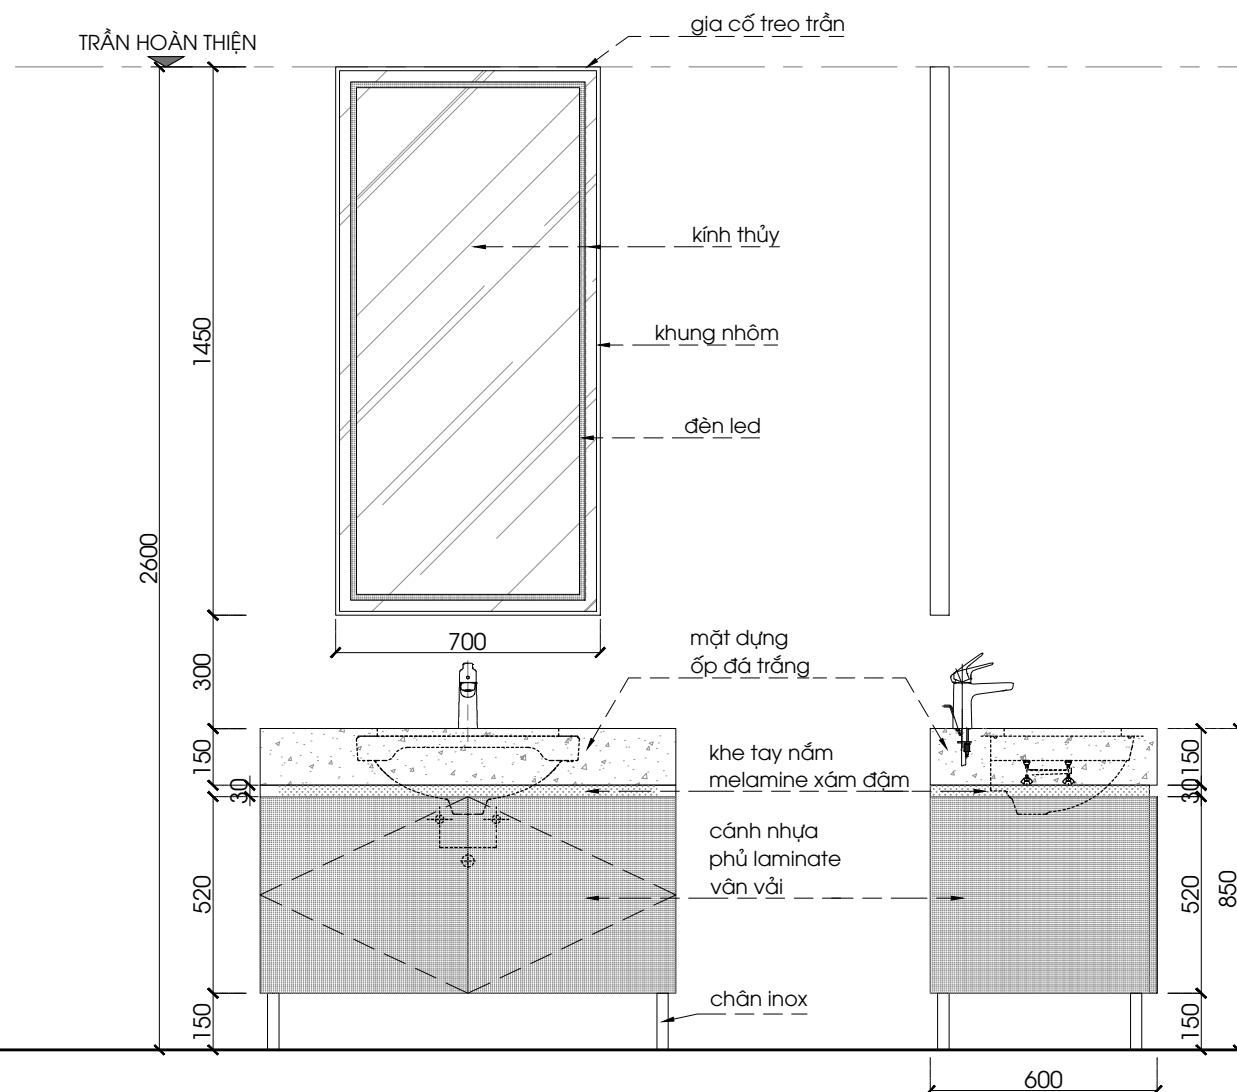

PN1-07 - MẶT ĐỨNG
1:20 @ A3


PN1-07 - MẶT ĐỨNG BÊN 1
1:20 @ A3

PN1-07 - MẶT ĐỨNG BÊN 2
1:20 @ A3

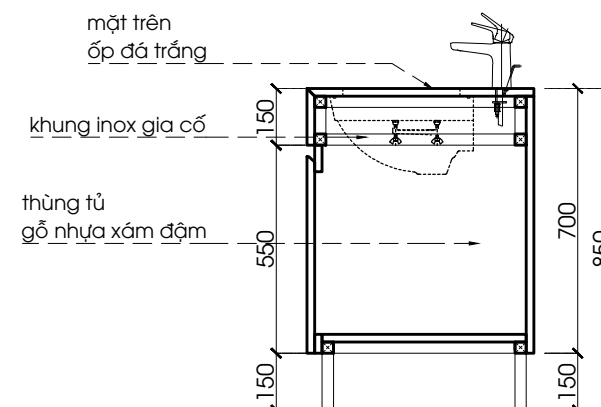


PN1-07 - MẶT CẮT
1:20 @ A3

PHÁT HÀNH		HIỆU CHÍNH		GHI CHÚ - MỌI KÍCH THƯỚC CẦN ĐƯỢC KIỂM TRA THEO THỰC TẾ CÔNG TRƯỜNG	ARCHITECTURAL DESIGN — THIẾT KẾ KIẾN TRÚC CÔNG TY TNHH KIẾN TRÚC VIỆT VACO DESIGN LẦU 1, 3bis PHAN VĂN ĐẠT - P. BẾN NGHÉ - Q.1 - TP. HCM TEL: +84-9-36223364 EMAIL: info@vacodesign.com	DESIGNER - CHỦ TRÌ THIẾT KẾ ThS.KTS. ĐỖ QUỐC HIỆP	PROJECT TITLE - TÊN DỰ ÁN CĂN HỘ 08.03- 08.04-08.05-08.06	DATE - NGÀY 03 - 2025	
								SCALE - TỈ LỆ 1:20	
								DRAWING NO. - SỐ HIỆU BẢN VẼ N1-08a	KÝ HIỆU BẢNG VẼ N
					ThS.KTS. ĐỖ QUỐC HIỆP	KTS. TRẦN TRUNG KIẾN	DRAWING TITLE - TÊN BẢN VẼ CHI TIẾT NỘI THẤT TỦ LAVABO PN1-07 TỦ TRANG TRÍ WC PN1-08		

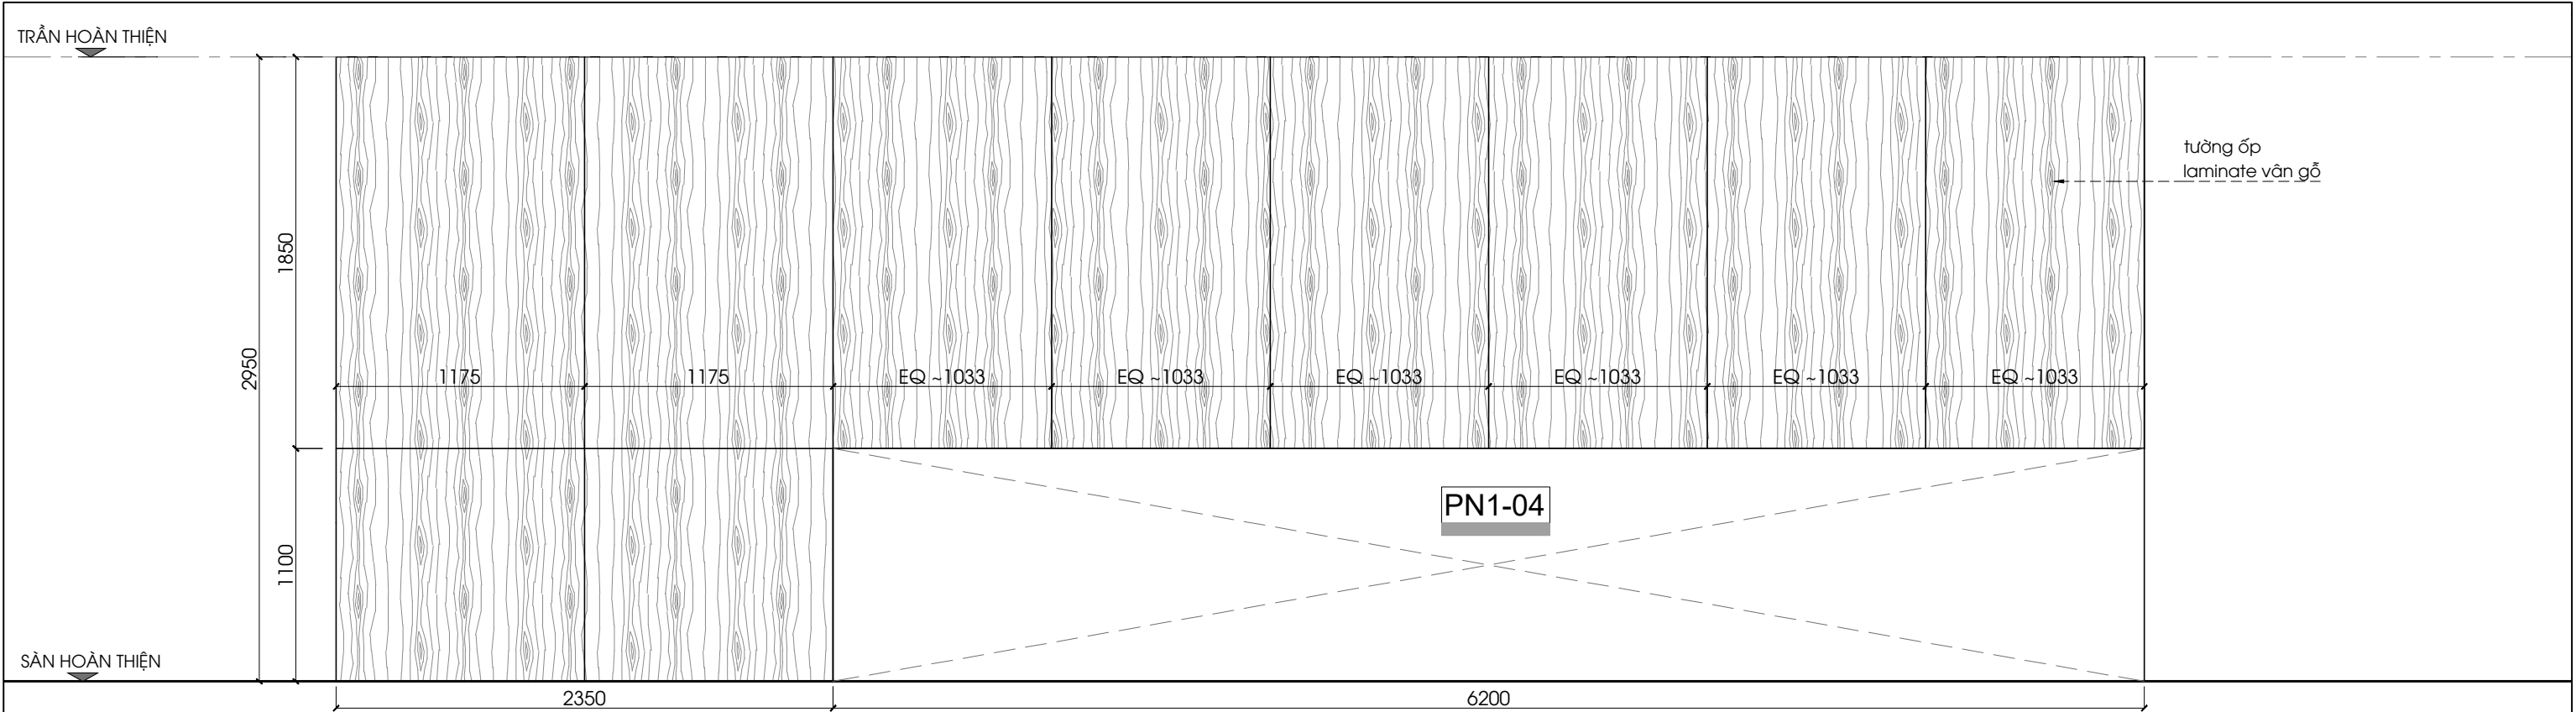

PN1-V1 - MẶT ĐỨNG

1:30 @ A3

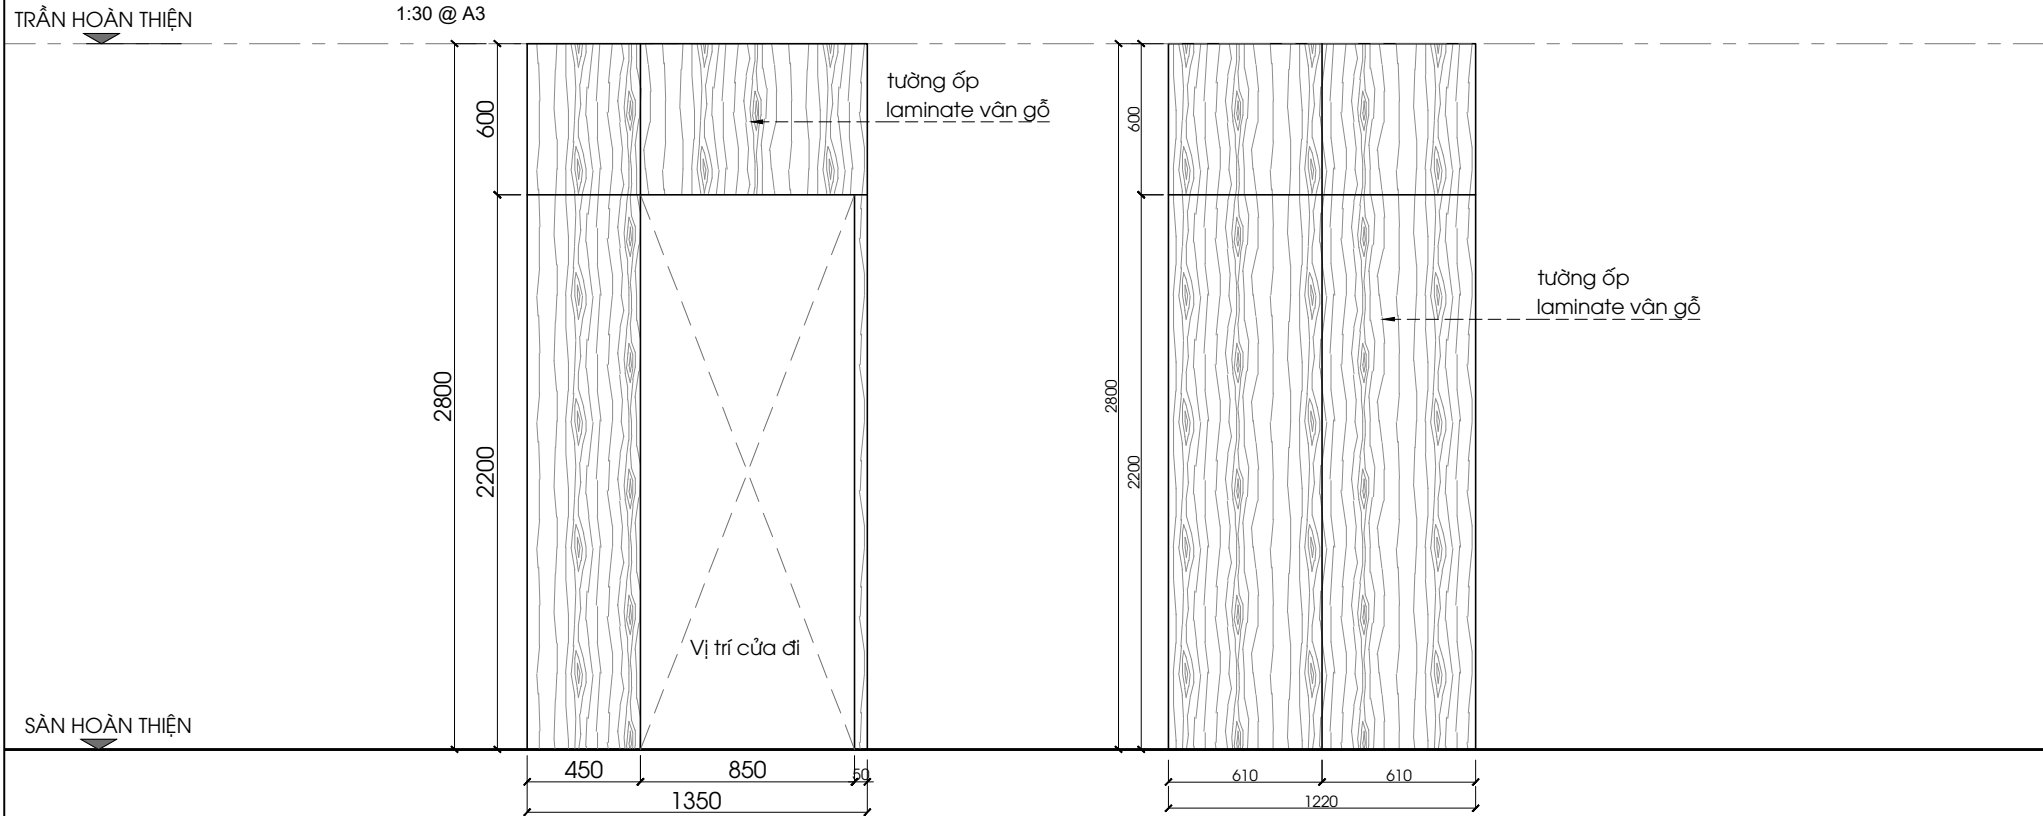

PN1-V2 - MẶT ĐỨNG

1:30 @ A3

PN1-V3 - MẶT ĐỨNG

1:30 @ A3

PHÁT HÀNH		HIỆU CHÍNH		GHI CHÚ	ARCHITECTURAL DESIGN — THIẾT KẾ KIẾN TRÚC		DESIGNER - CHỦ TRÌ THIẾT KẾ		PROJECT TITLE - TÊN DỰ ÁN		DATE - NGÀY	
					CÔNG TY TNHH KIẾN TRÚC VIỆT VACO DESIGN LẦU 1, 3bis PHAN VĂN ĐẠT - P. BẾN NGHÉ - Q.1 - TP. HCM TEL: +84-9-36223364 EMAIL: info@vacodesign.com				CĂN HỘ 08.03- 08.04-08.05-08.06		03 - 2025	
								ThS.KTS. ĐỖ QUỐC HIỆP	SCALE - TỈ LỆ		1:30	
									DRAWING TITLE - TÊN BẢN VẼ		DRAWING NO. - SỐ HIỆU BẢN VẼ	
									CHI TIẾT NỘI THẤT		N1-09	
									VÁCH ỐP PN1-V1, PN1-V2, PN1-V3		KỶ HIỆU BẢNG VẼ	
				- MỌI KÍCH THƯỚC CẦN ĐƯỢC KIỂM TRA THEO THỰC TẾ CÔNG TRƯỜNG	ThS.KTS. ĐỖ QUỐC HIỆP	DIRECTOR - GIÁM ĐỐC	KTS. TRẦN TRUNG KIẾN	DRAWN BY - NGƯỜI VẼ			N	